10-7 GROUNDS

All wires are 57 (BK) unless otherwise noted.
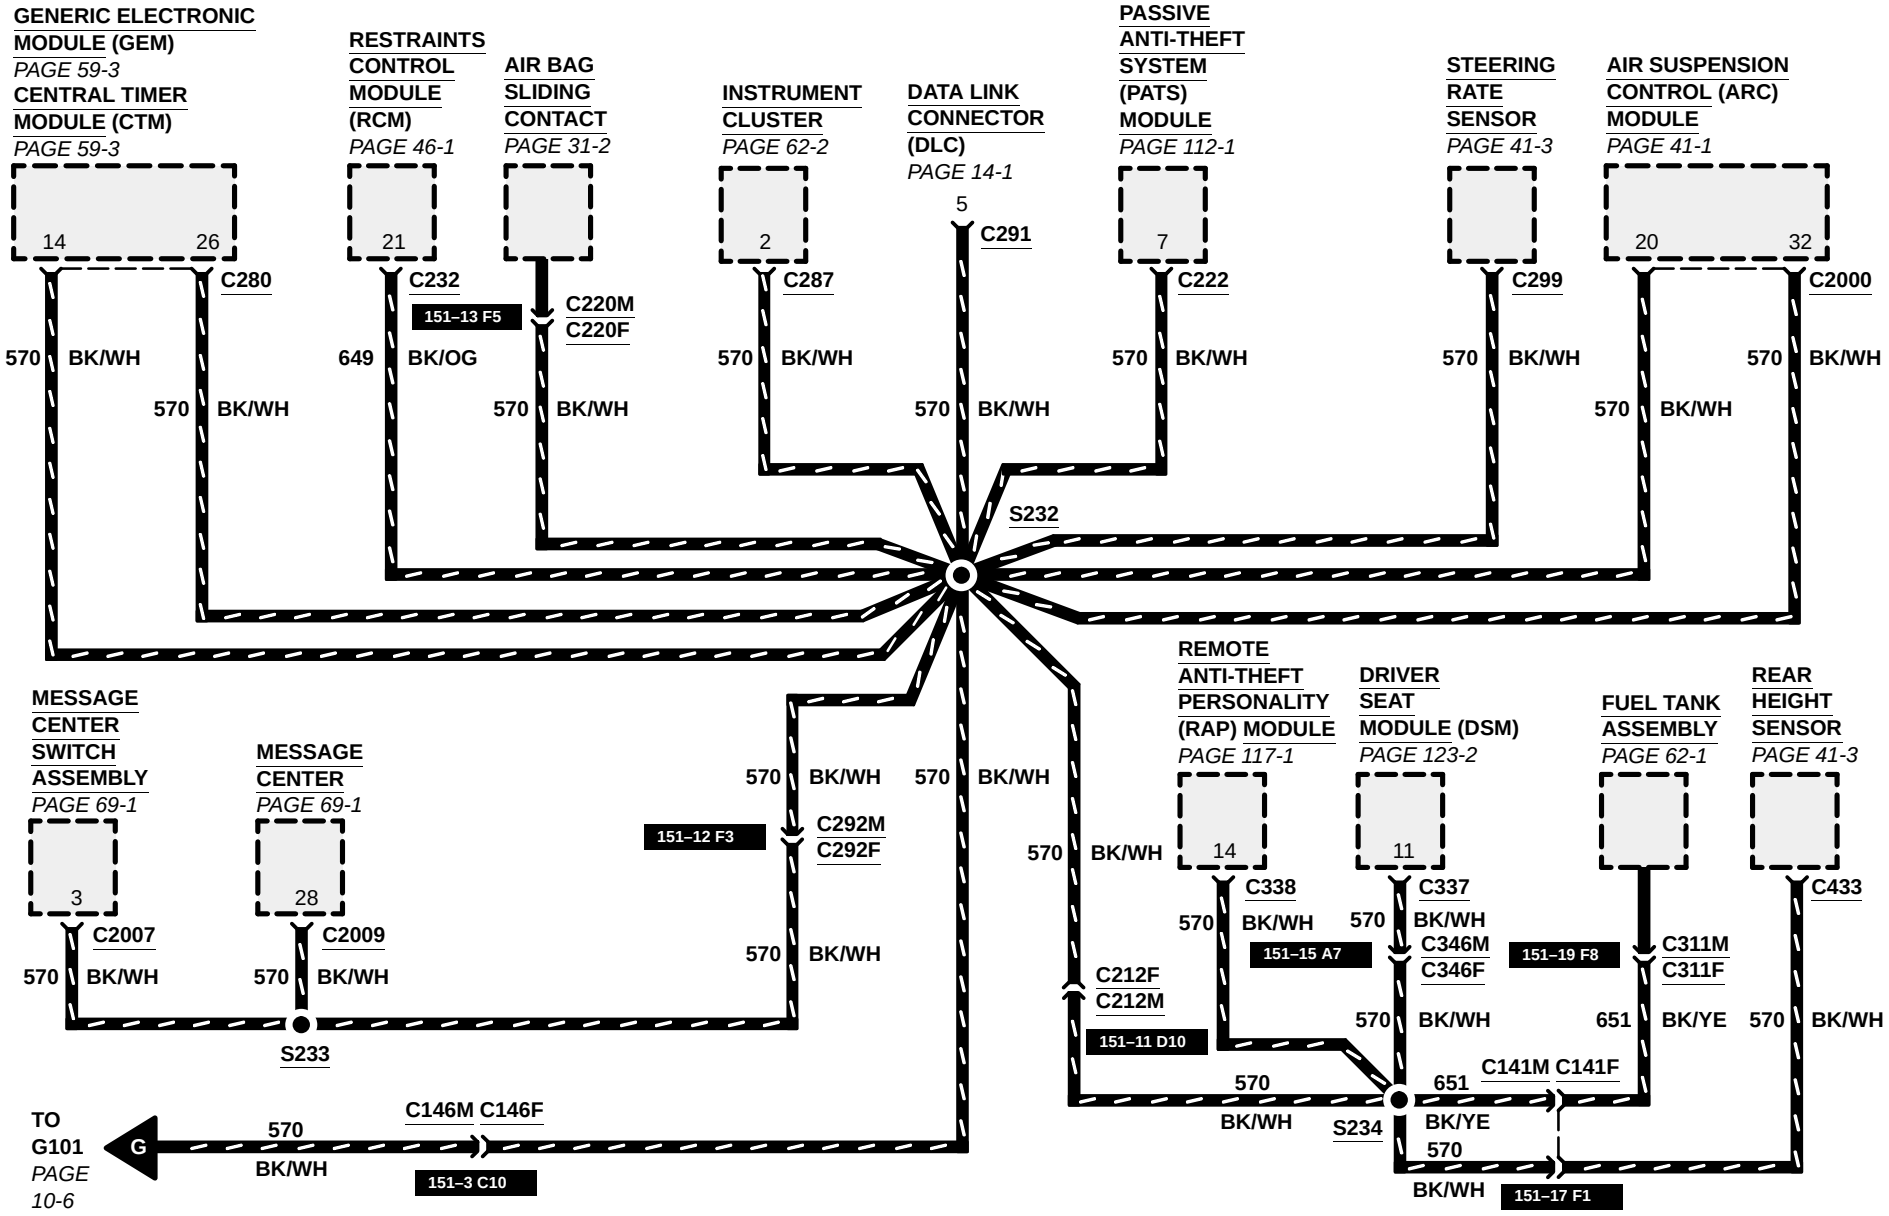
G101