10-9 GROUNDS

All Circuits are 57 BK unless otherwise noted.

***W/O REMOTE KEYLESS ENTRY**
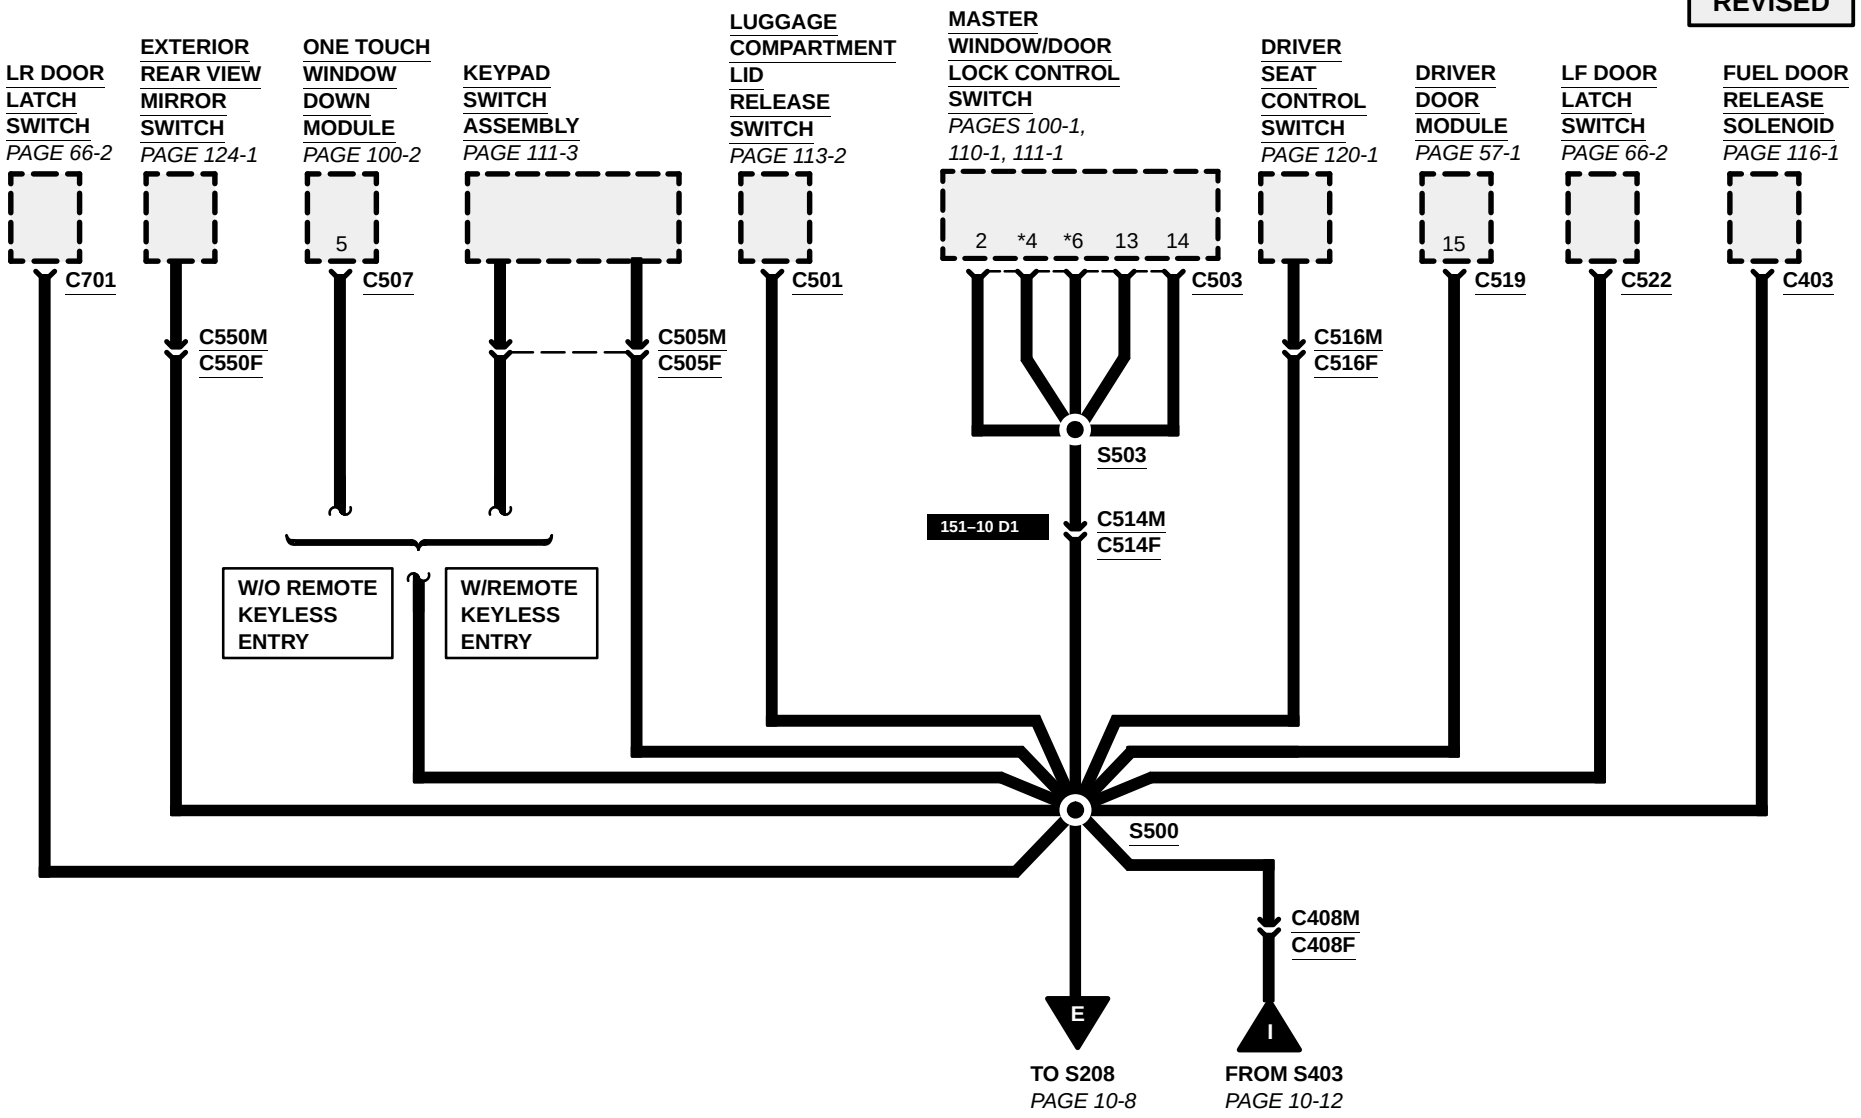
REVISED