10-11 GROUNDS
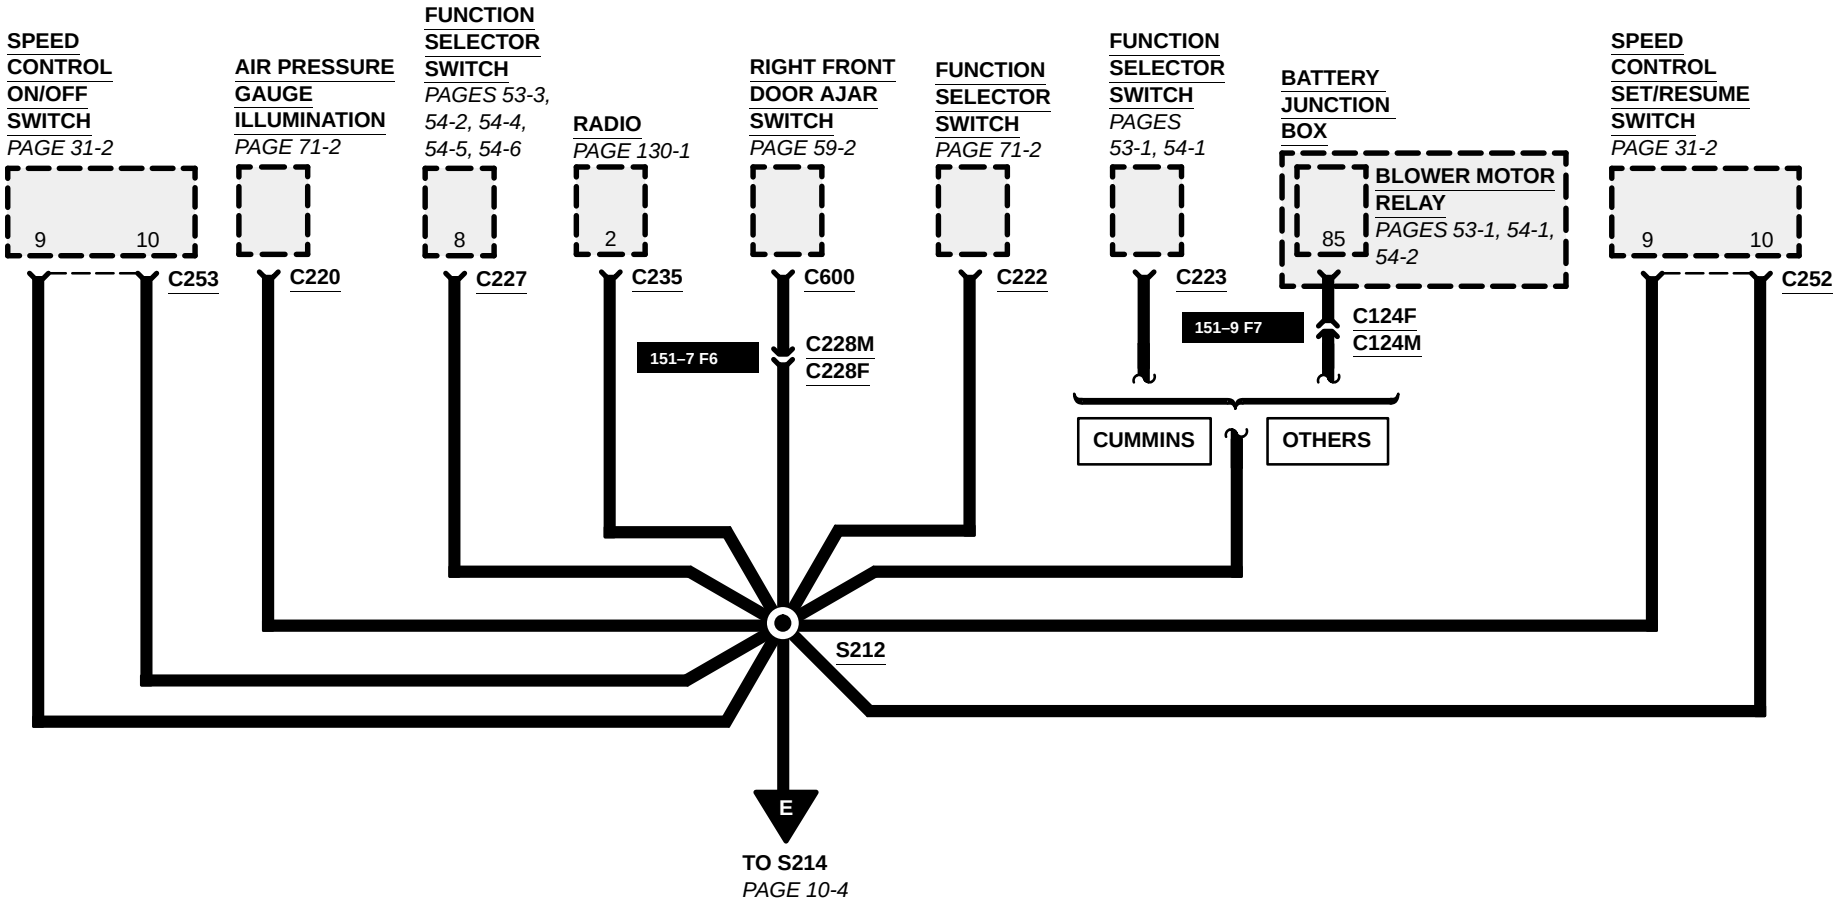
All wires are 57 (BK) unless otherwise noted.