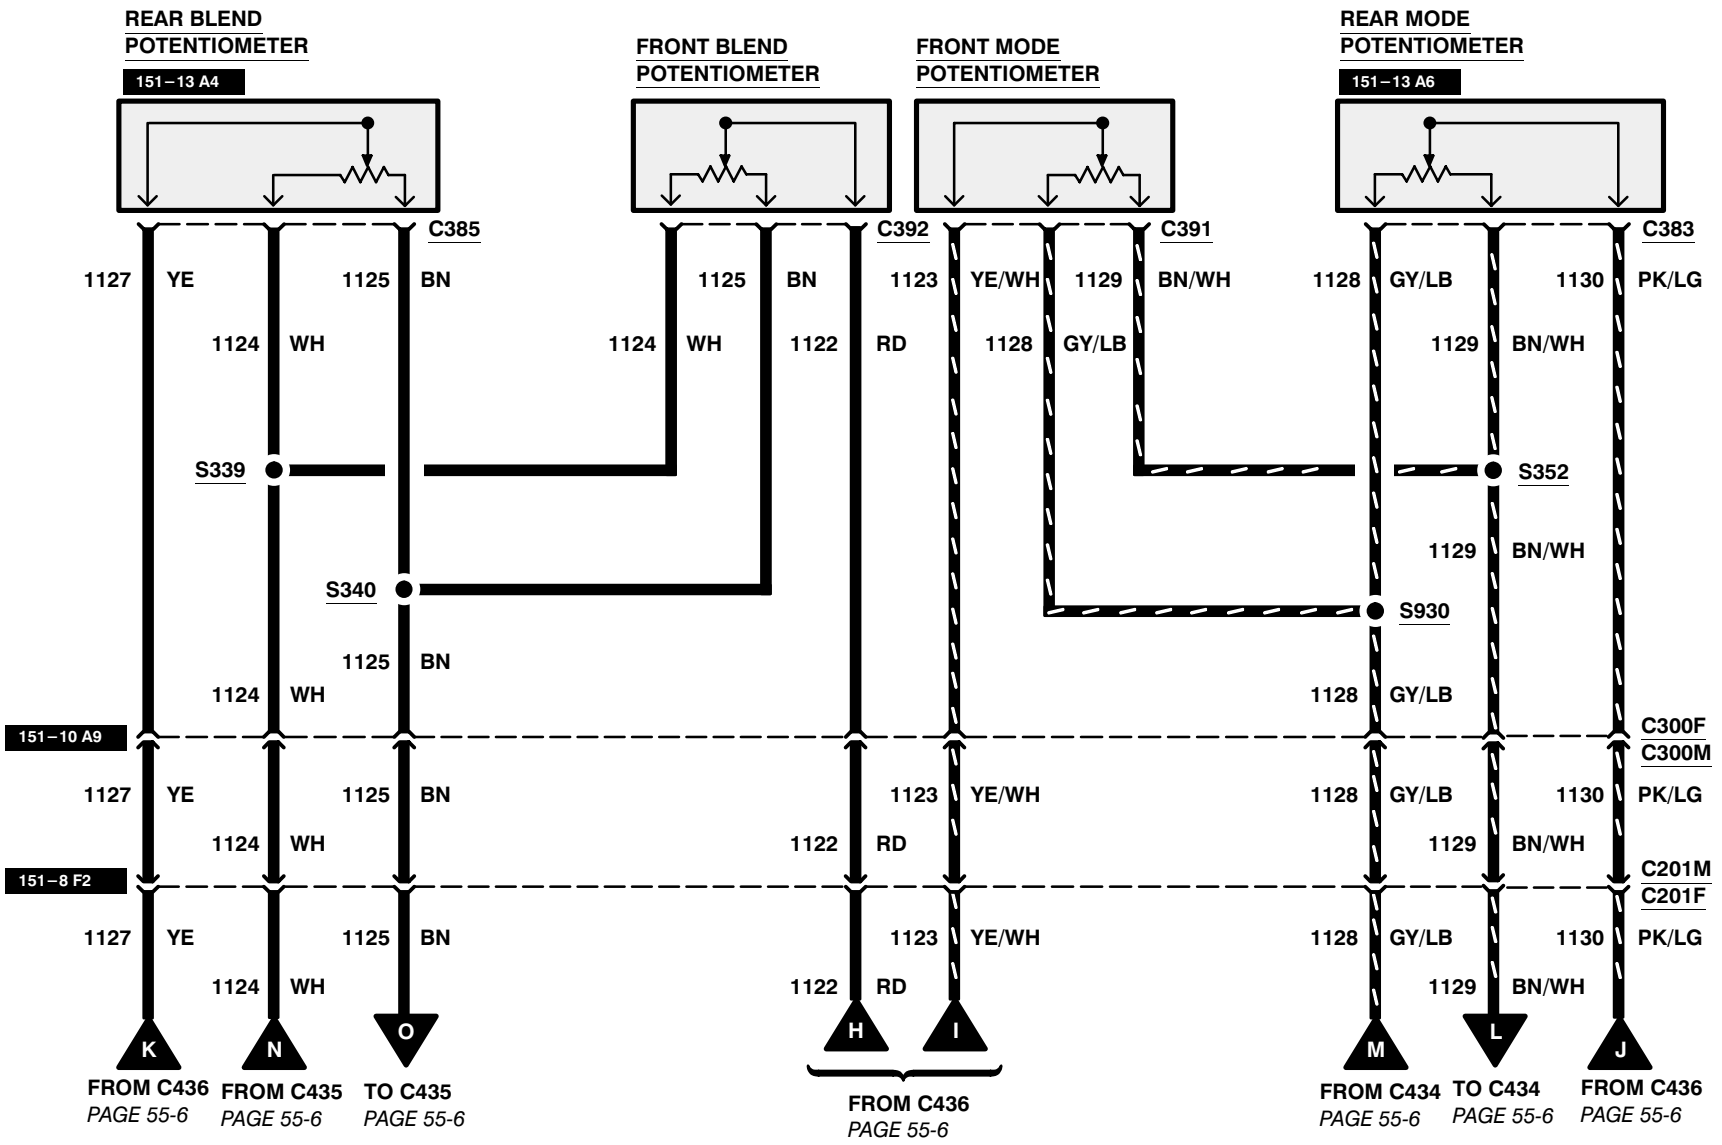## EXPEDITION W/ROOF OPENING PANEL