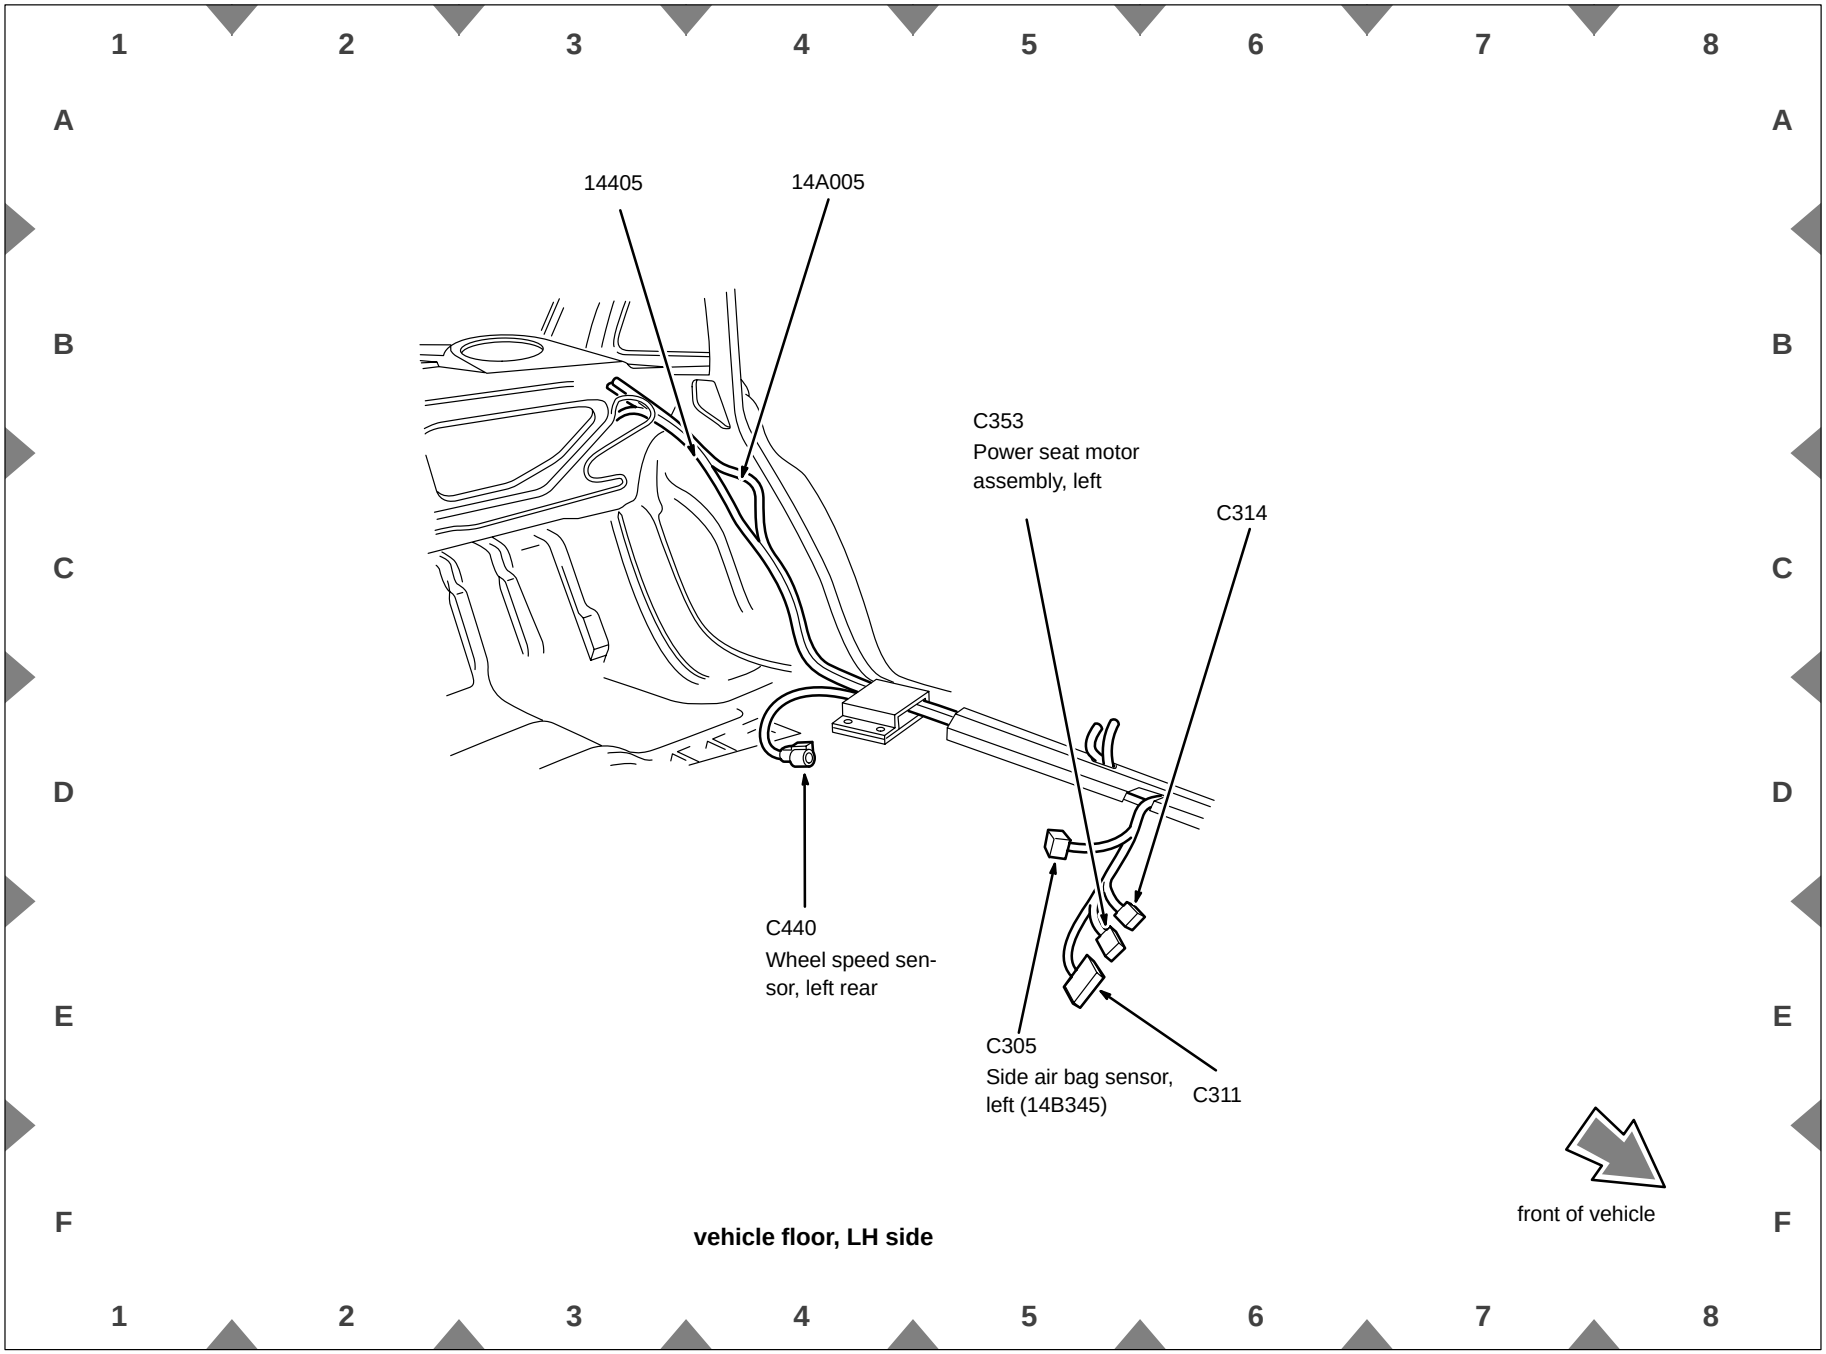

vehicle floor, LH side