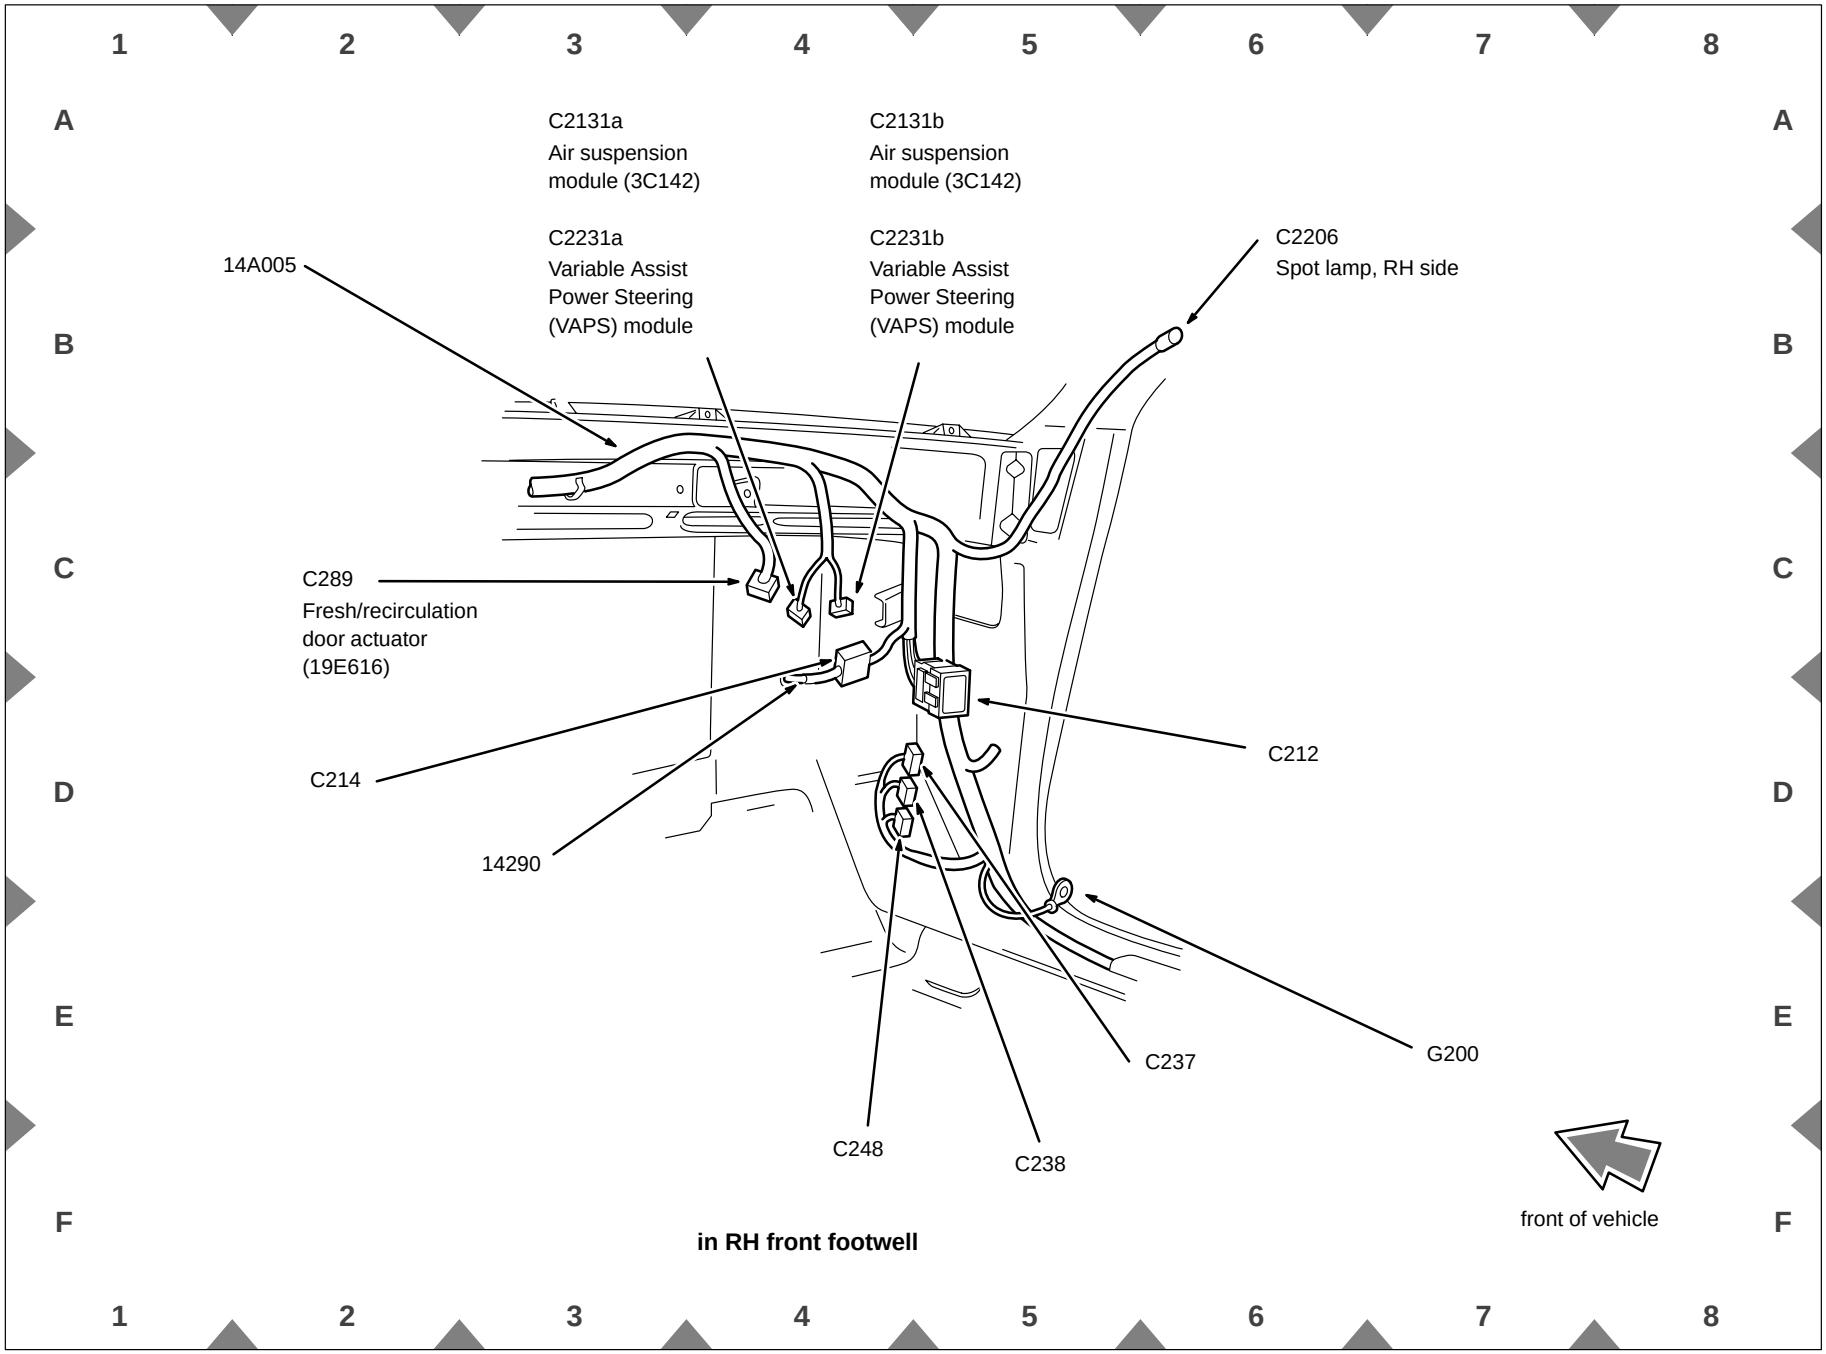

in RH front footwell