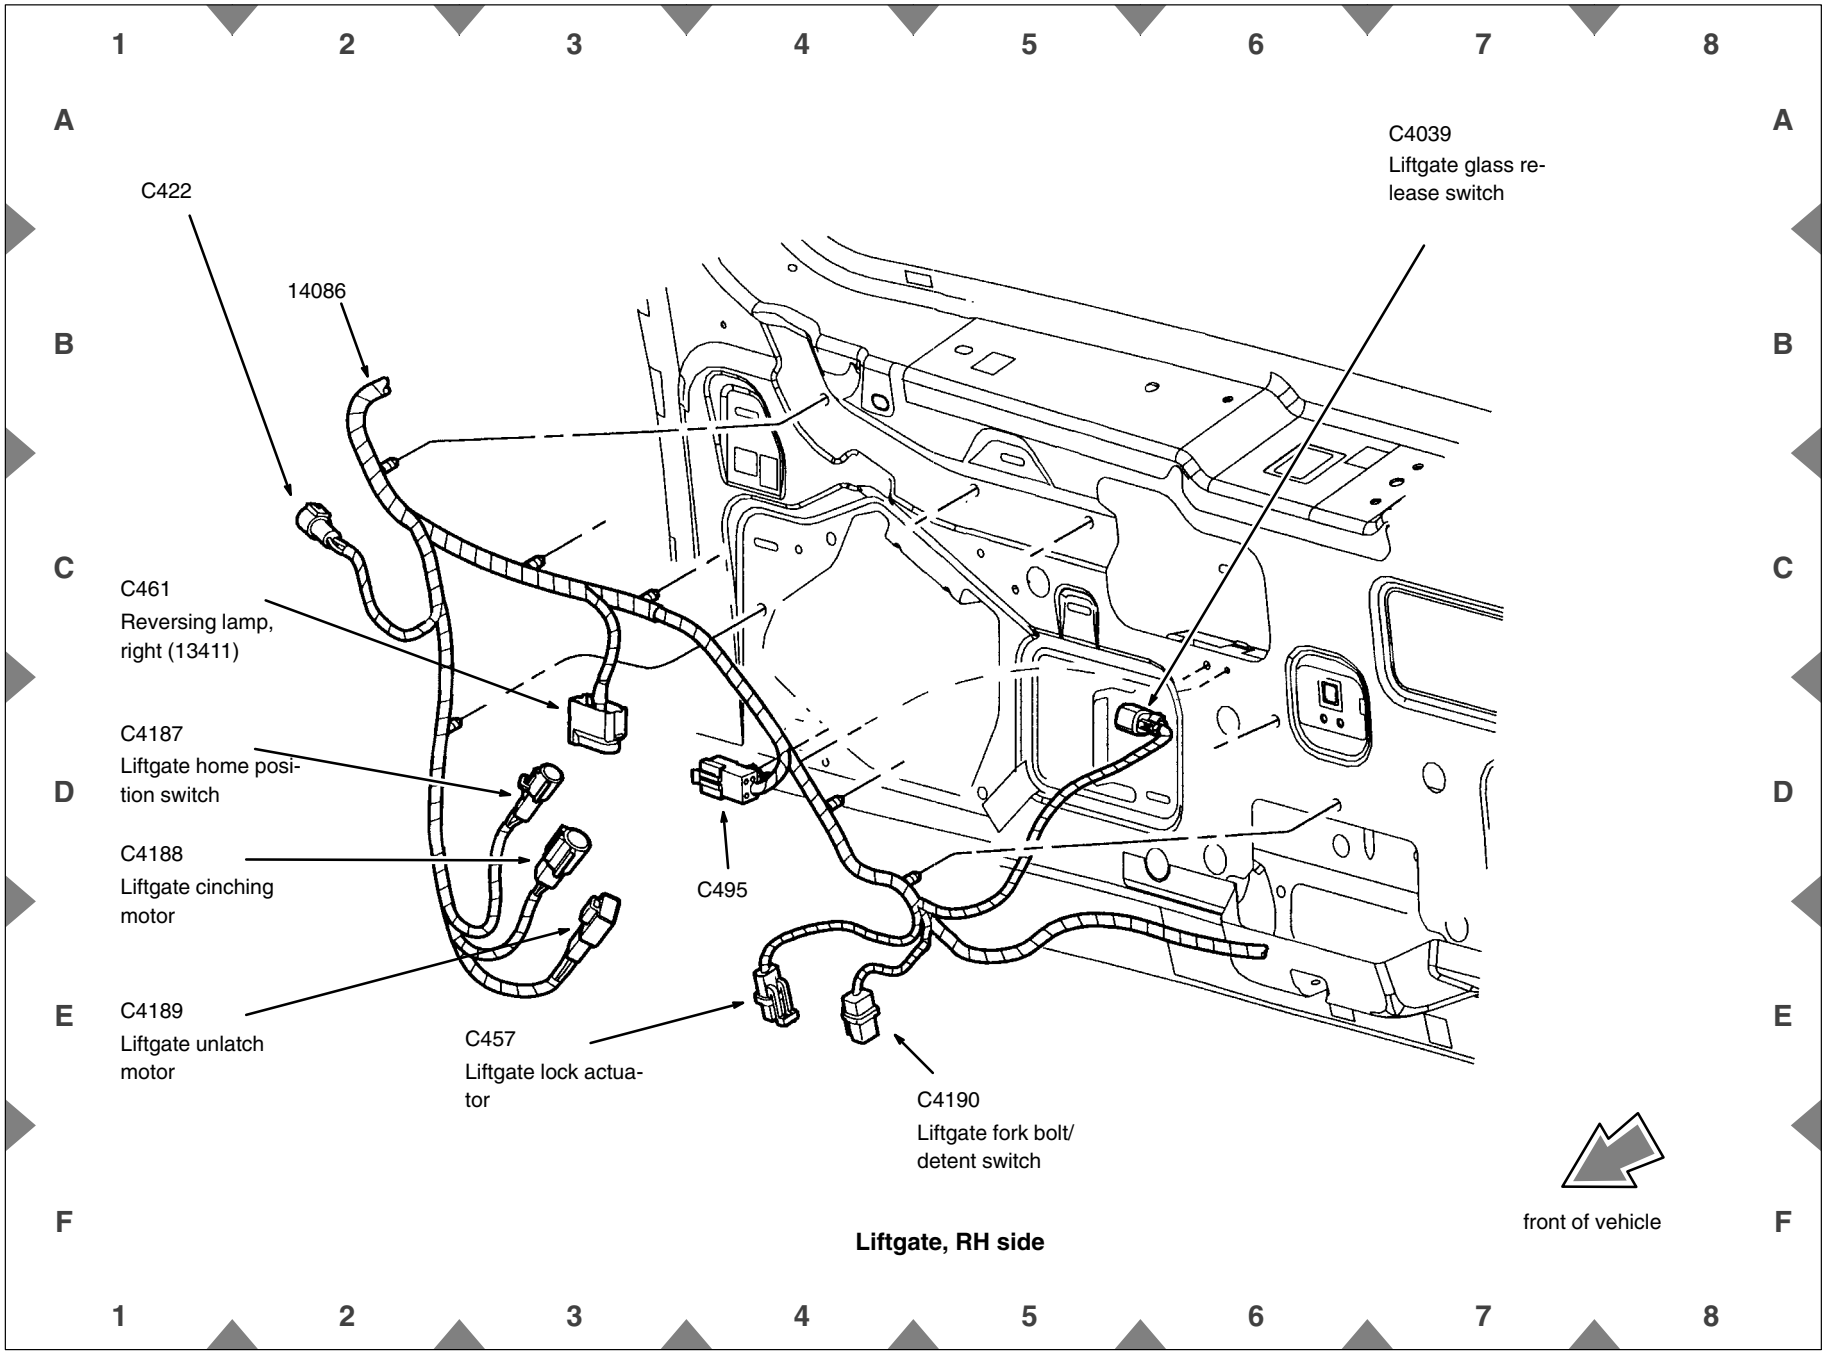

Liftgate, RH side