10-3 GROUNDS

All wires are 57 (BK) unless otherwise noted.
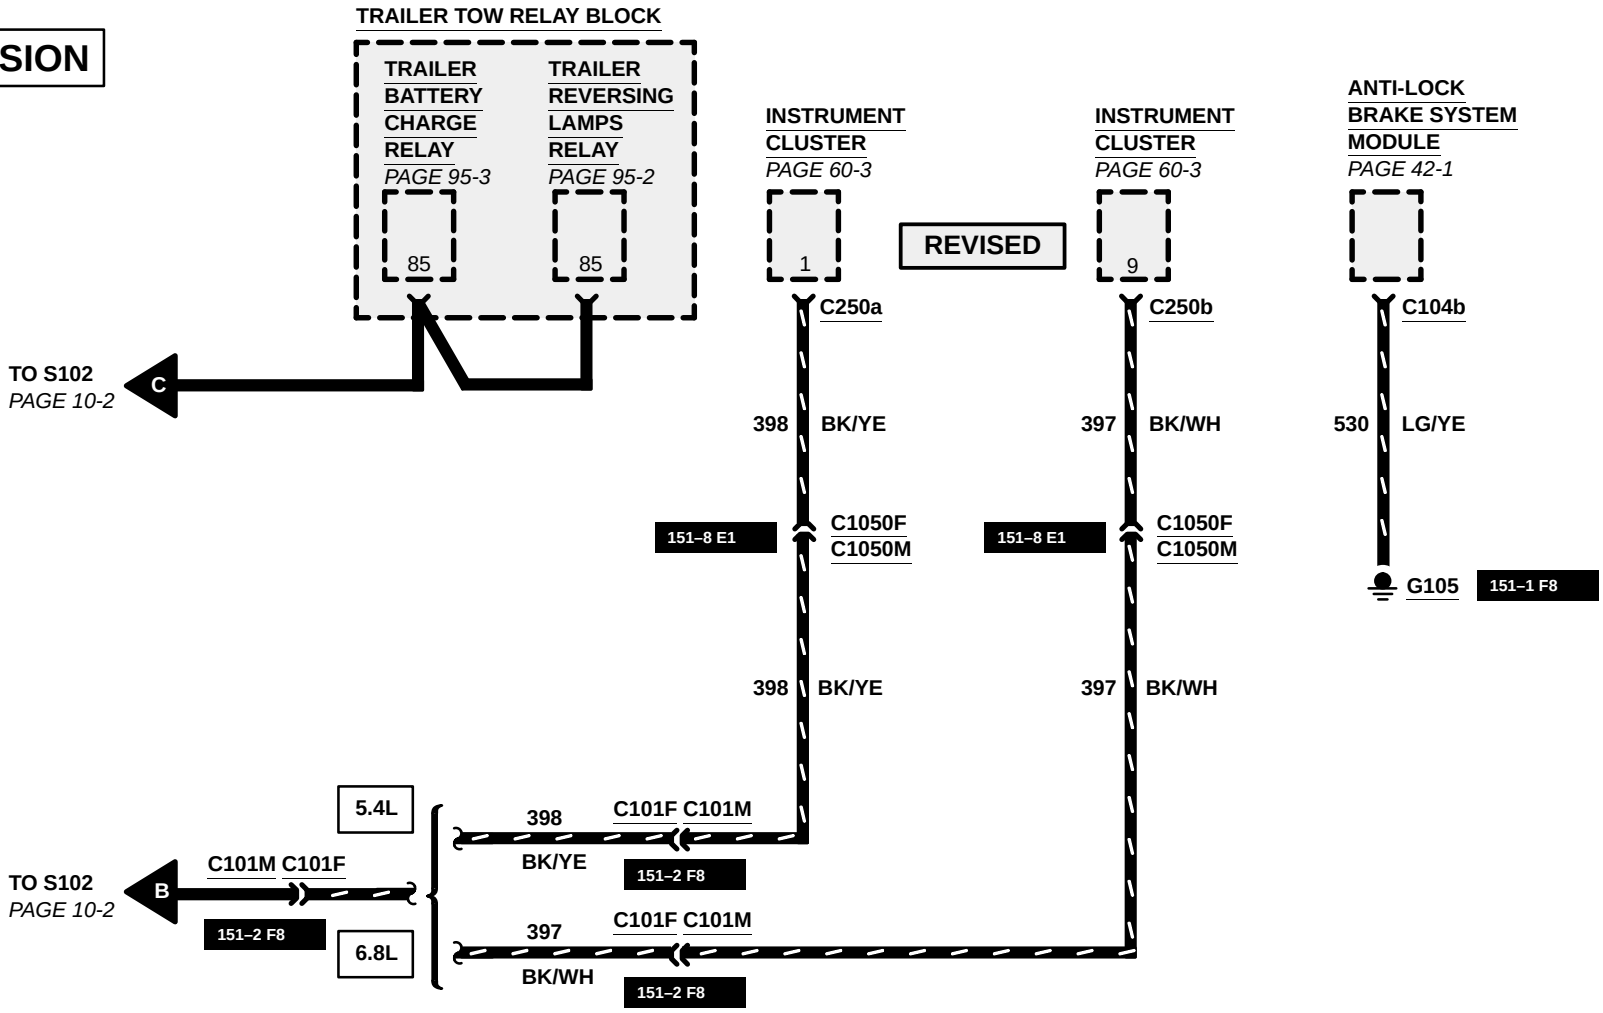
EXCURSION