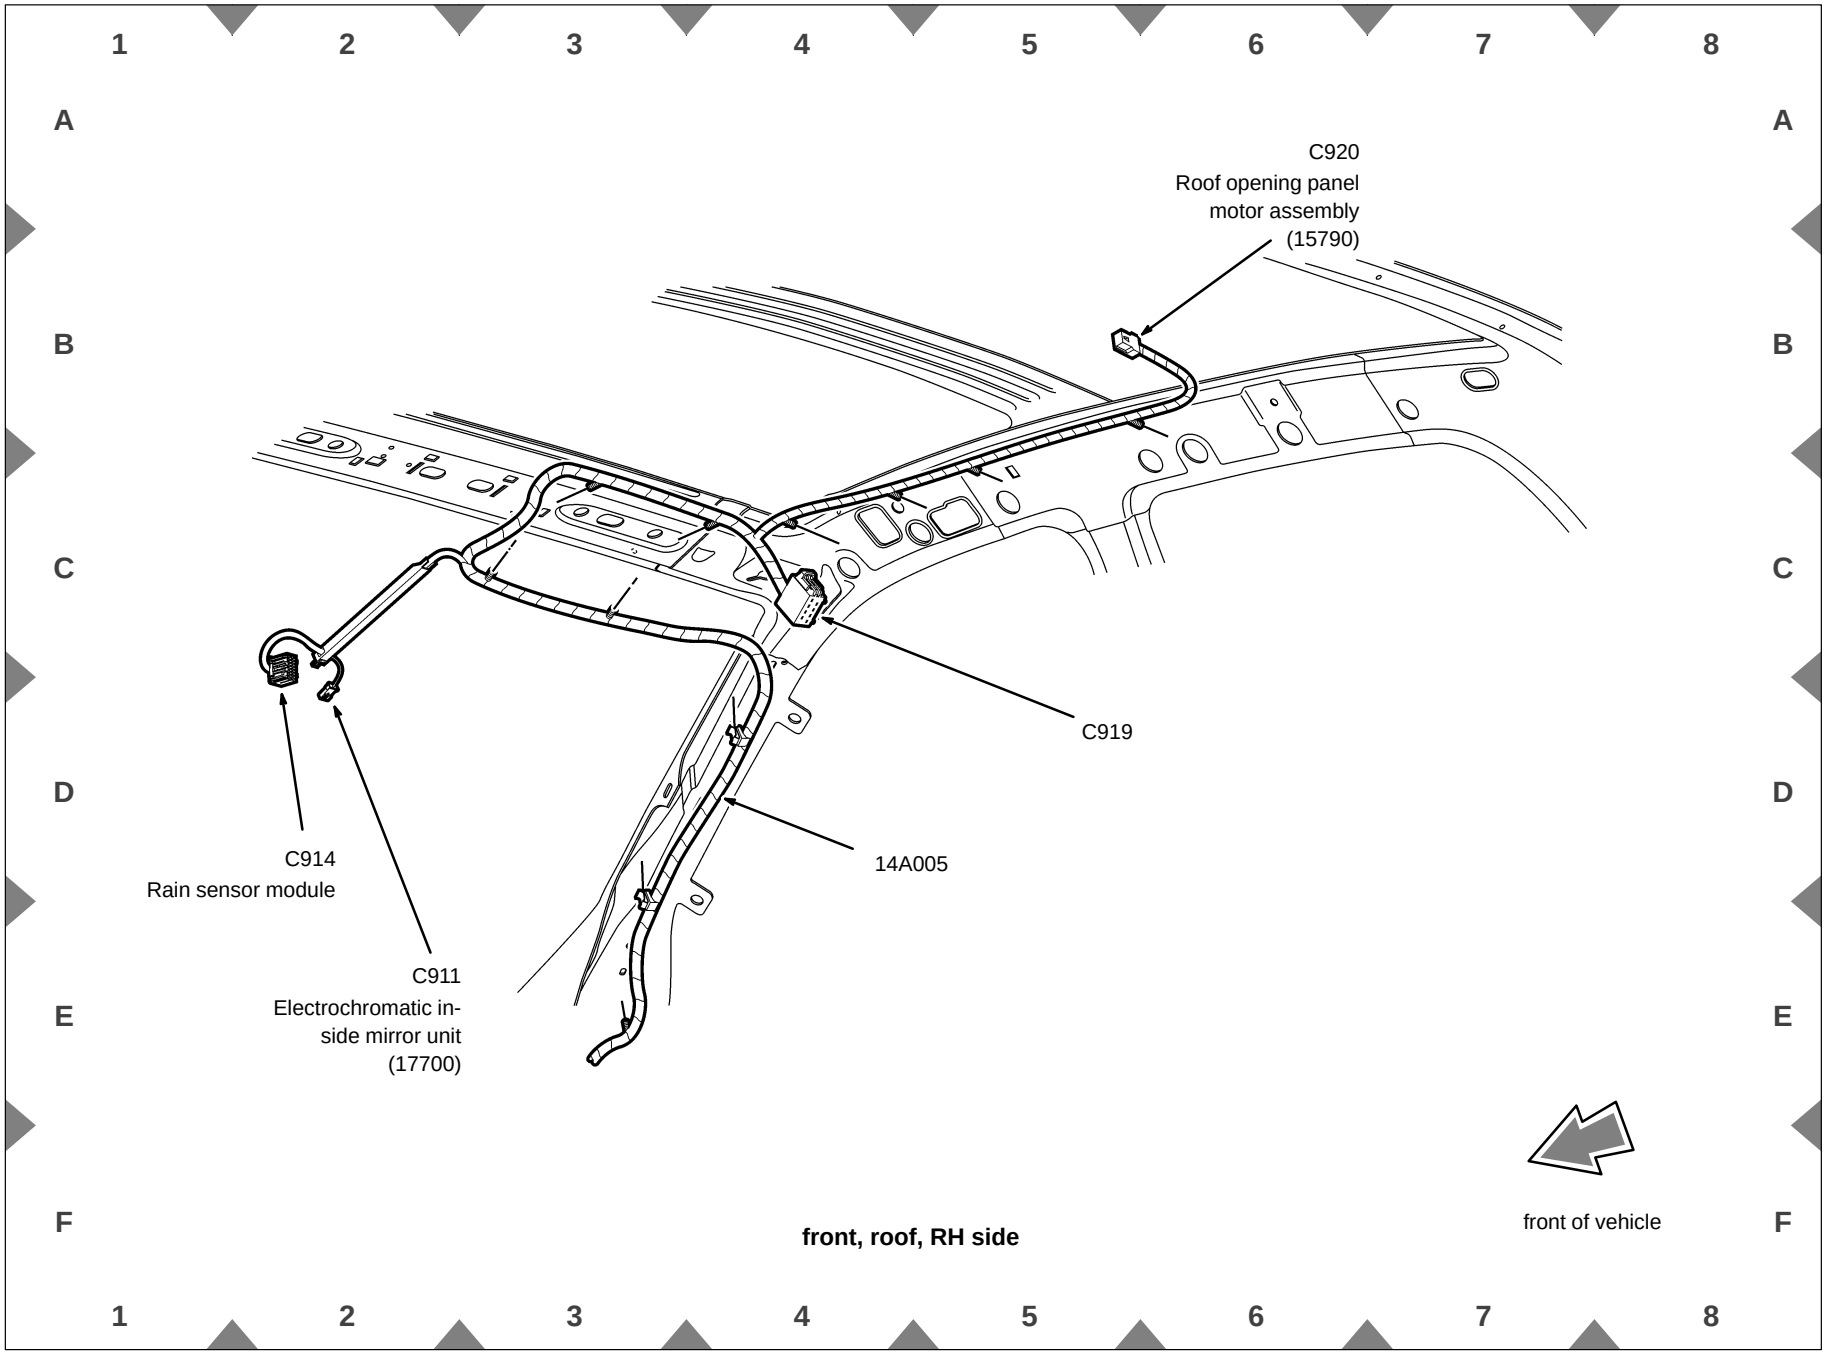

front, roof, RH side