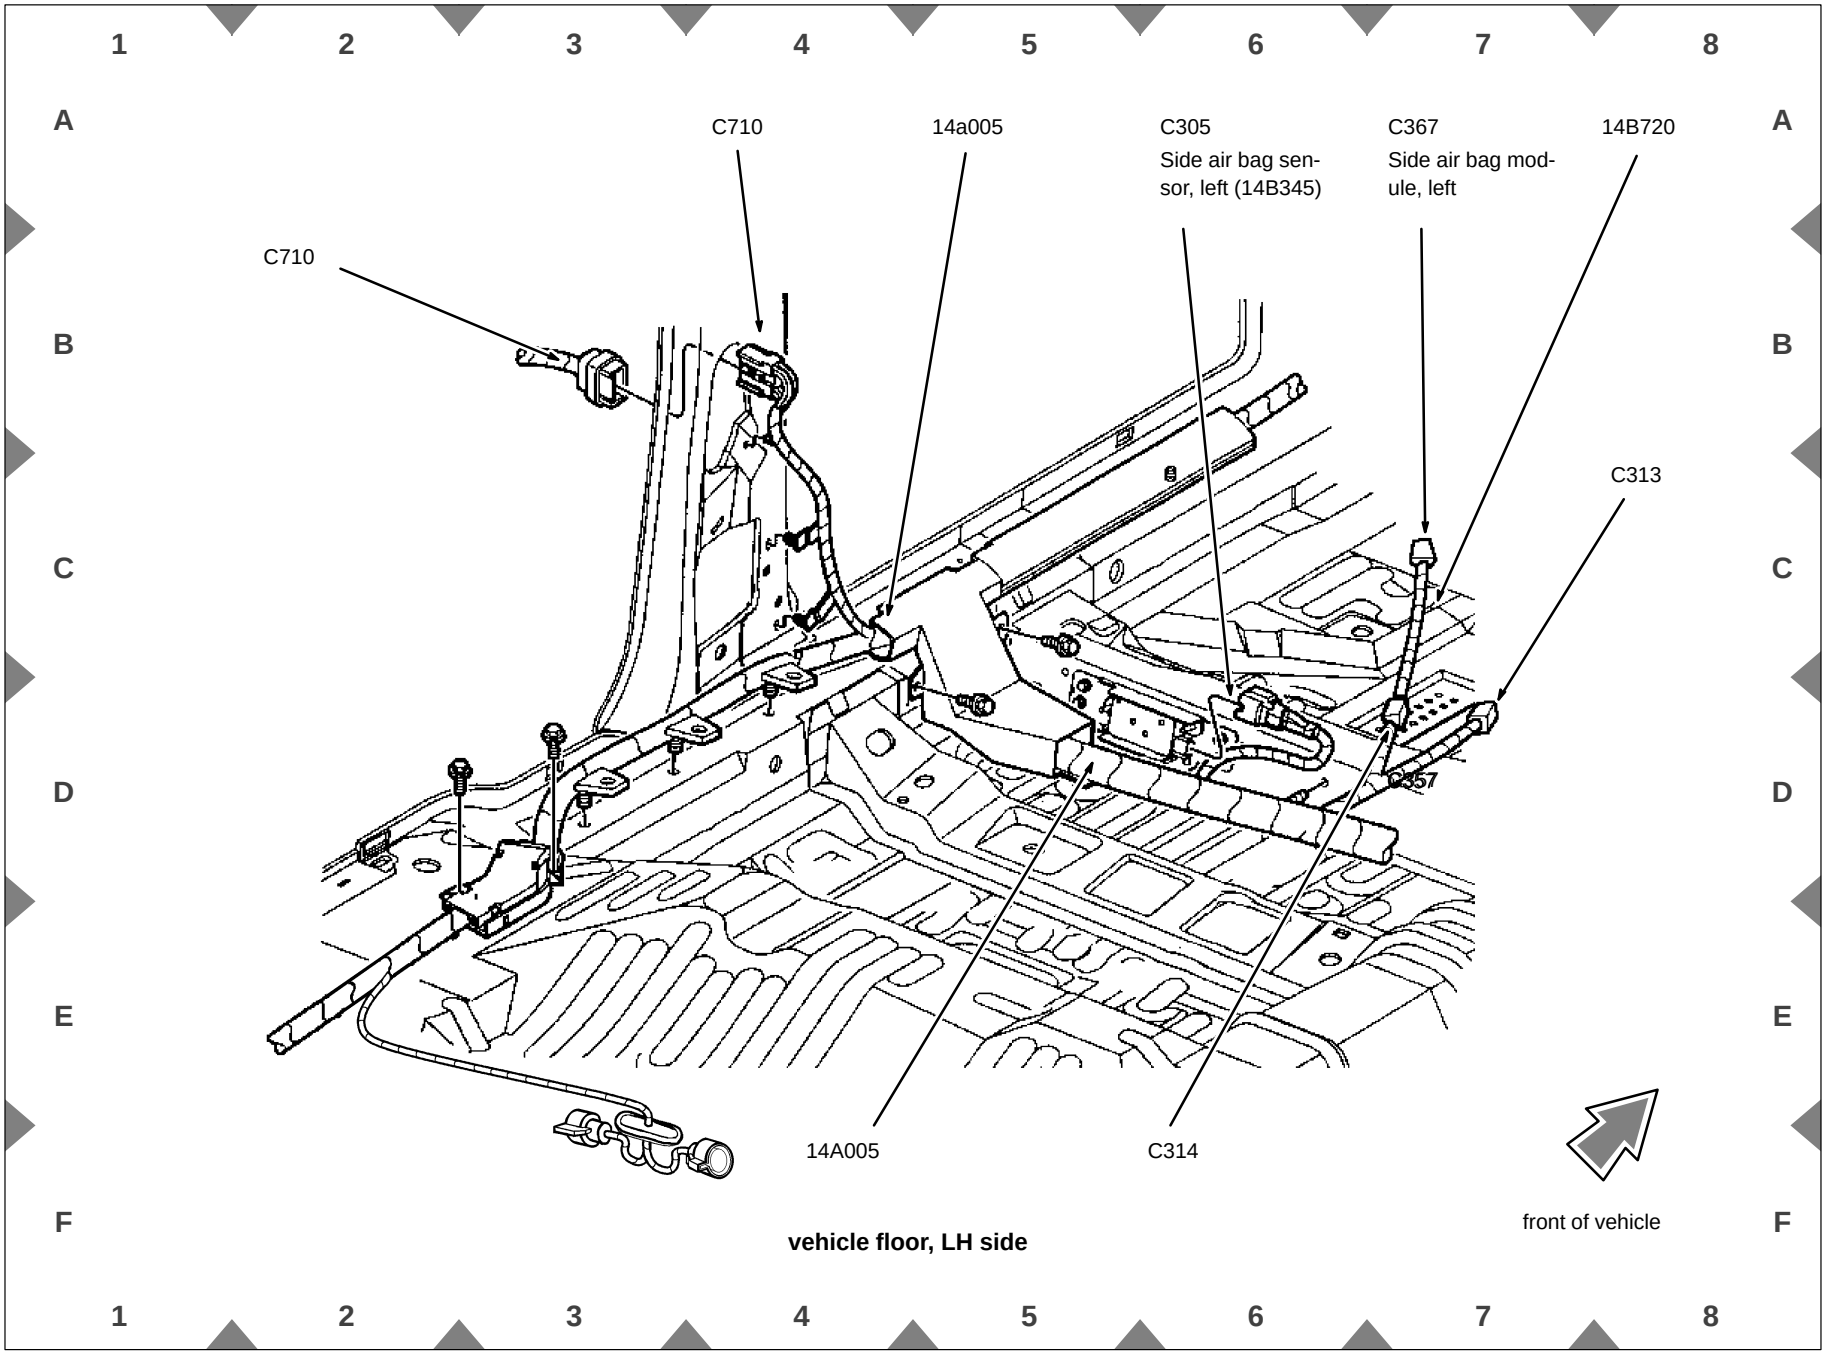


vehicle floor, LH side