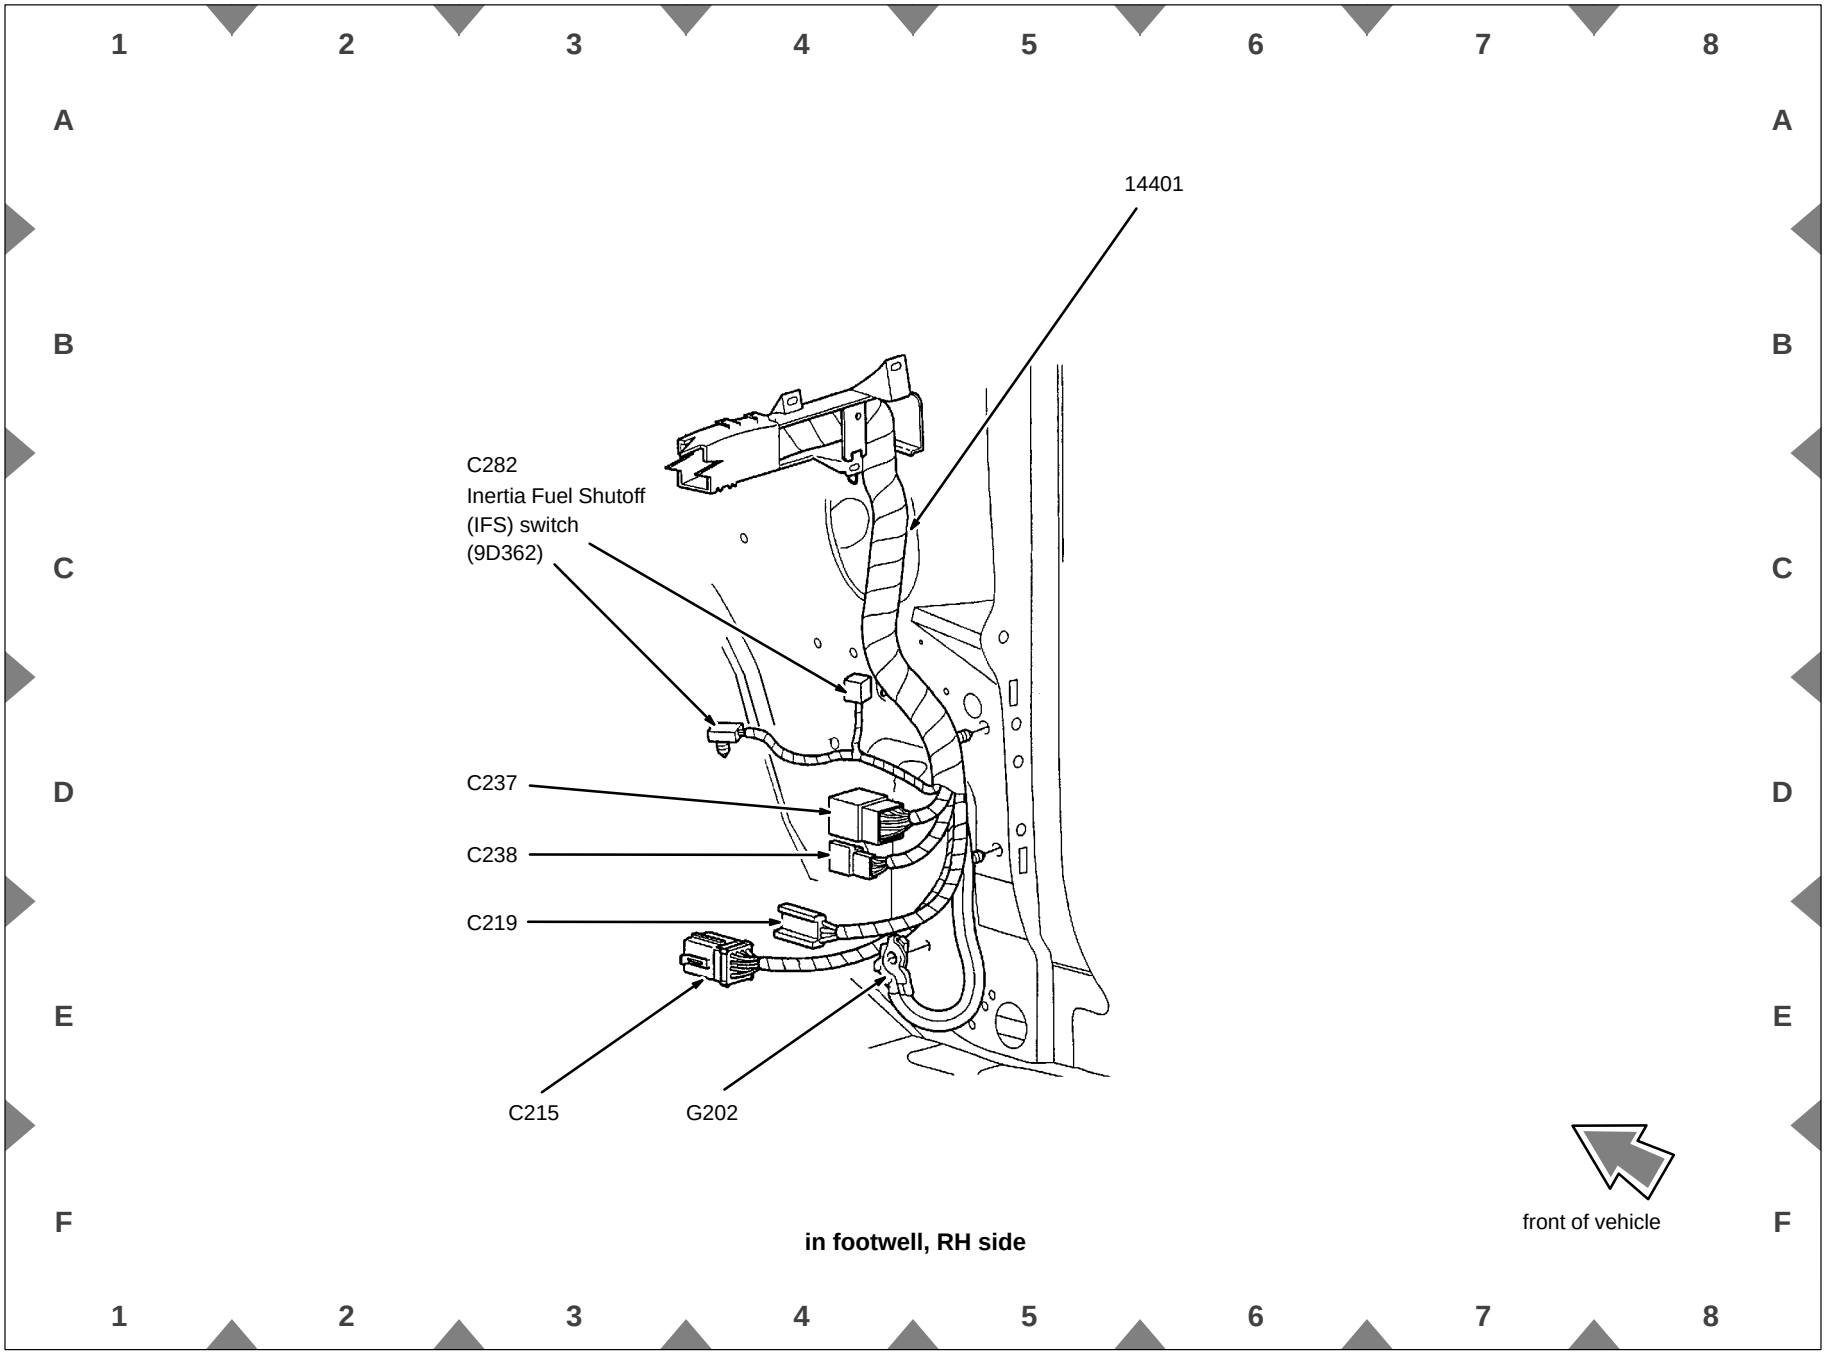

in footwell, RH side