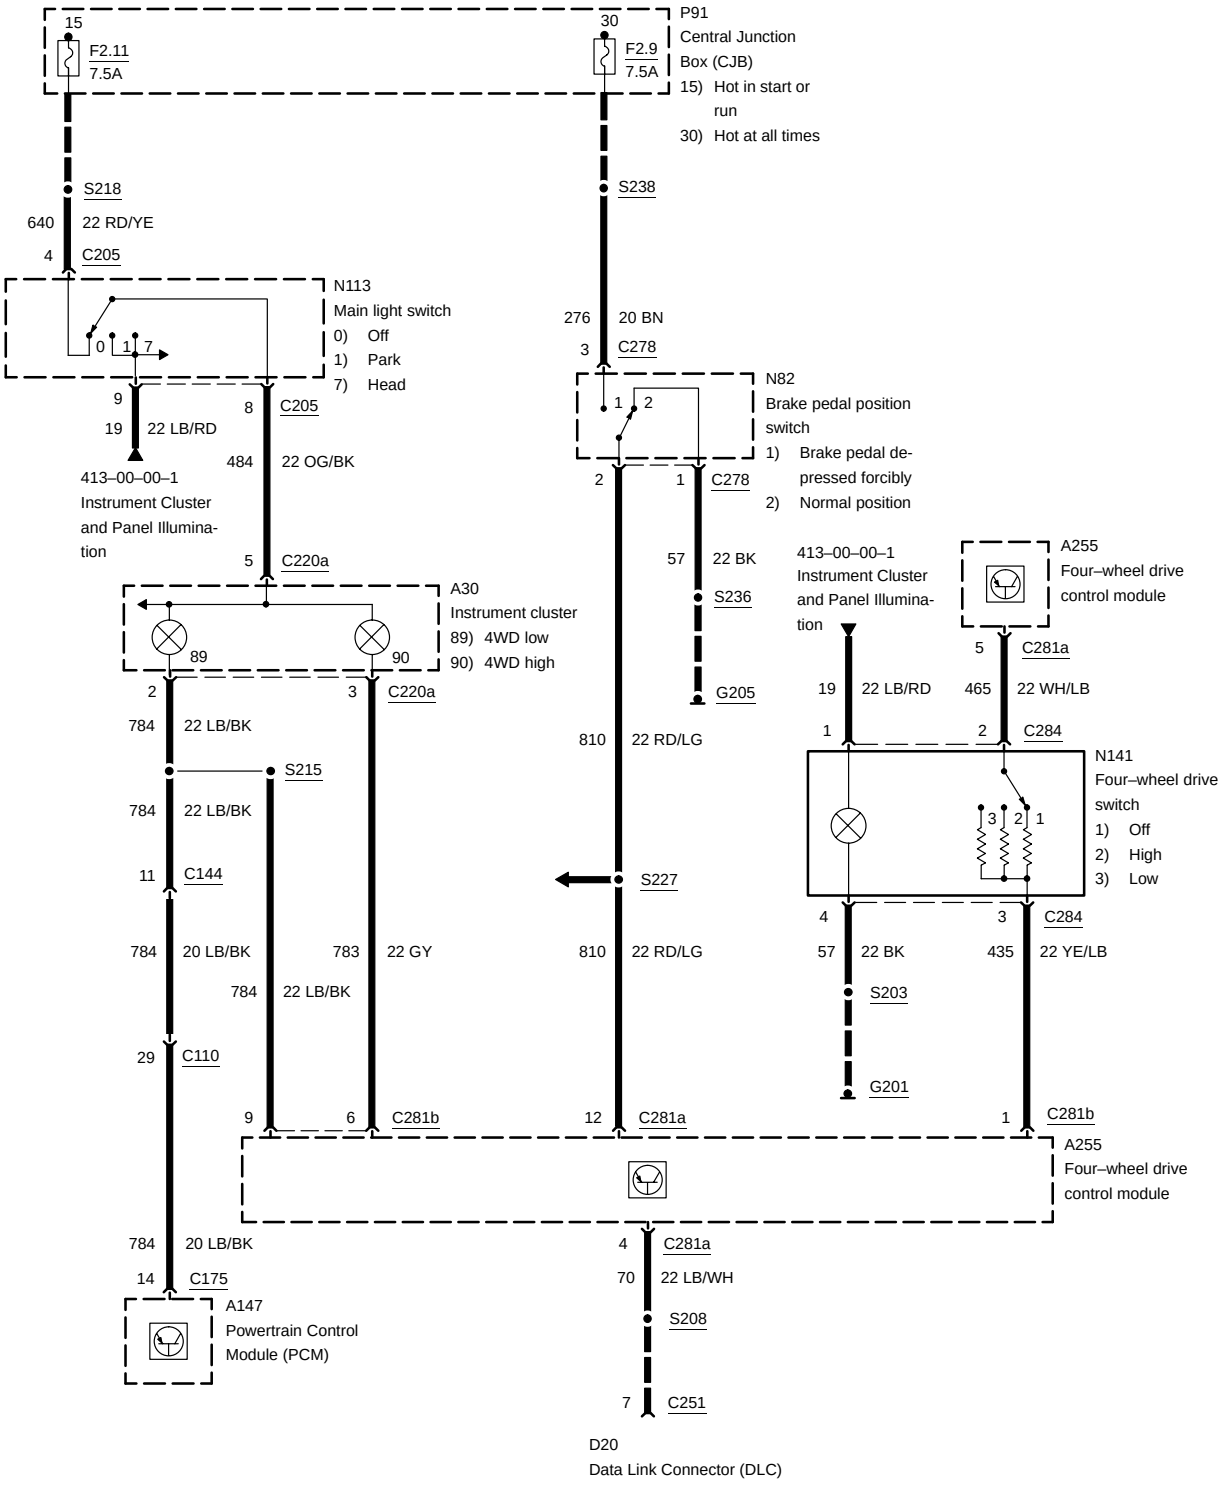Regular 4x4 -2