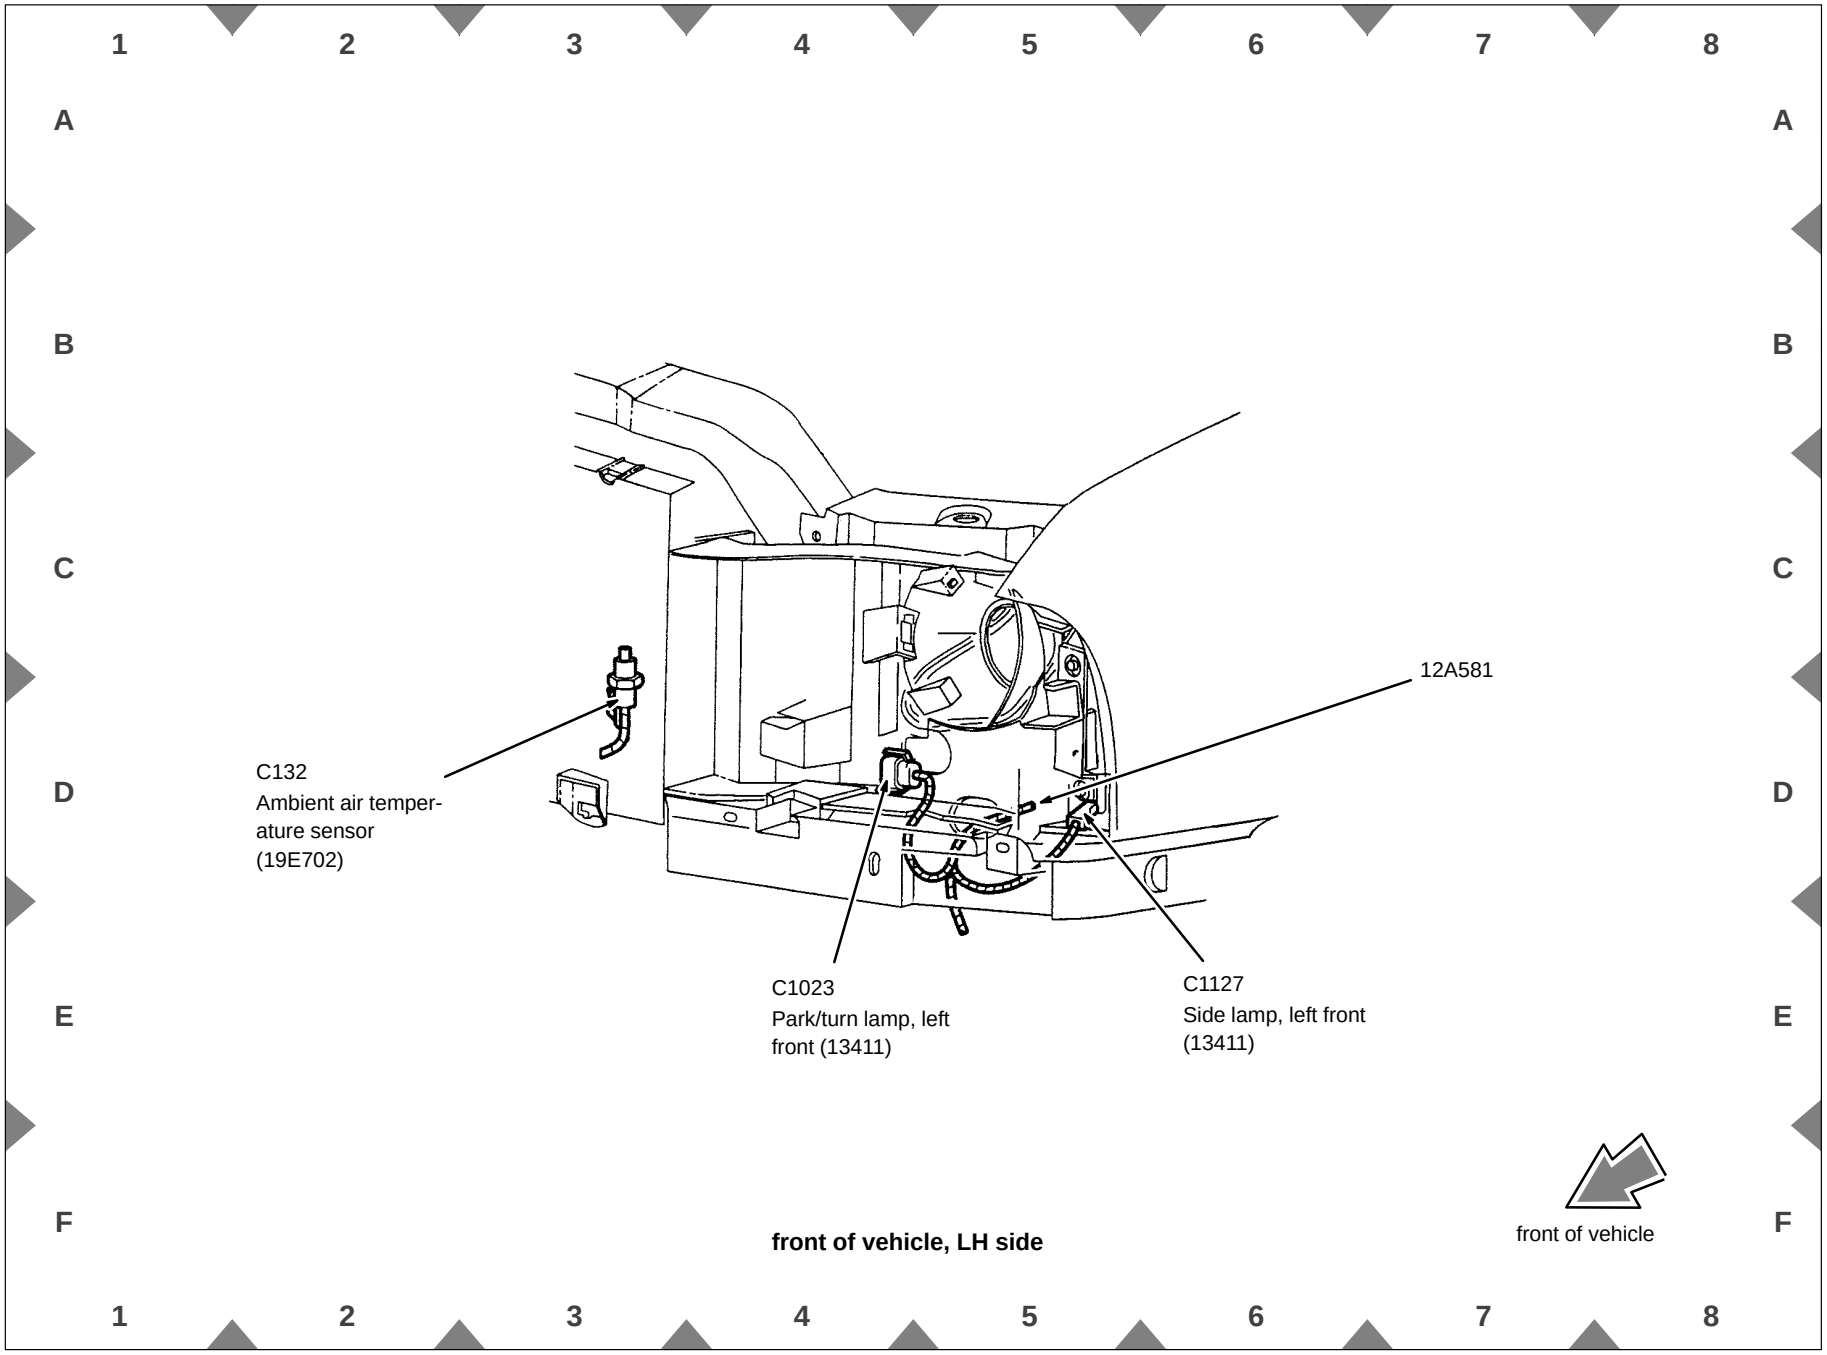

front of vehicle, LH side