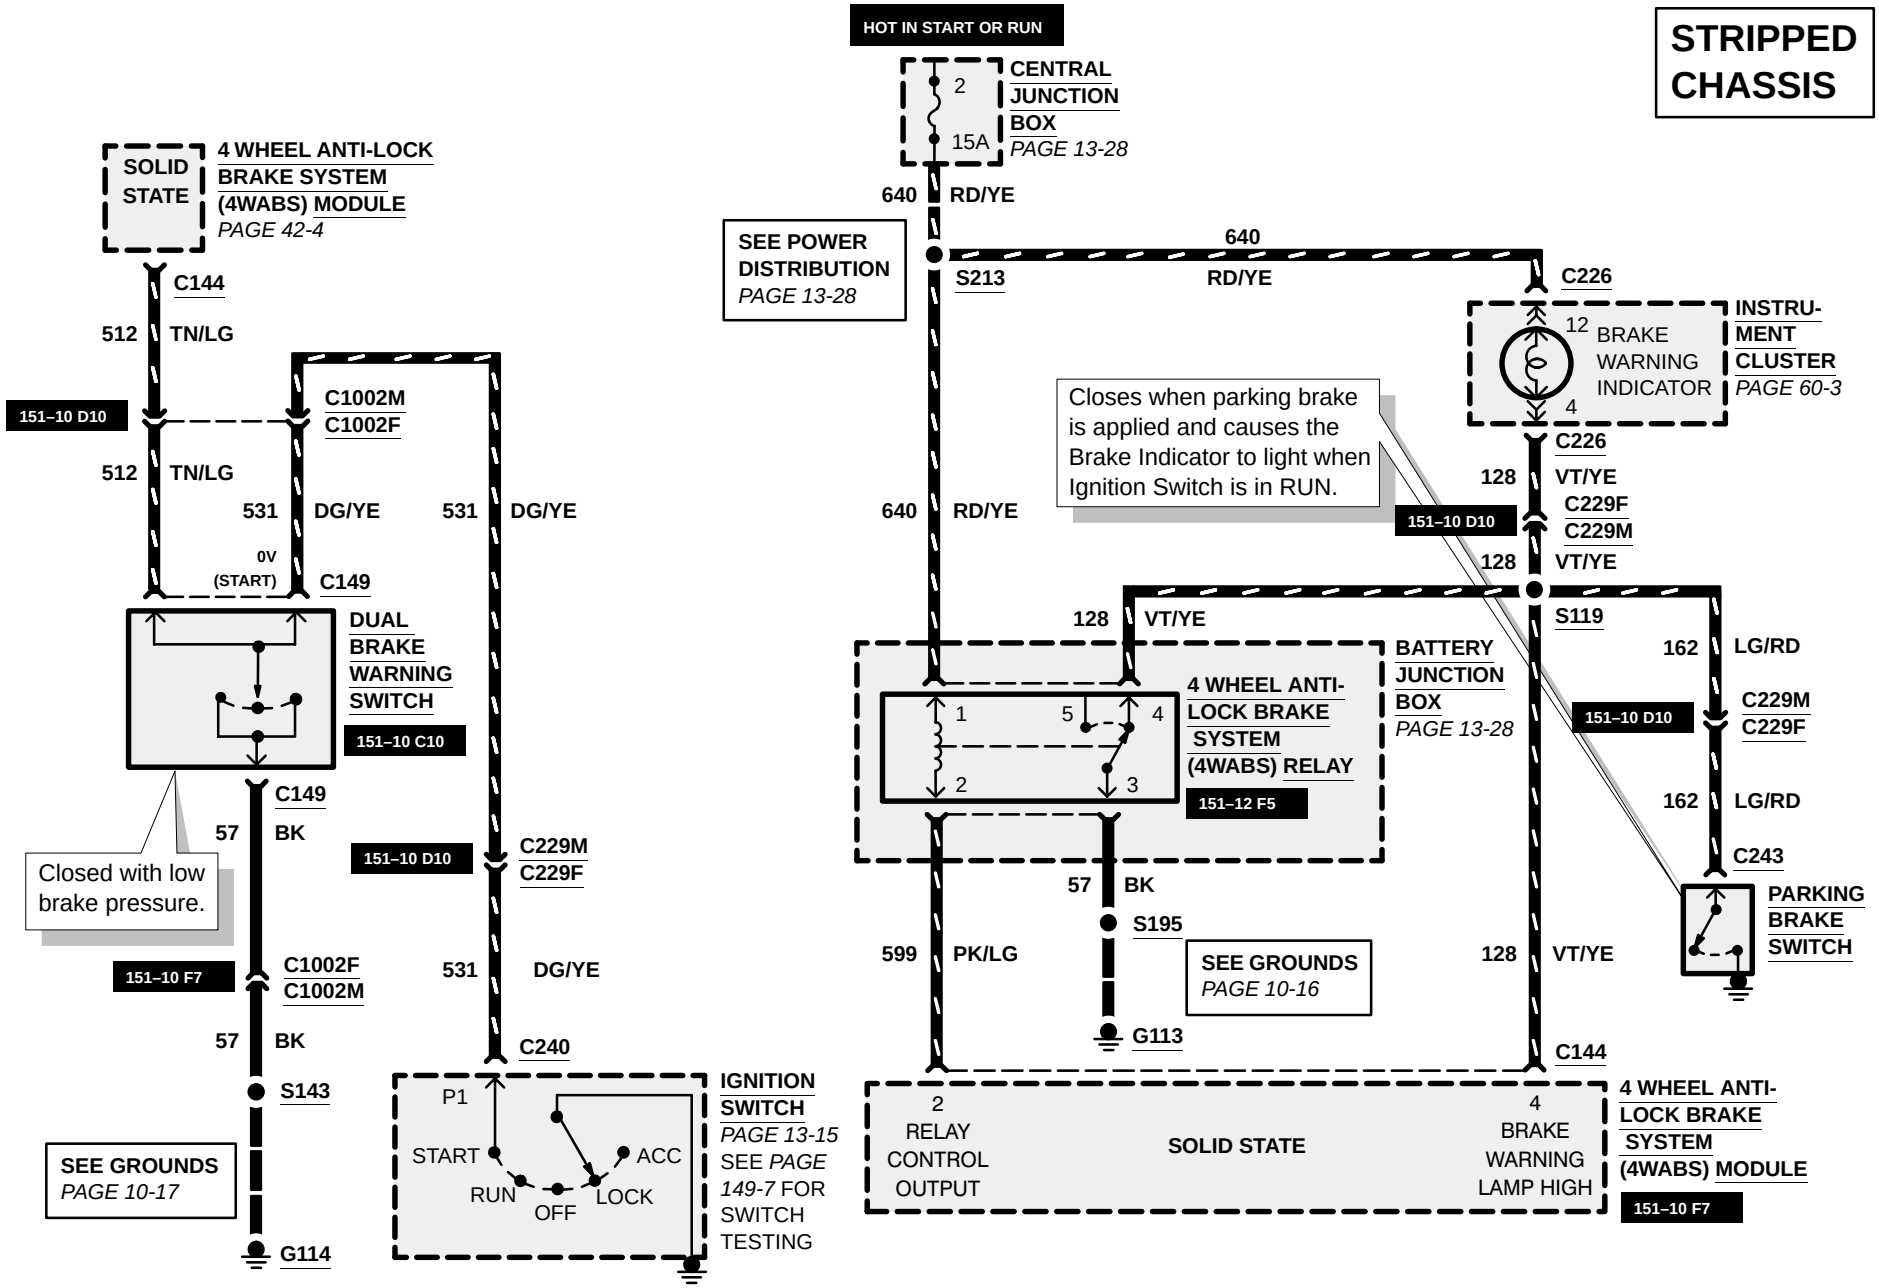65-3 WARNING INDICATORS