Master window control switch

Schematic

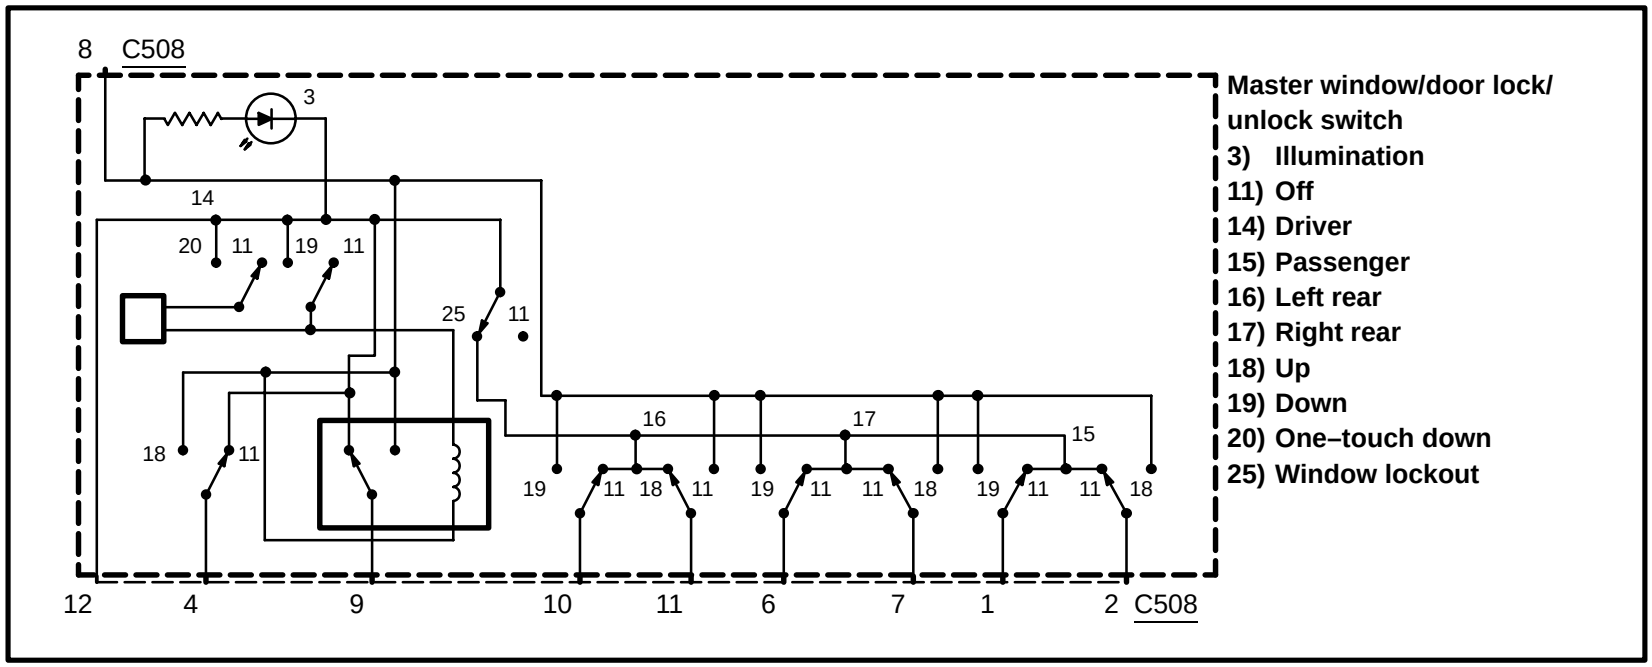
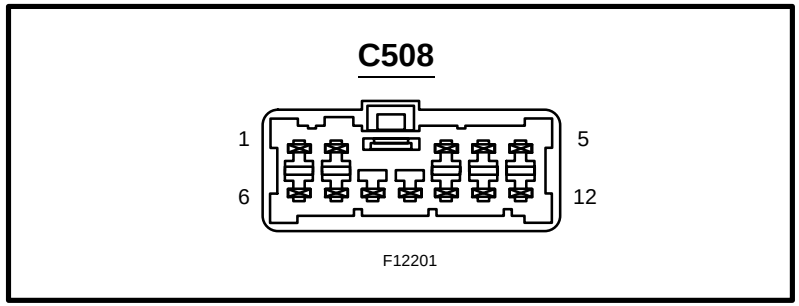
Terminals