10-1 GROUNDS

2001 CONTINENTAL
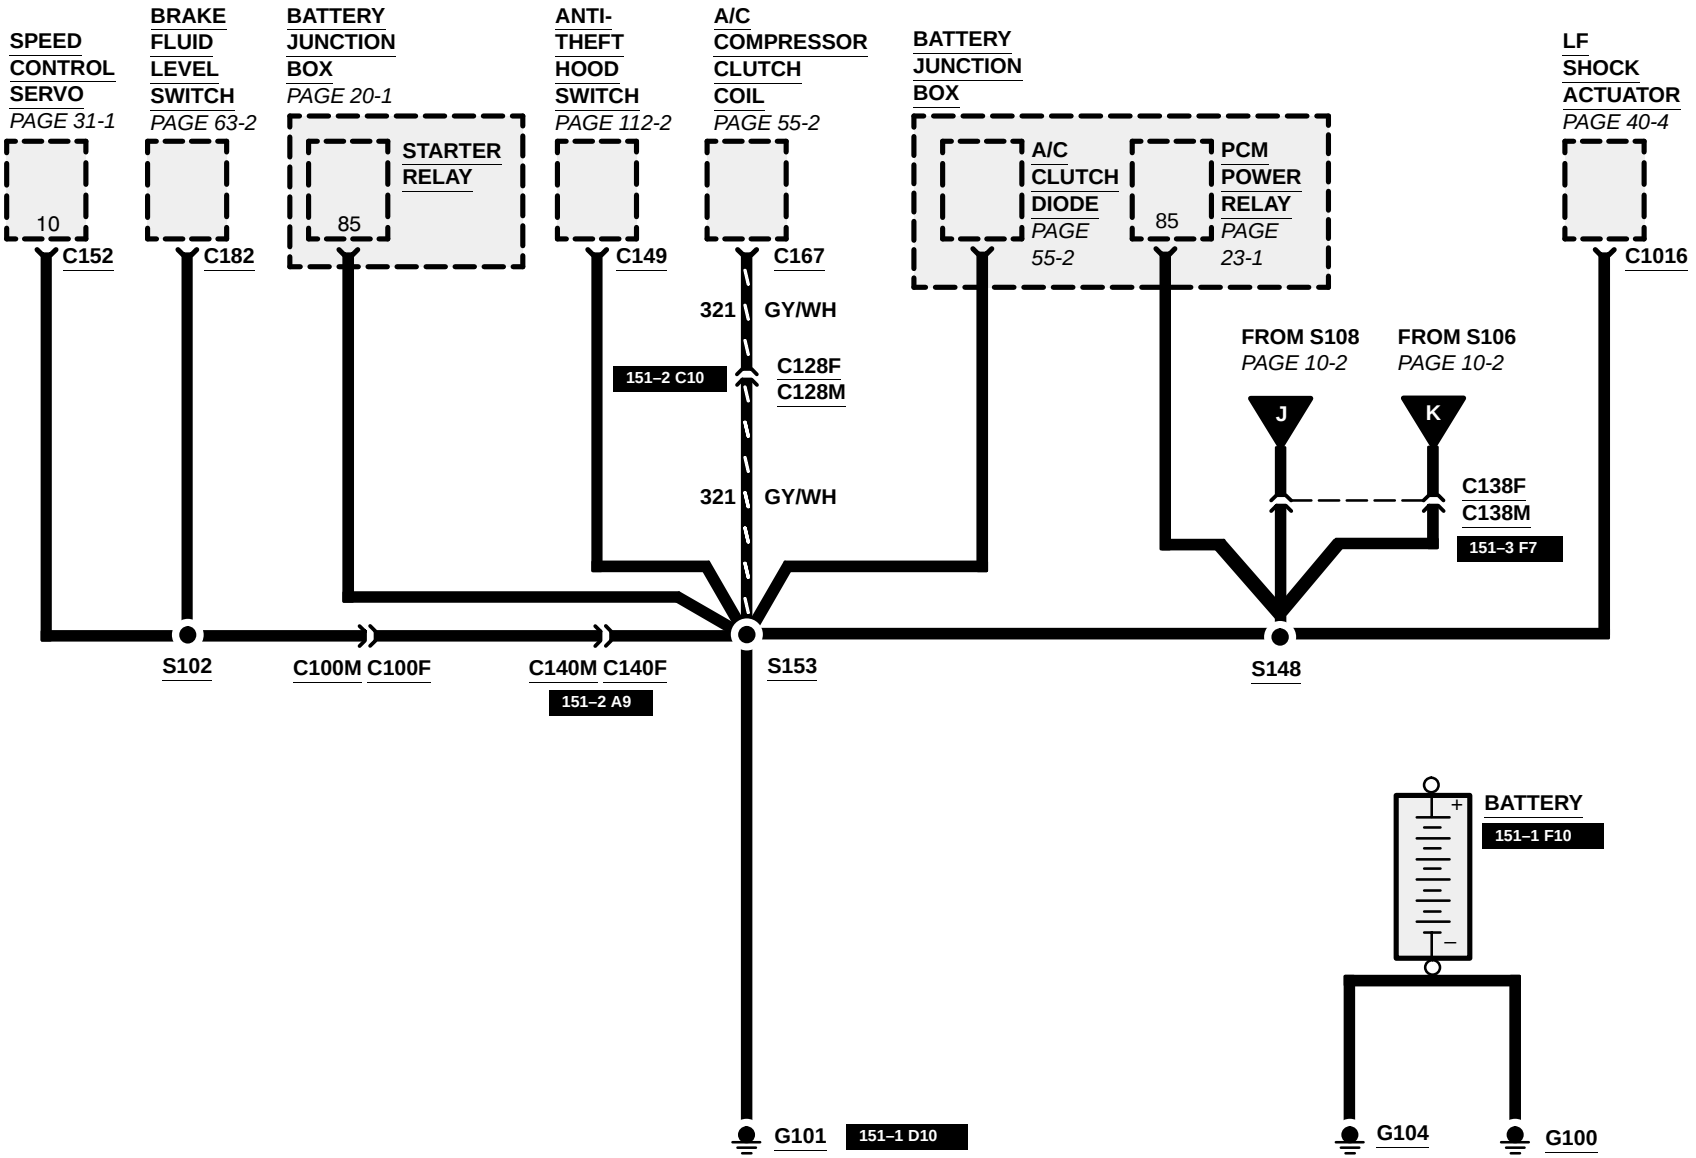
All wires are 57 BK unless otherwise noted.