101-1 ROOF OPENING PANEL
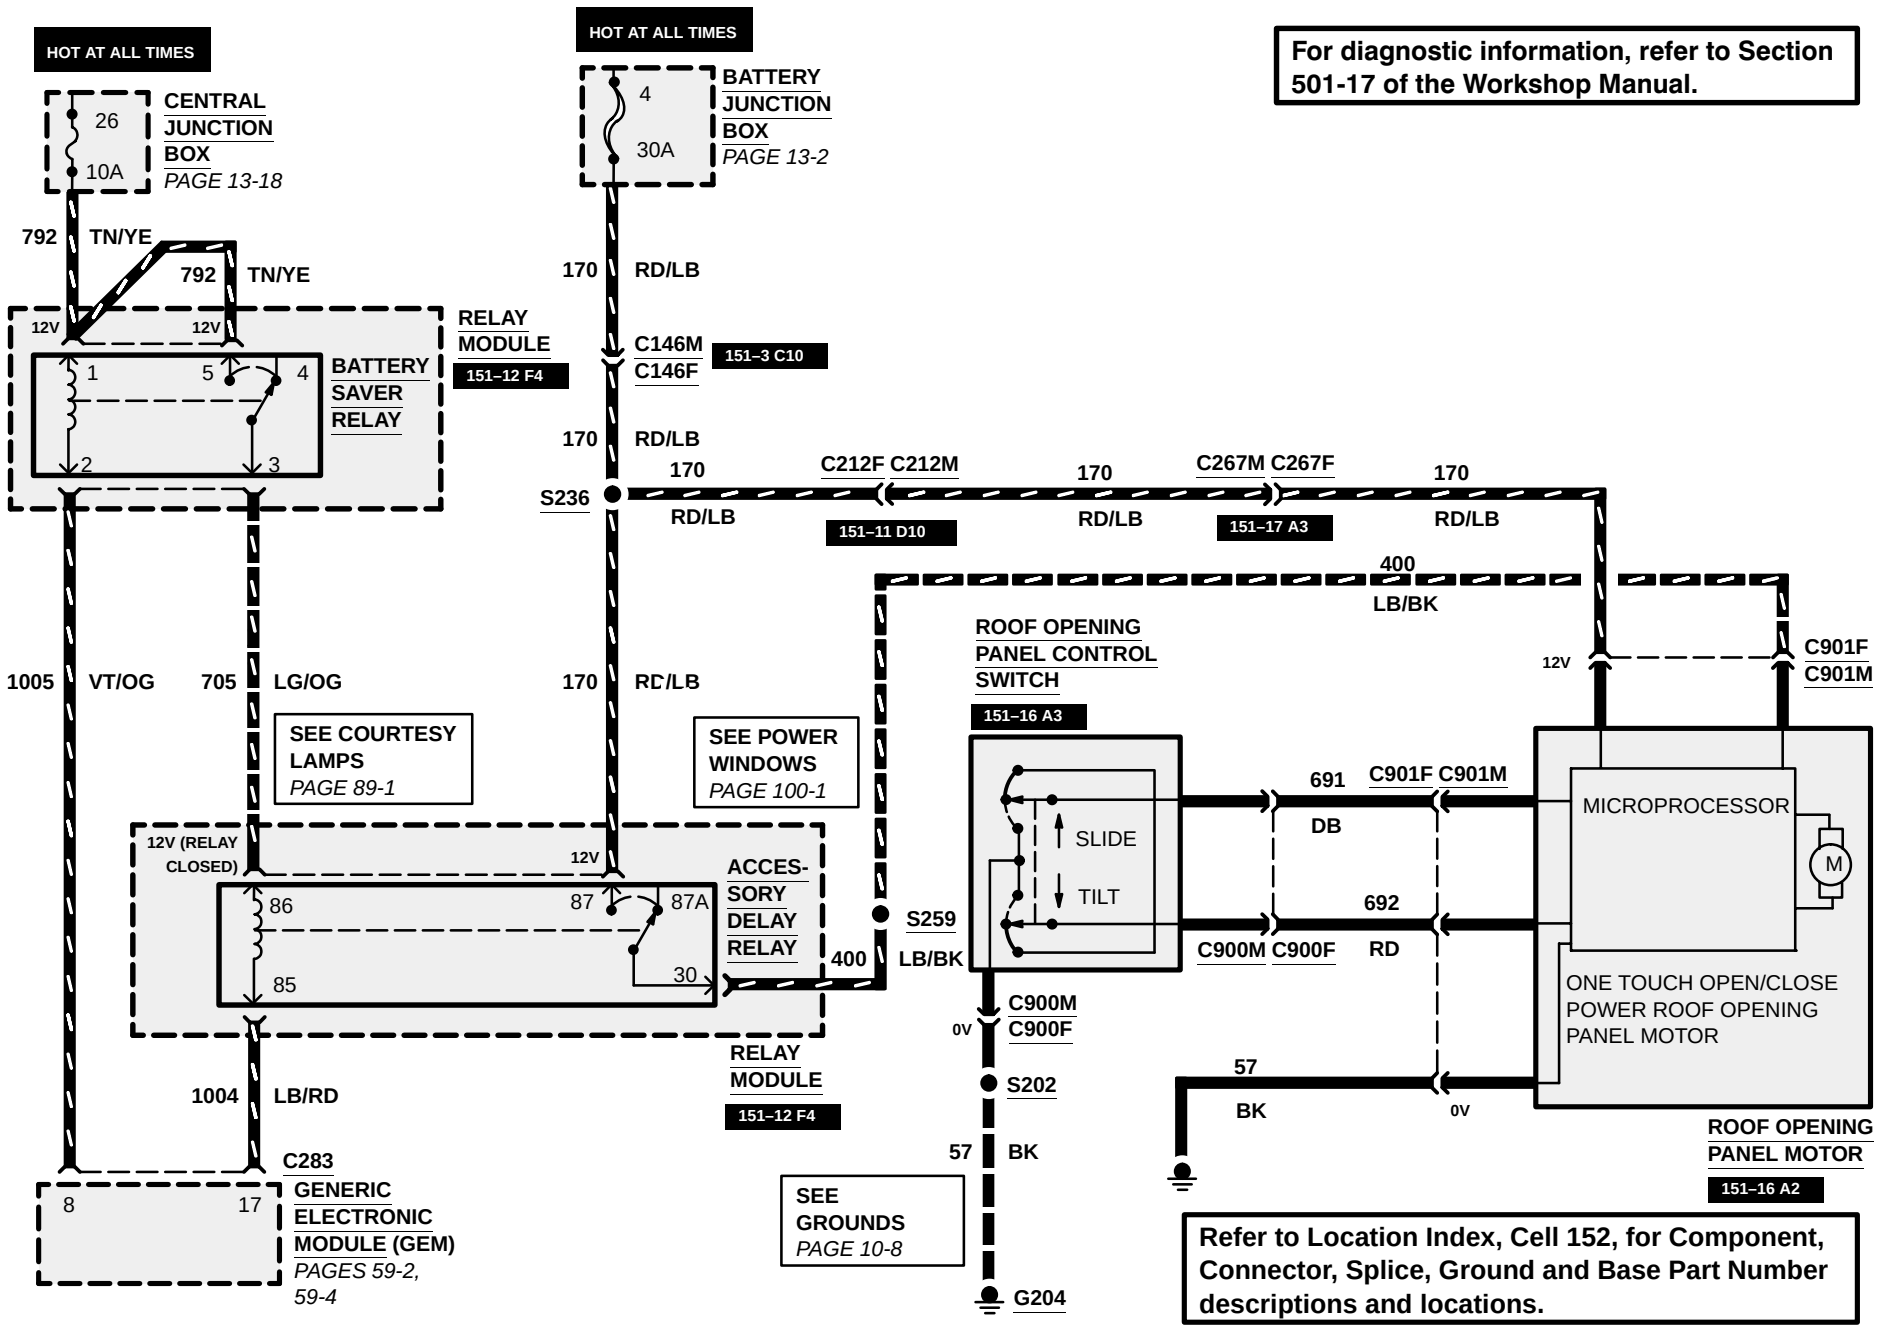
2001 EXPLORER/MOUNTAINEER