10-7 GROUNDS
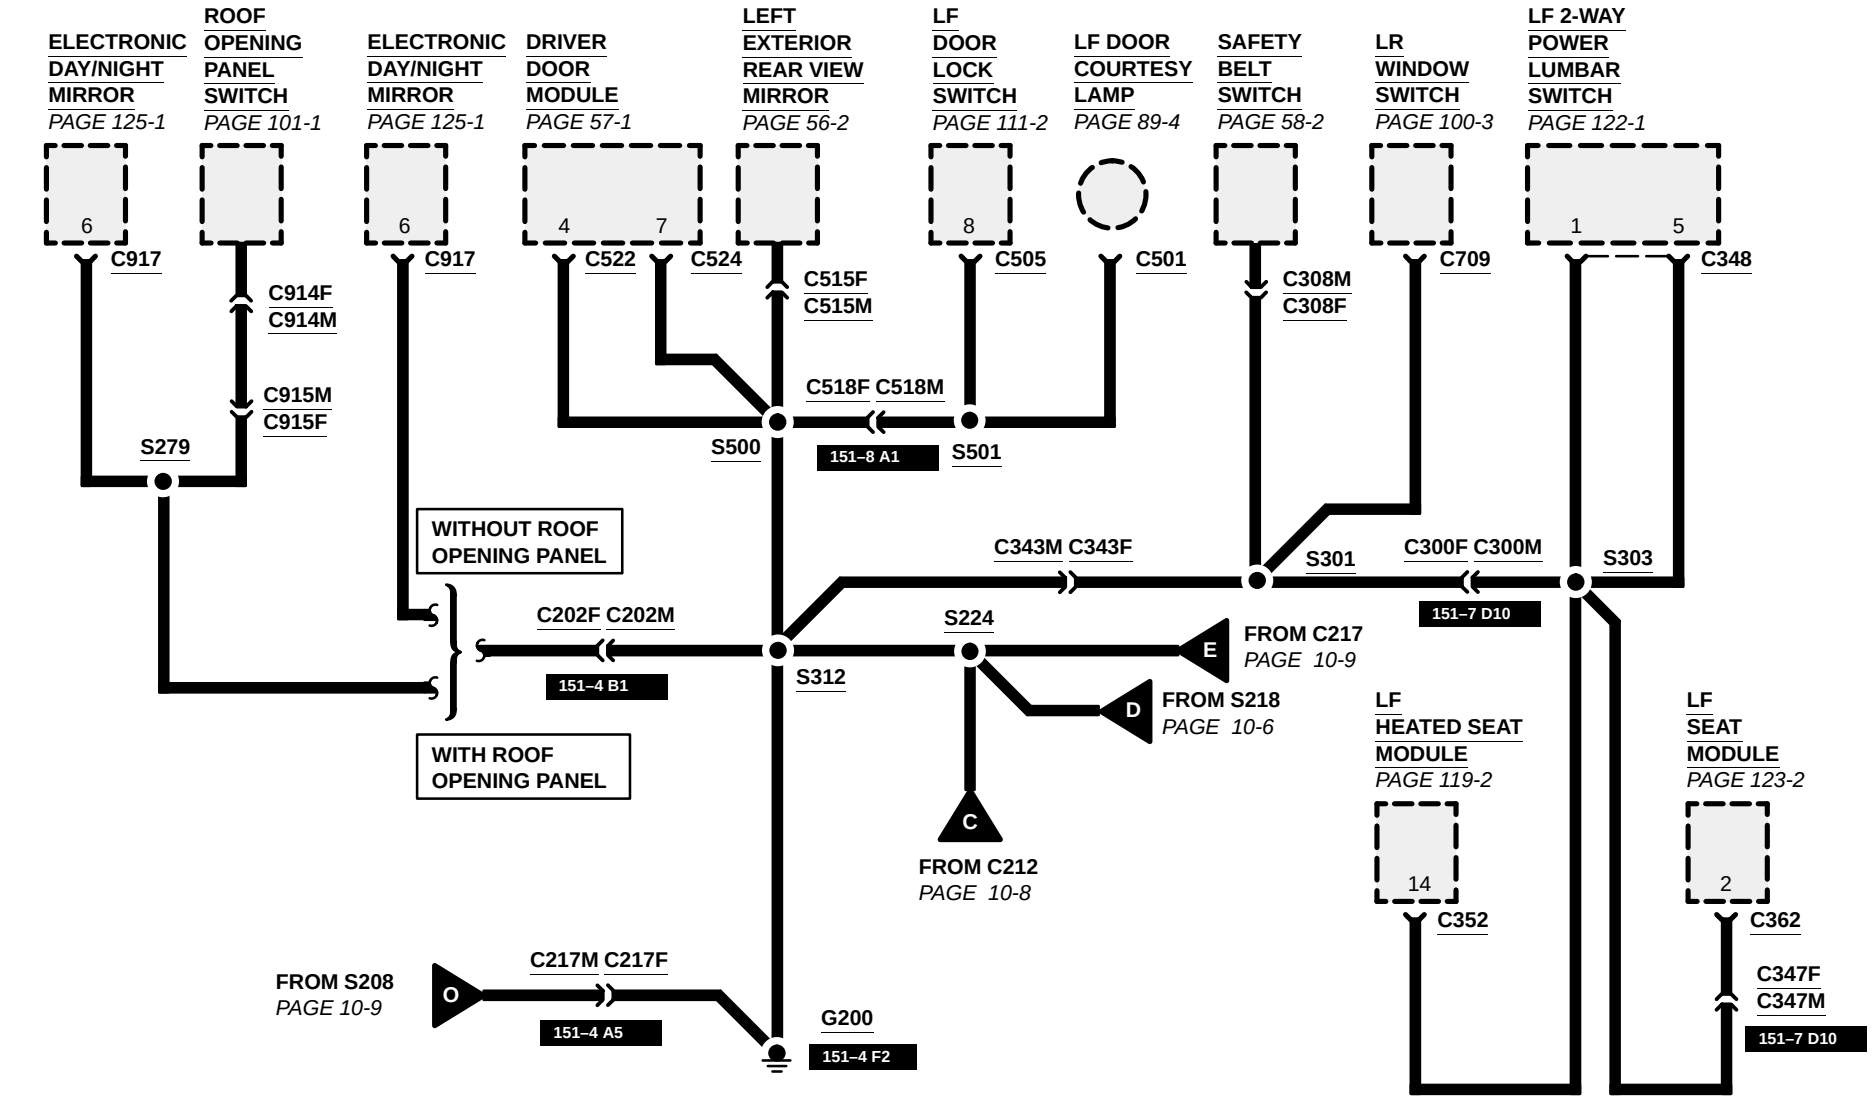
All wires are 57 BK unless otherwise noted.