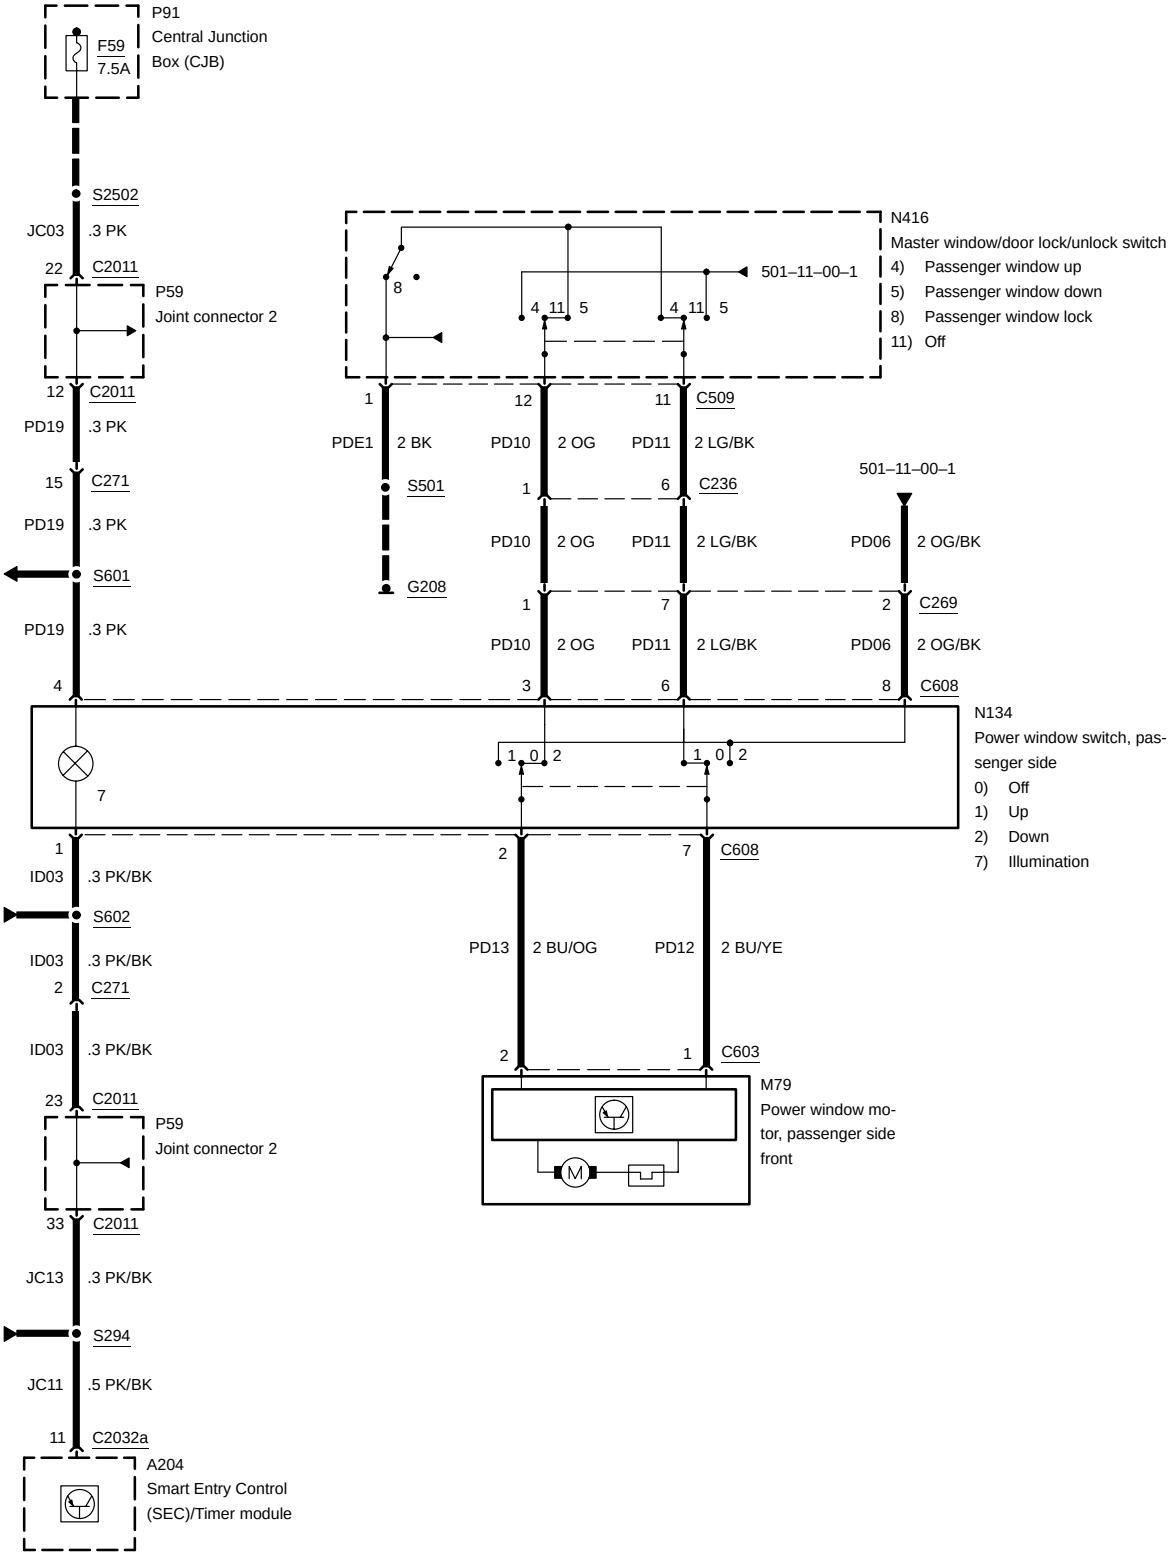front power windows -2