10-13 GROUNDS

2001 TOWN CAR

All Circuits are 57 BK unless otherwise noted.
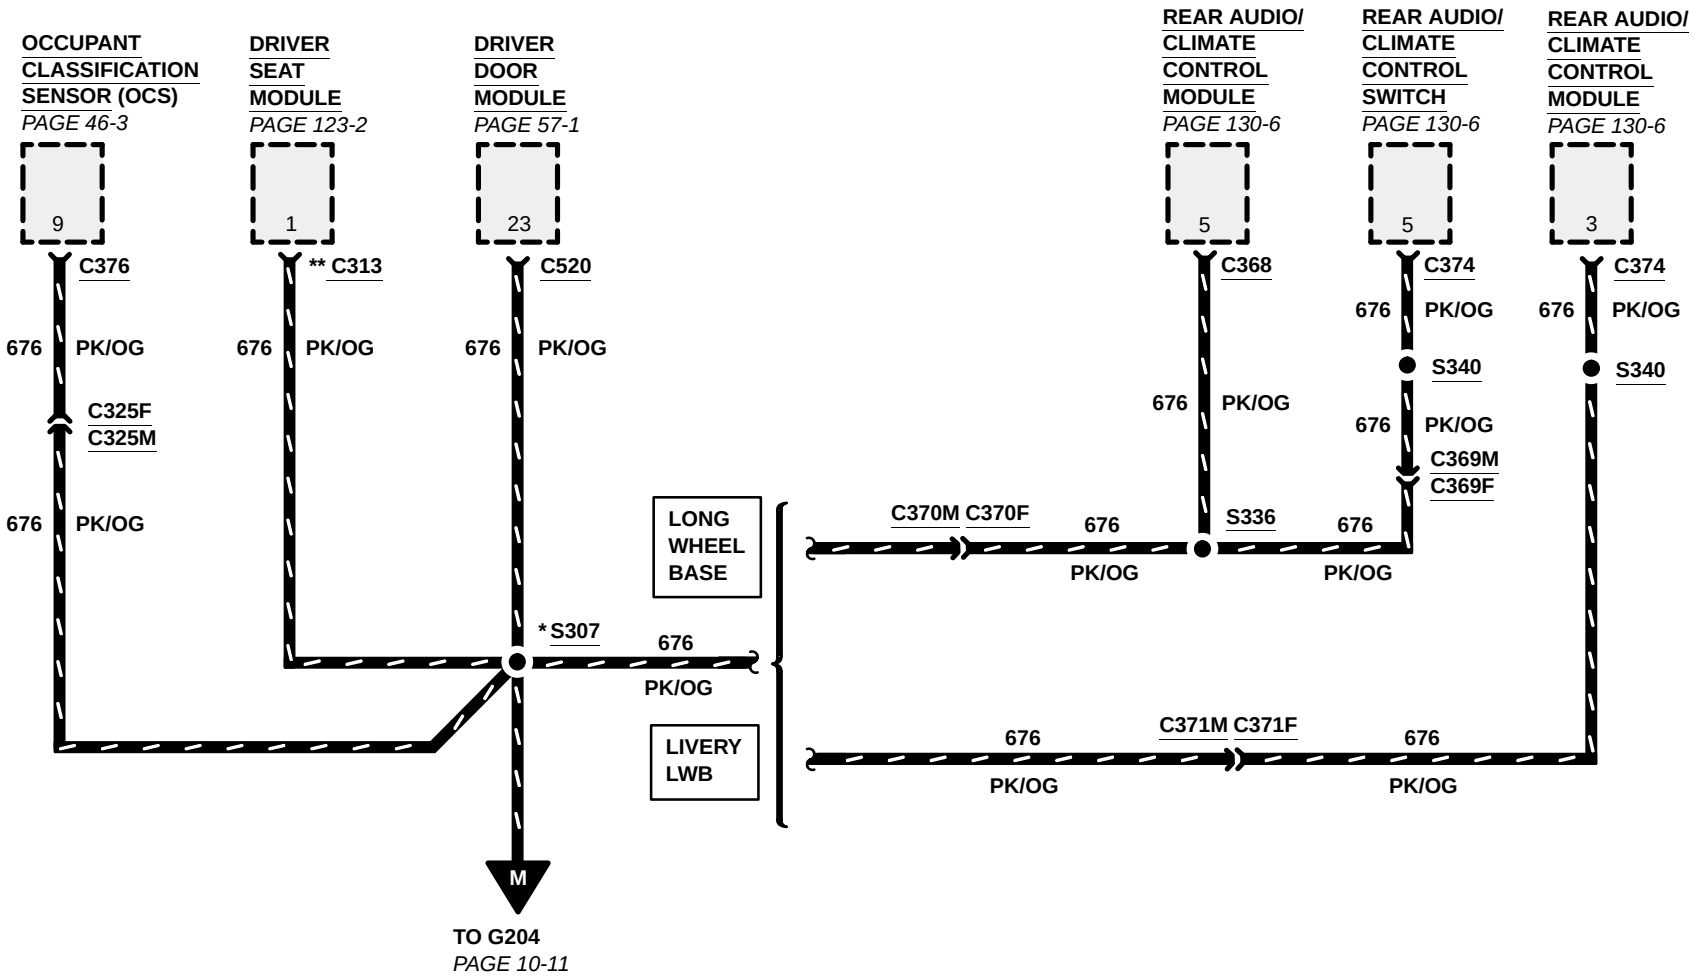
*** SIGNATURE/CARTIER**
**** EXCEPT LIVERY LWB**