COMPONENT LOCATION VIEWS 151-18

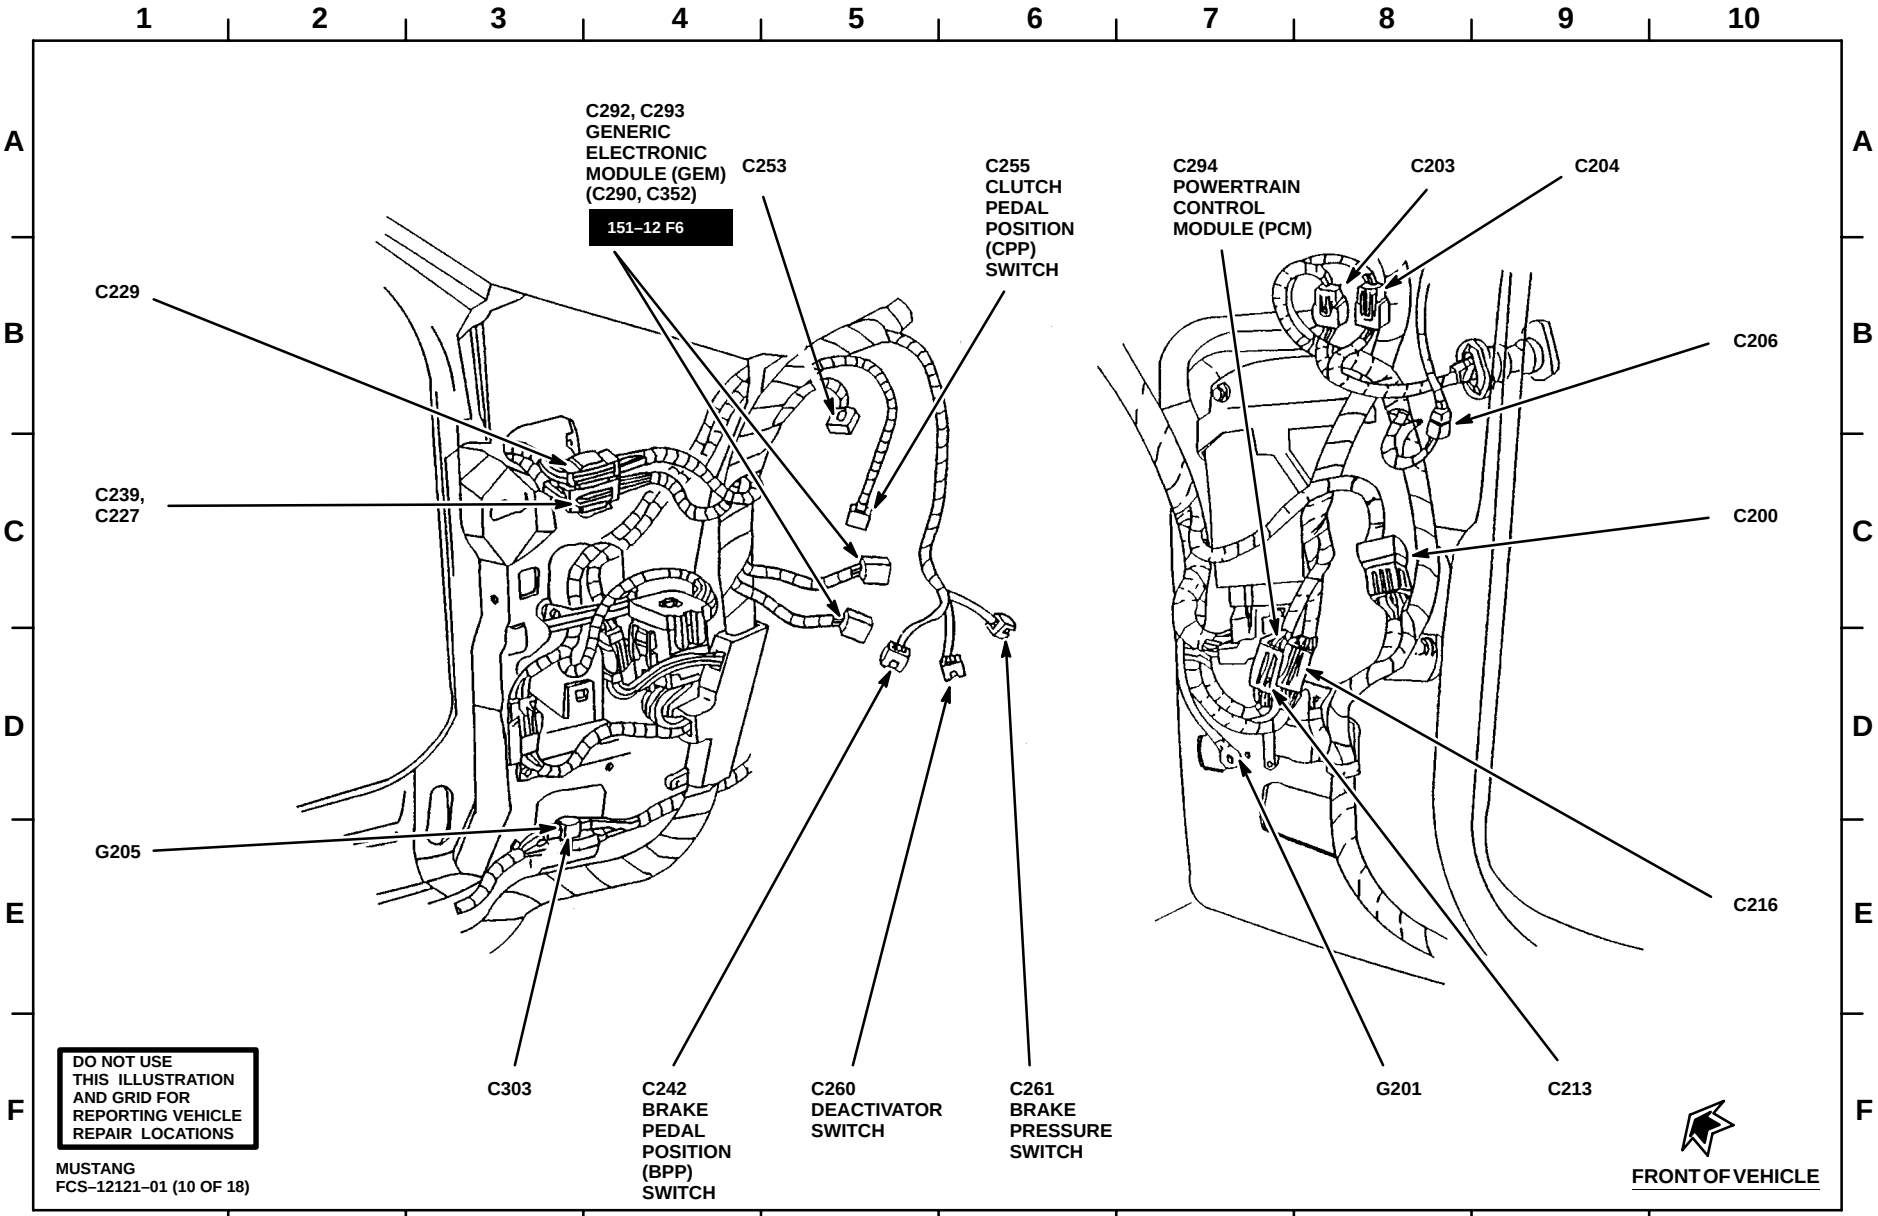

COWLS