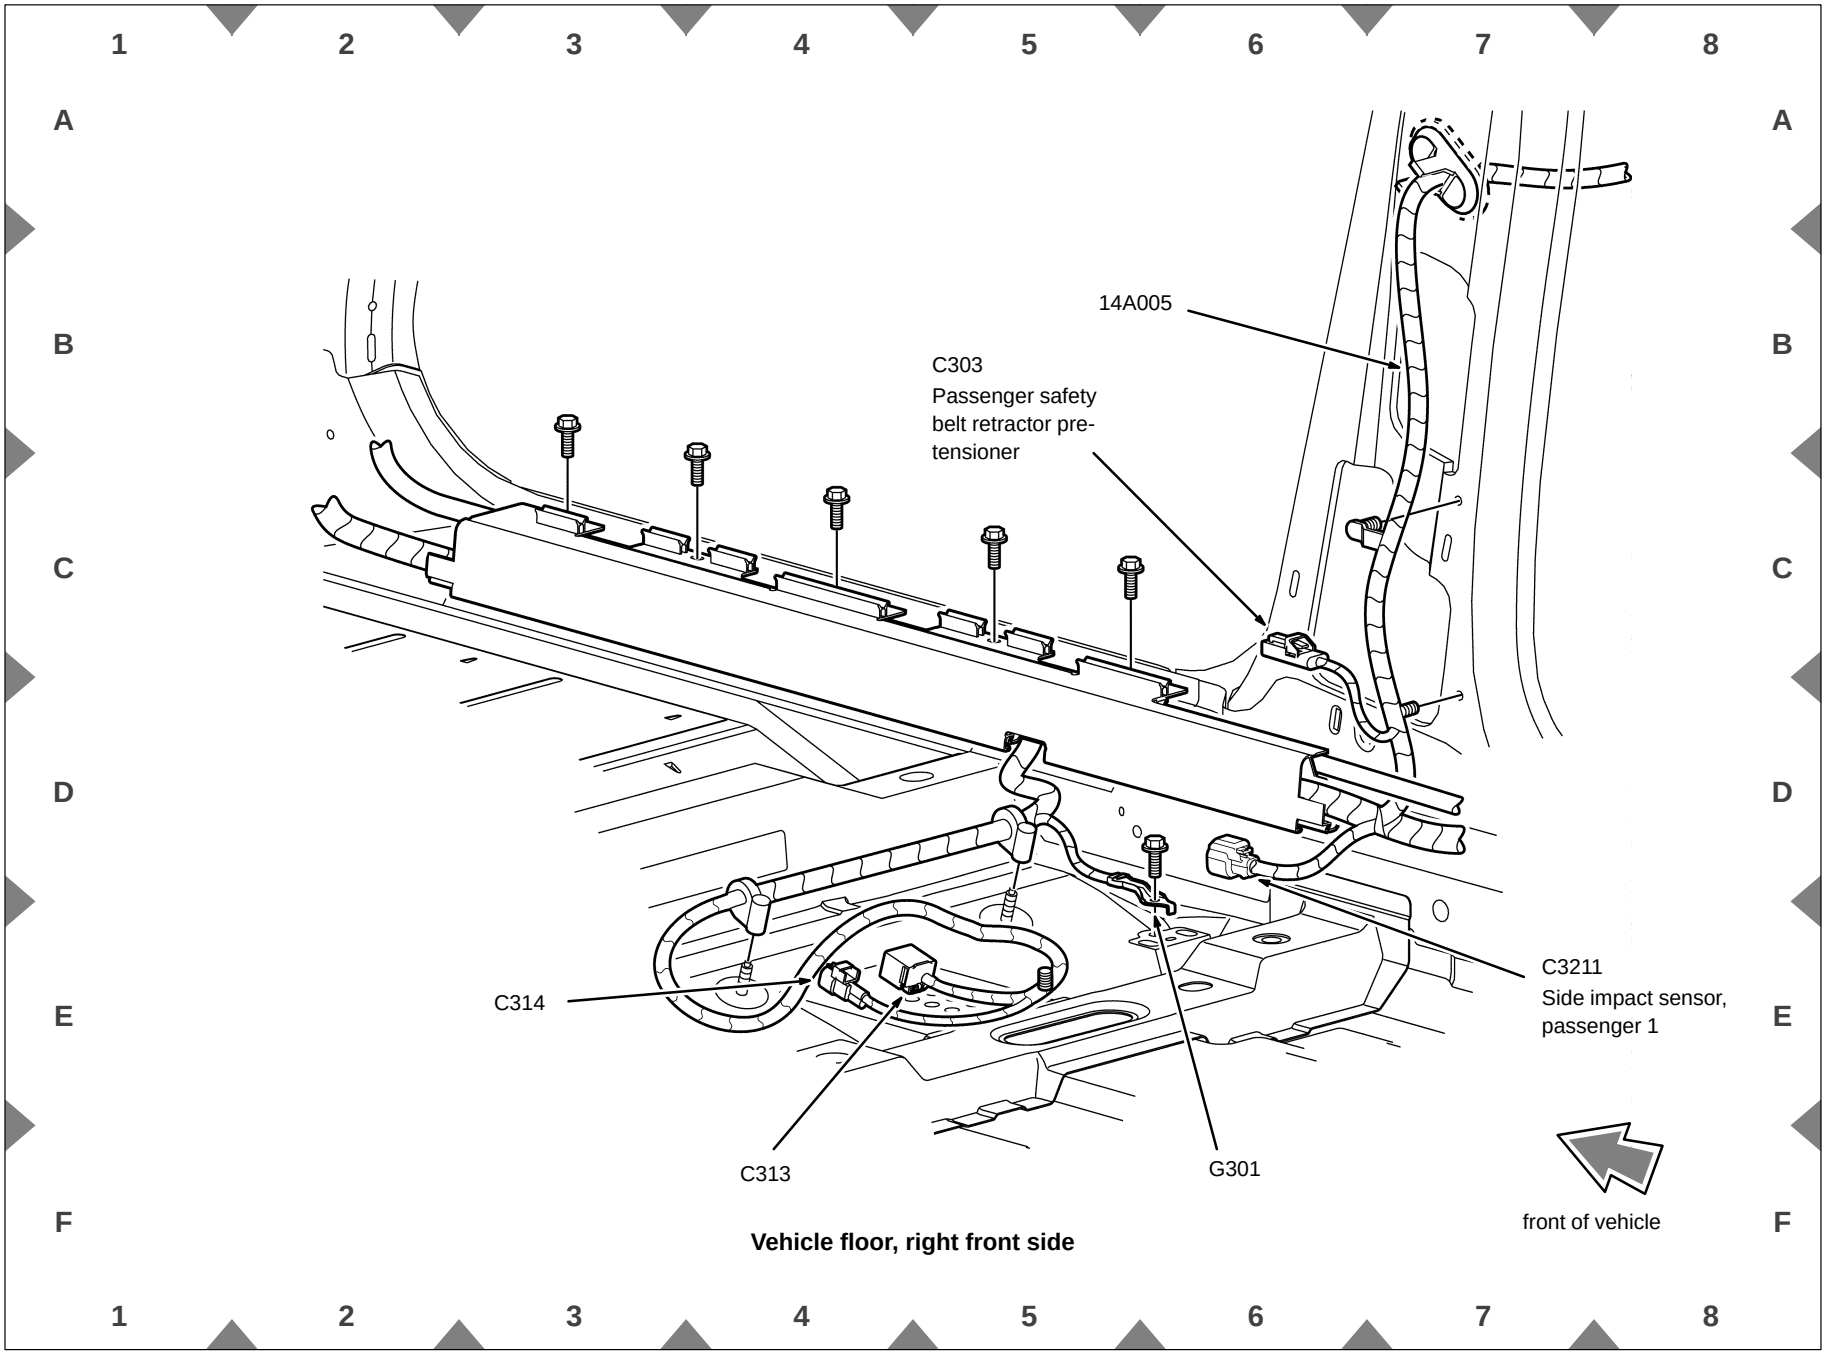


Vehicle floor, right front side