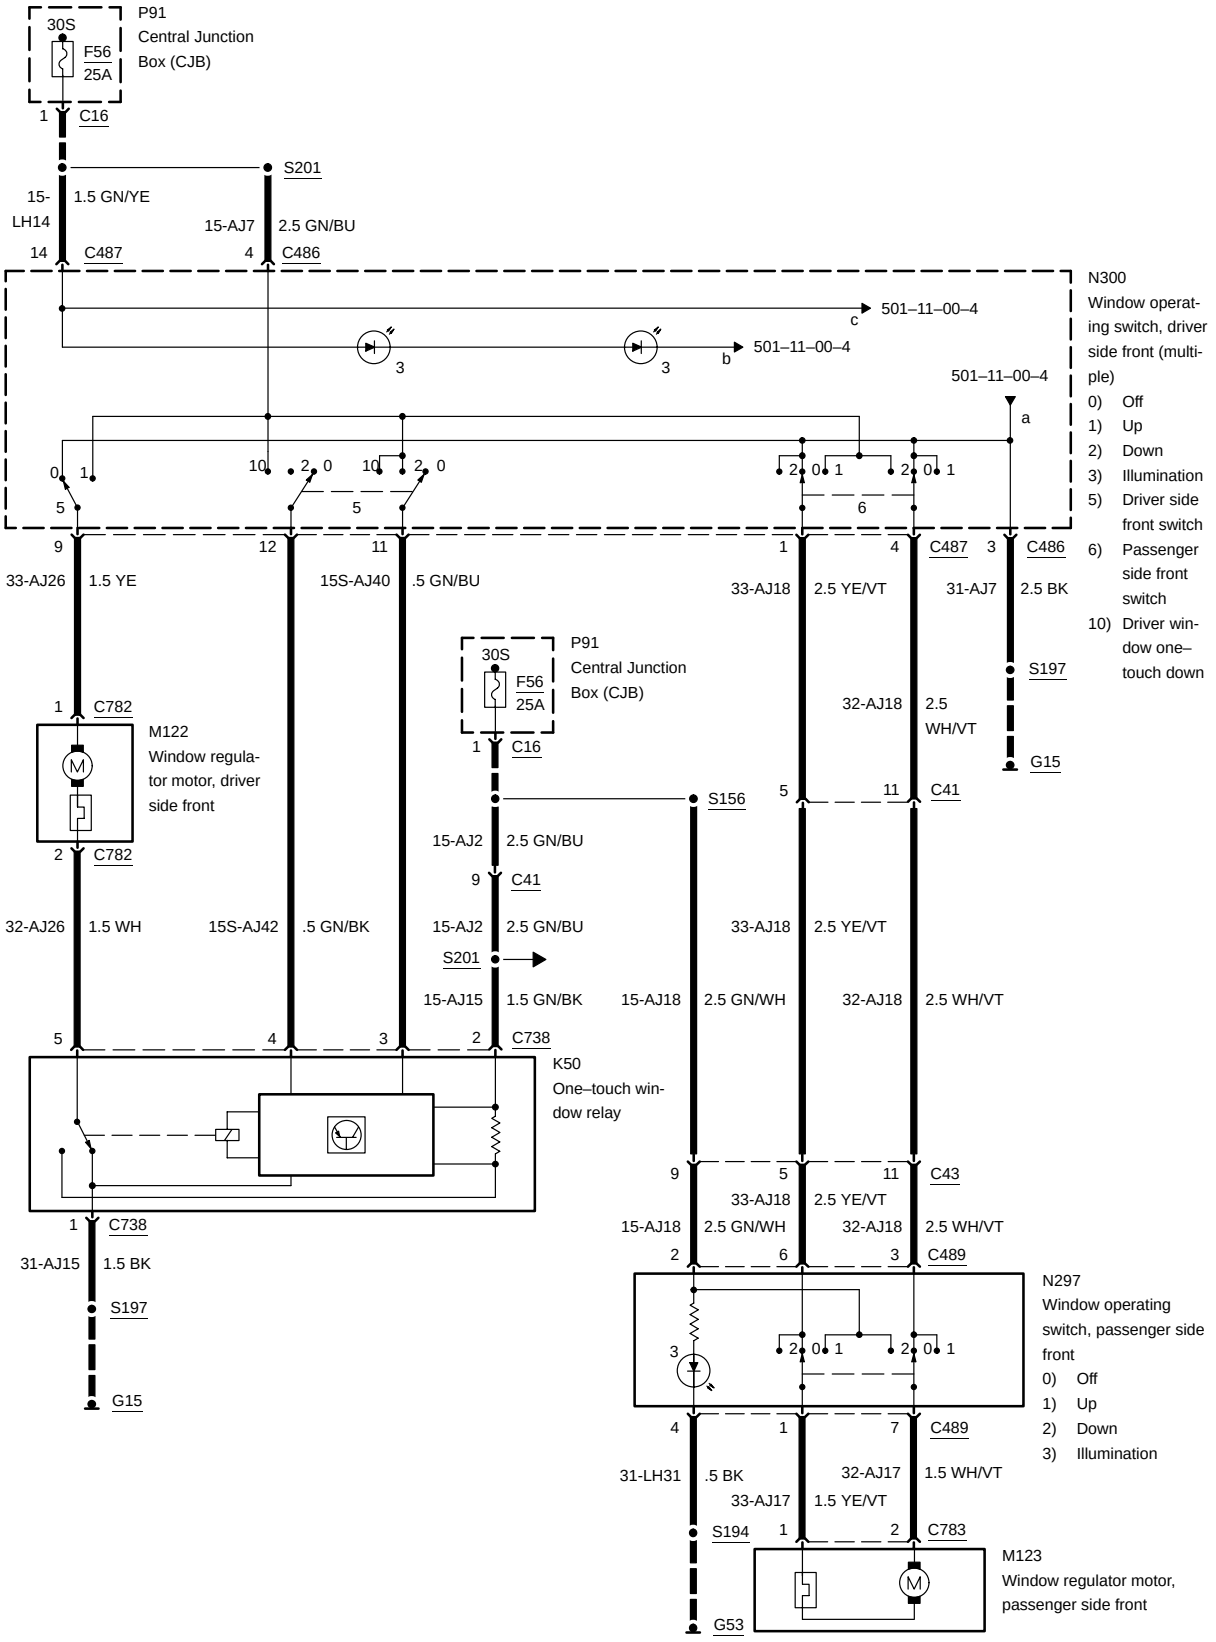with front and rear power windows -2