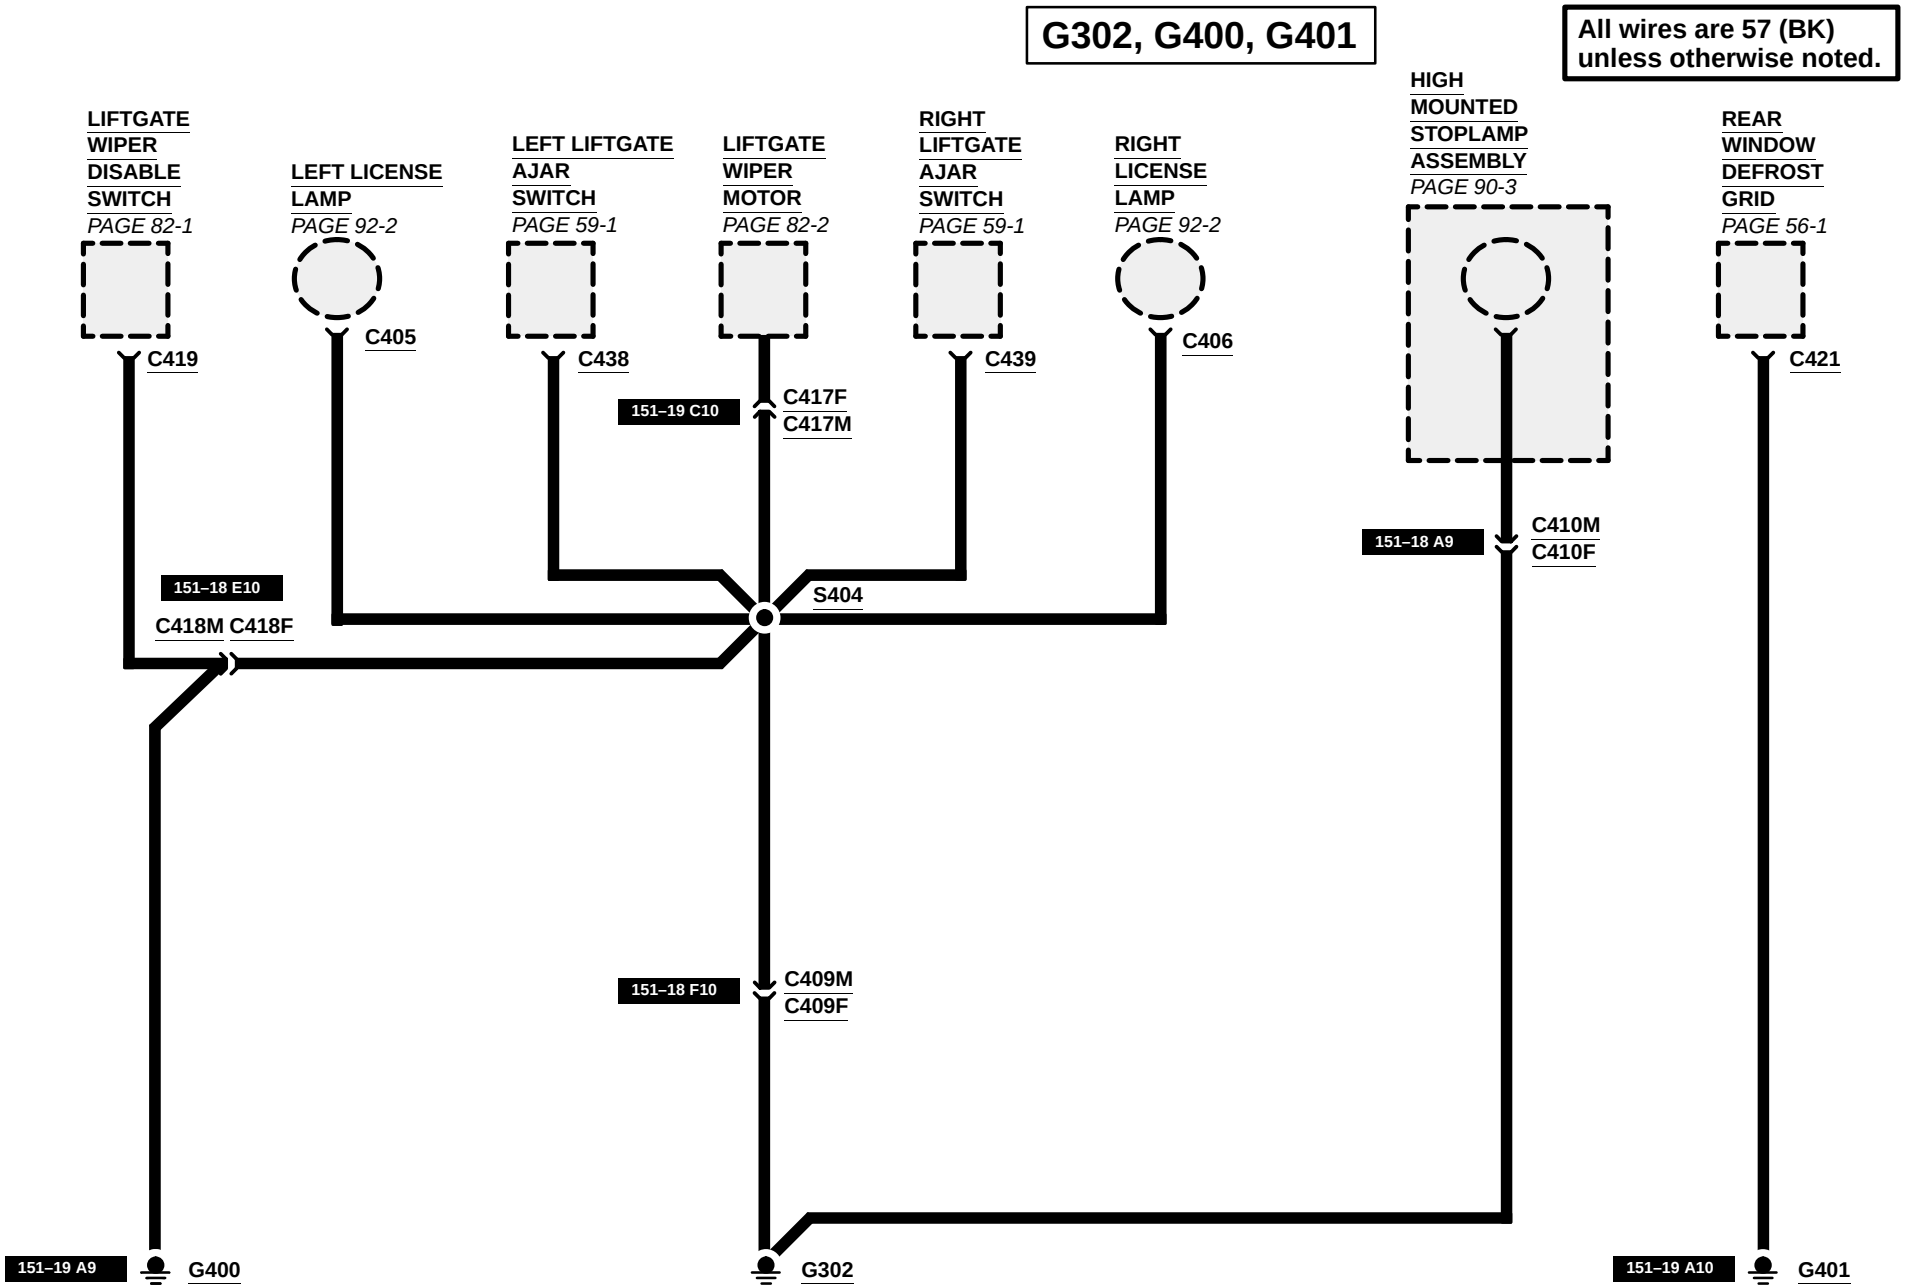
G302, G400, G401
All wires are 57 (BK) unless otherwise noted.
LIFTGATE WIPER DISABLE SWITCH
PAGE 82-1
C419
LEFT LICENSE LAMP
PAGE 92-2
C405
LEFT LIFTGATE AJAR SWITCH
PAGE 59-1
C438
LIFTGATE WIPER MOTOR
PAGE 82-2
C417F
C417M
151–19 C10
RIGHT LIFTGATE AJAR SWITCH
PAGE 59-1
C439
RIGHT LICENSE LAMP
PAGE 92-2
C406
HIGH MOUNTED STOPLAMP ASSEMBLY
PAGE 90-3
C410M
C410F
151–18 A9
REAR WINDOW DEFROST GRID
PAGE 56-1
C421
151–18 E10
C418M C418F
S404
151–18 F10
C409M
C409F
151–19 A9
G400
G302
151–19 A10
G401