10-3 GROUNDS

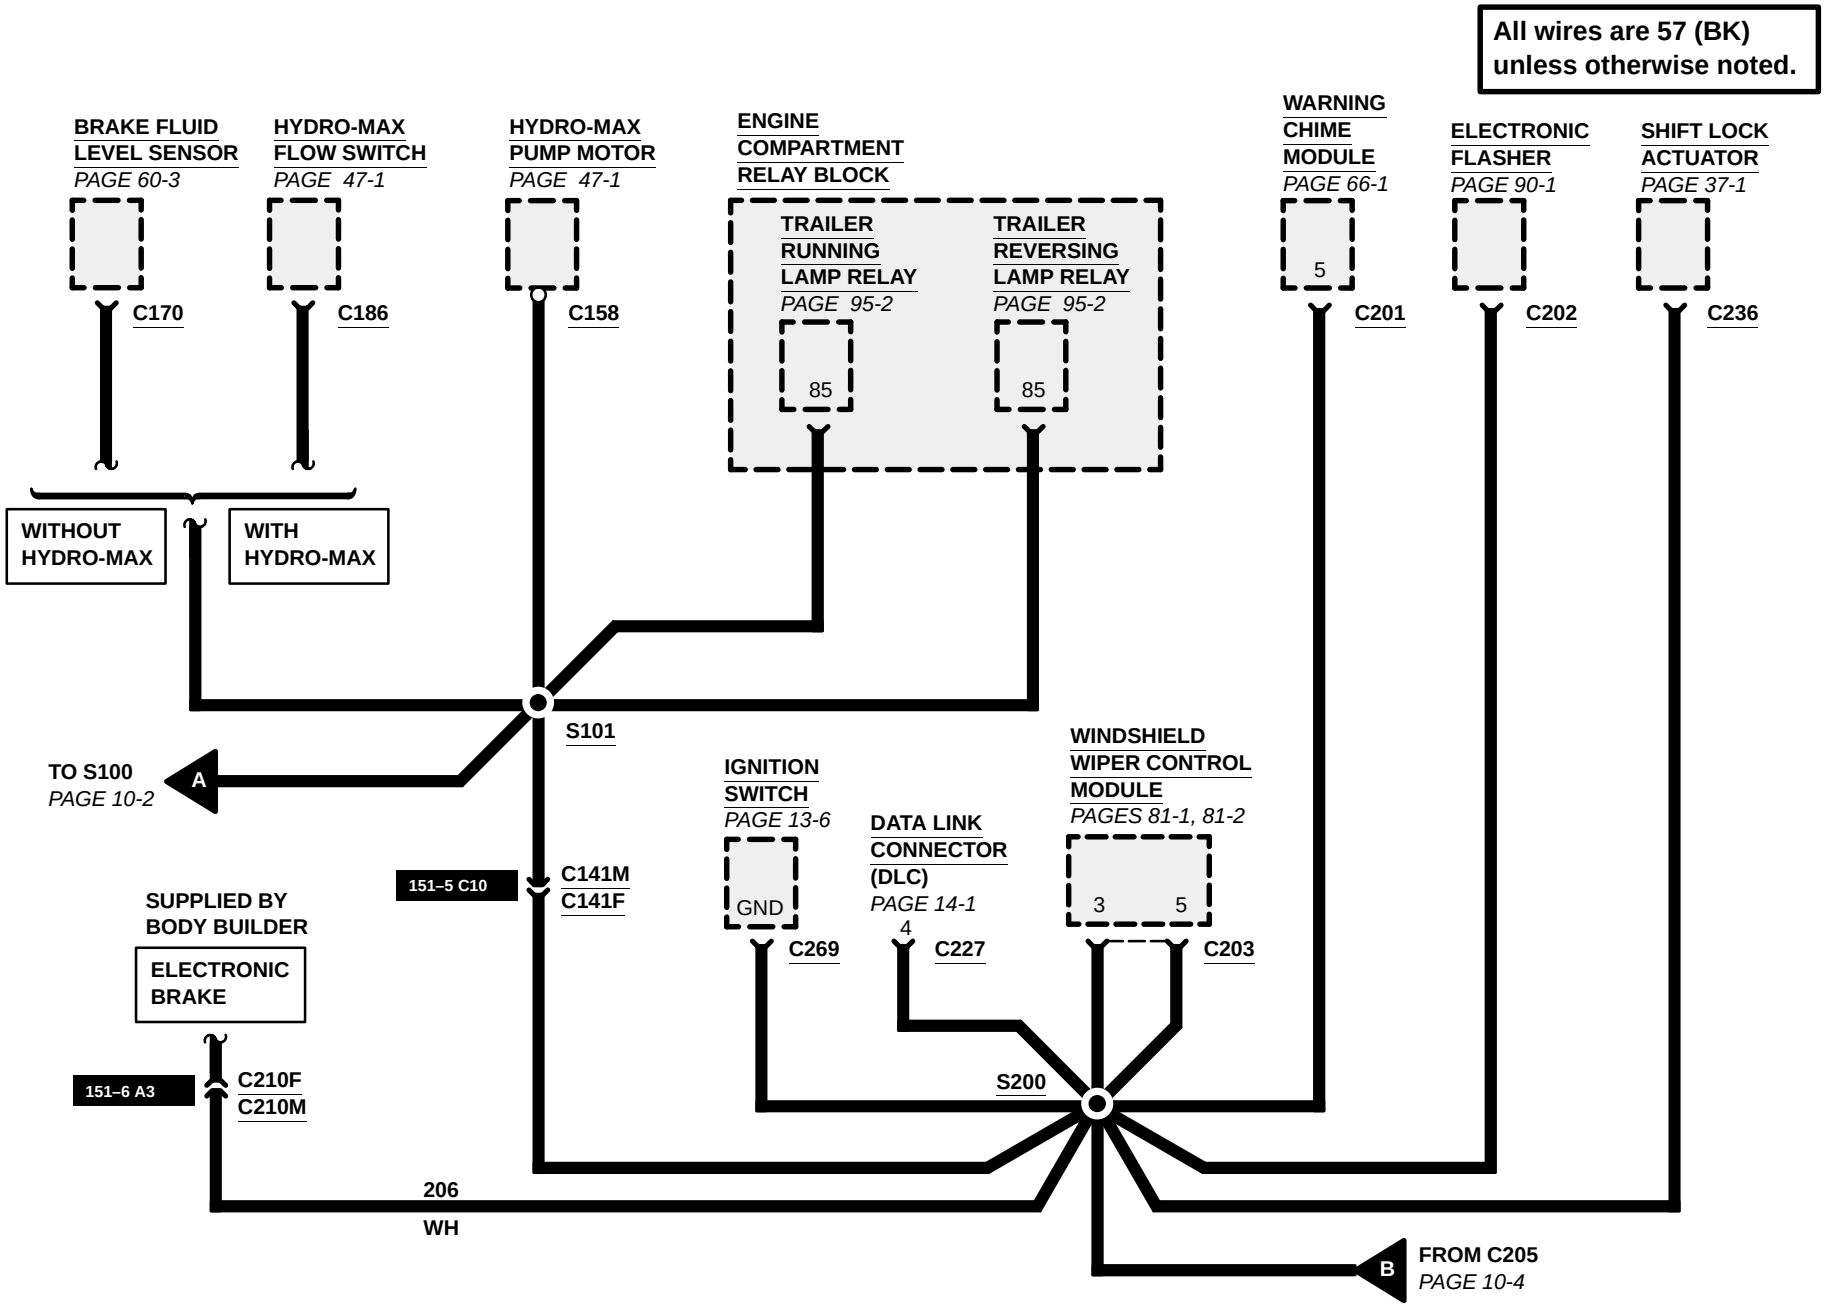
All wires are 57 (BK) unless otherwise noted.
BRAKE FLUID LEVEL SENSOR
PAGE 60-3
HYDRO-MAX FLOW SWITCH
PAGE 47-1
HYDRO-MAX PUMP MOTOR
PAGE 47-1
ENGINE COMPARTMENT RELAY BLOCK
TRAILER RUNNING LAMP RELAY
PAGE 95-2
TRAILER REVERSING LAMP RELAY
PAGE 95-2
WARNING CHIME MODULE
PAGE 66-1
ELECTRONIC FLASHER
PAGE 90-1
SHIFT LOCK ACTUATOR
PAGE 37-1
C170
C186
C158
85
85
5
C201
C202
C236
WITHOUT HYDRO-MAX
WITH HYDRO-MAX
S101
TO S100
PAGE 10-2
A
IGNITION SWITCH
PAGE 13-6
DATA LINK CONNECTOR (DLC)
PAGE 14-1
WINDSHIELD WIPER CONTROL MODULE
PAGES 81-1, 81-2
151–5 C10
C141M
C141F
GND
C269
4
C227
3
5
C203
SUPPLIED BY BODY BUILDER
ELECTRONIC BRAKE
151–6 A3
C210F
C210M
S200
206
WH
B
FROM C205
PAGE 10-4