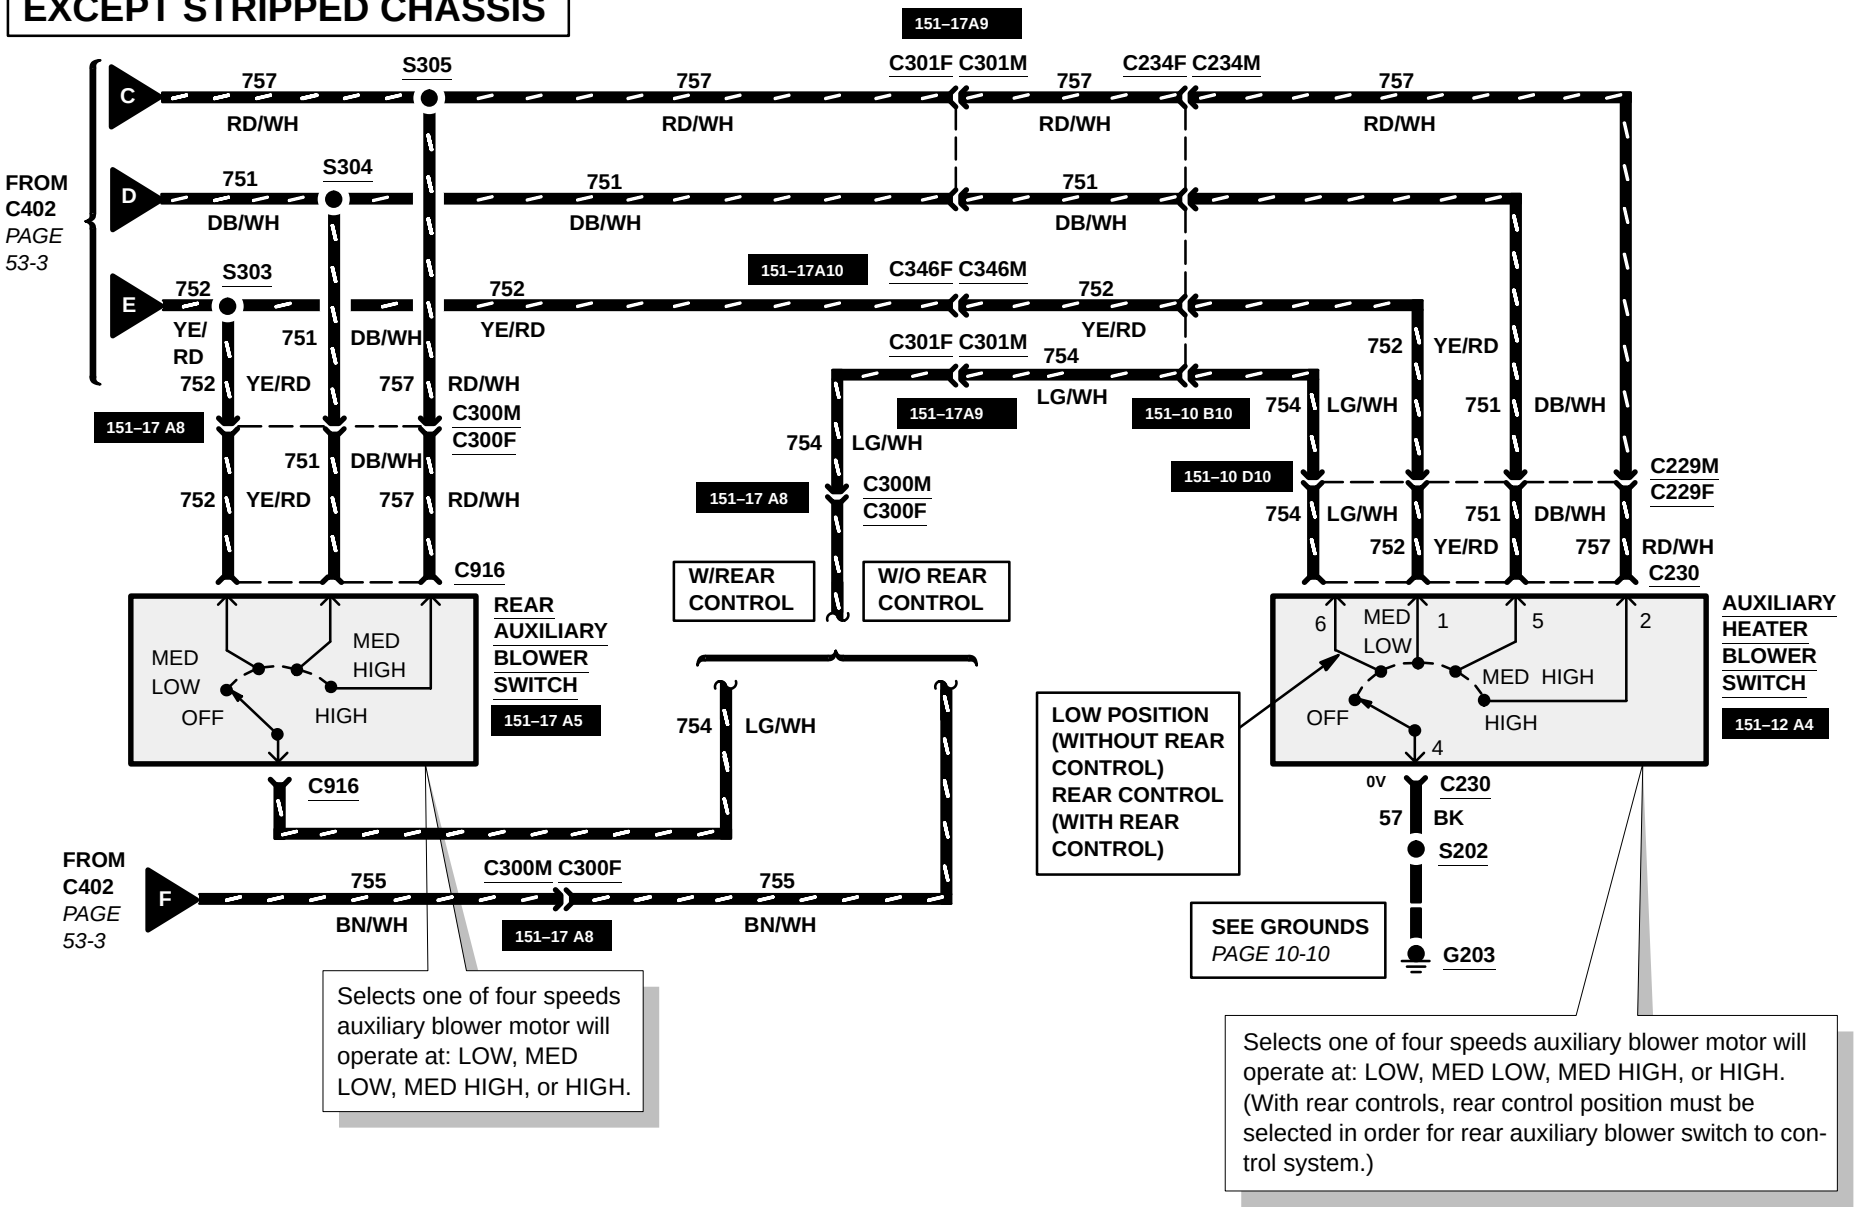EXCEPT STRIPPED CHASSIS