10-15 GROUNDS
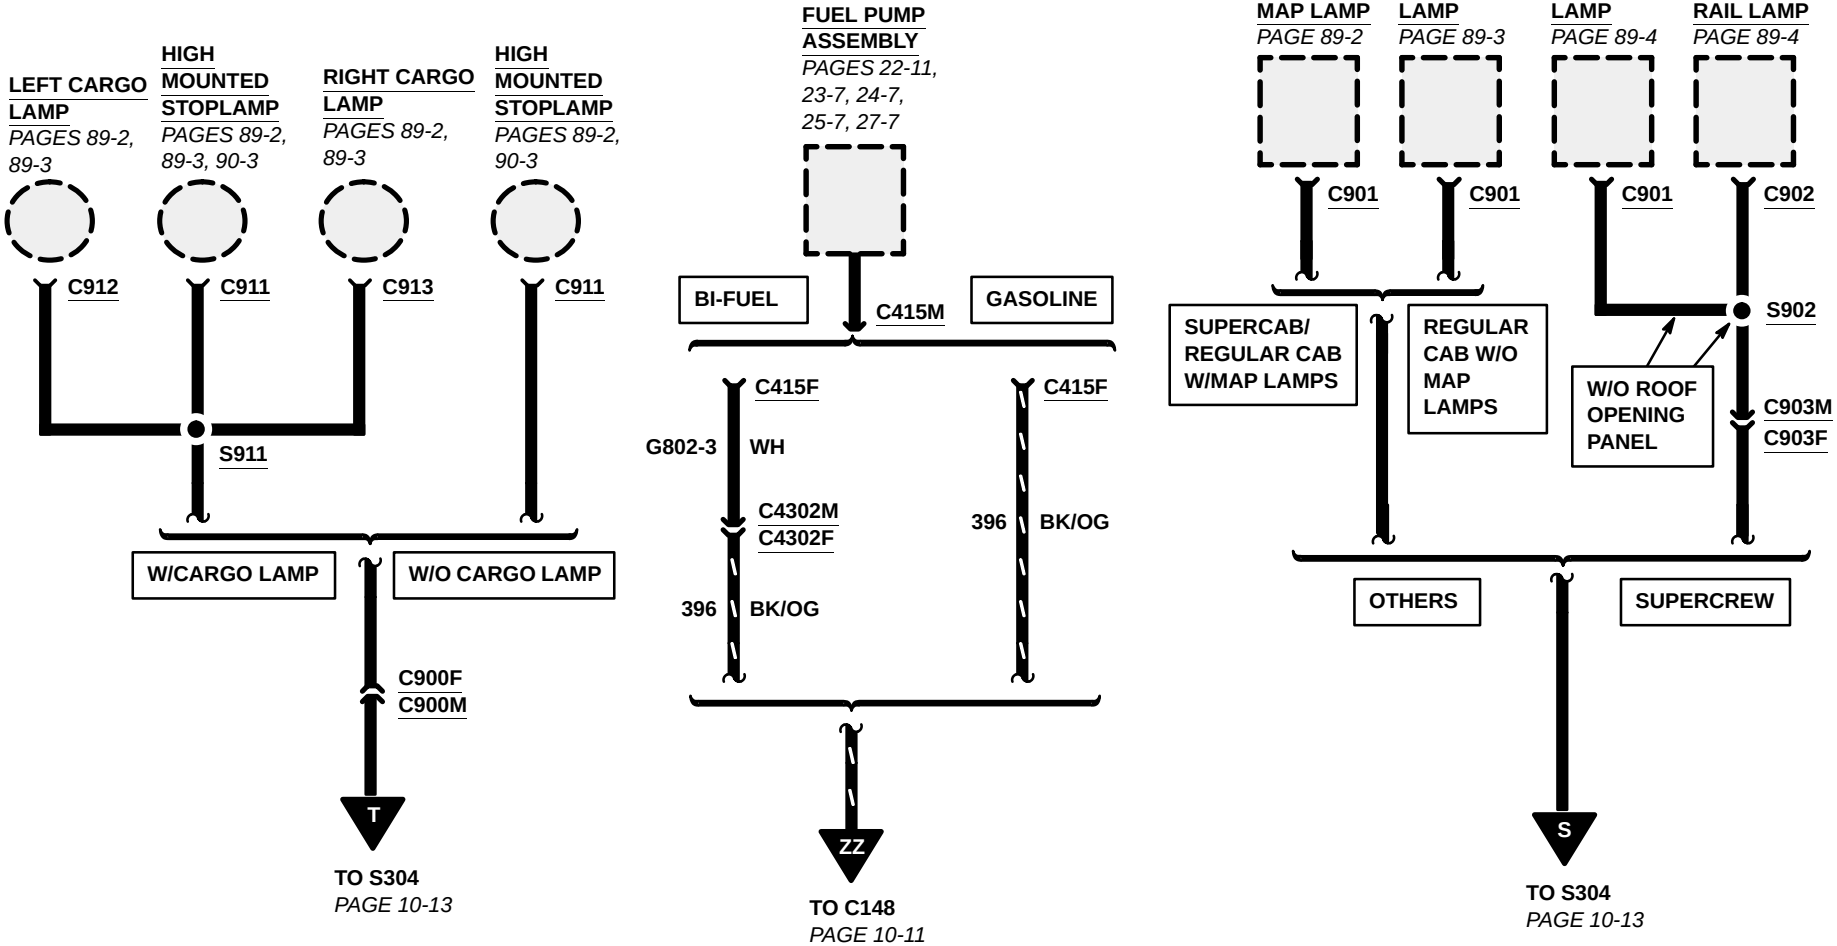
All Circuits are 57 BK unless otherwise noted.