W/O POWER EQUIPMENT
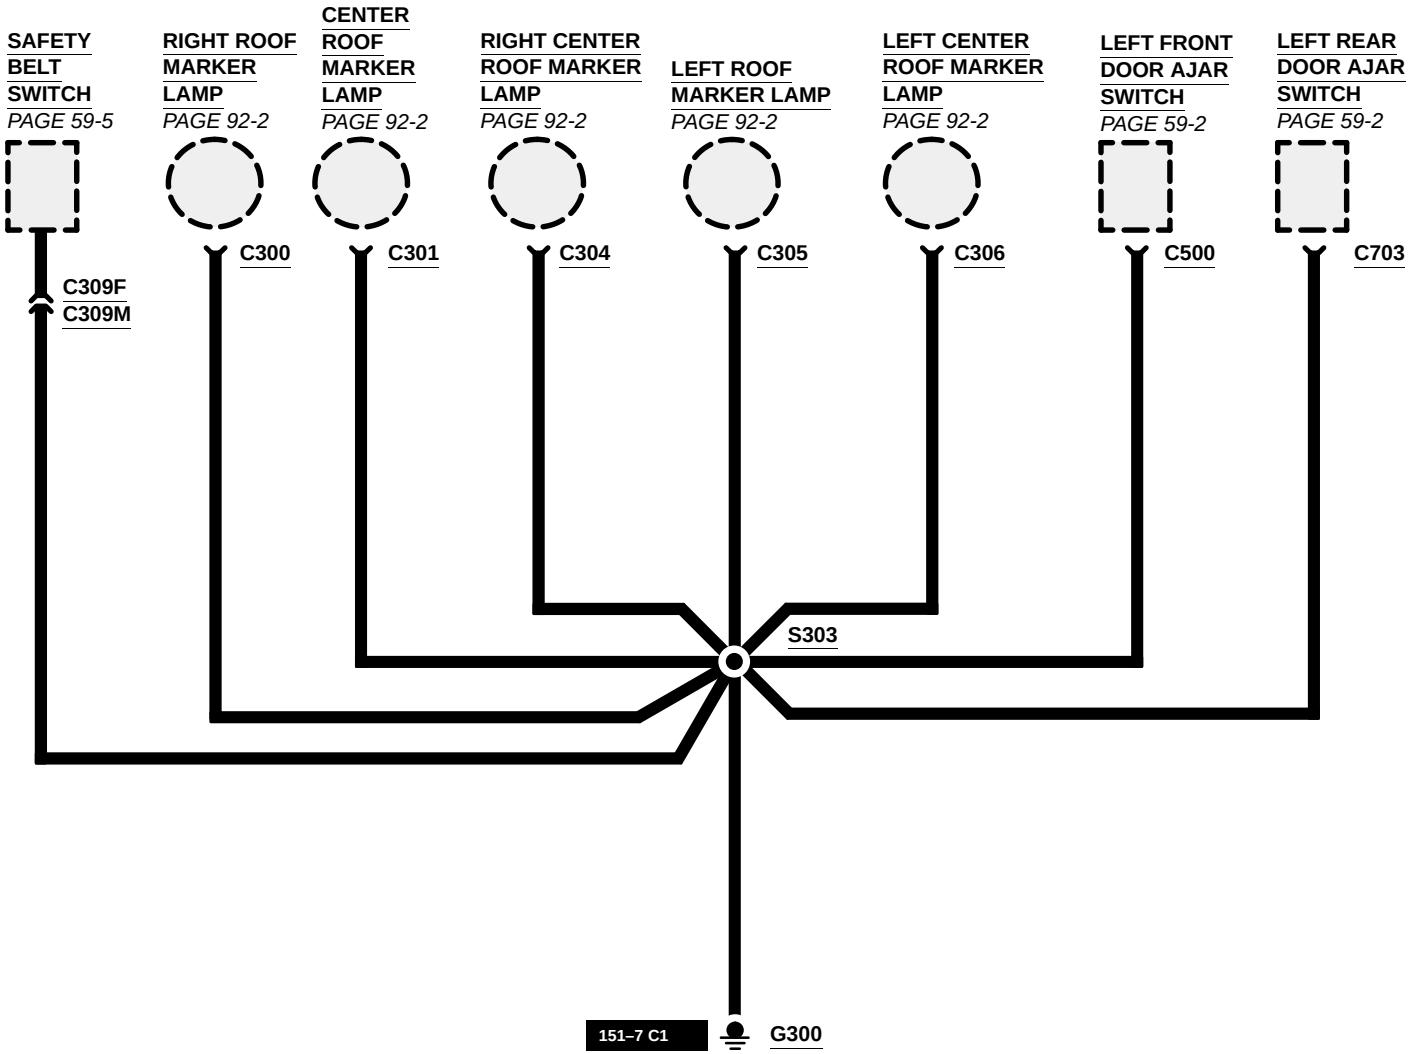
All wires are 57 (BK) unless otherwise noted.