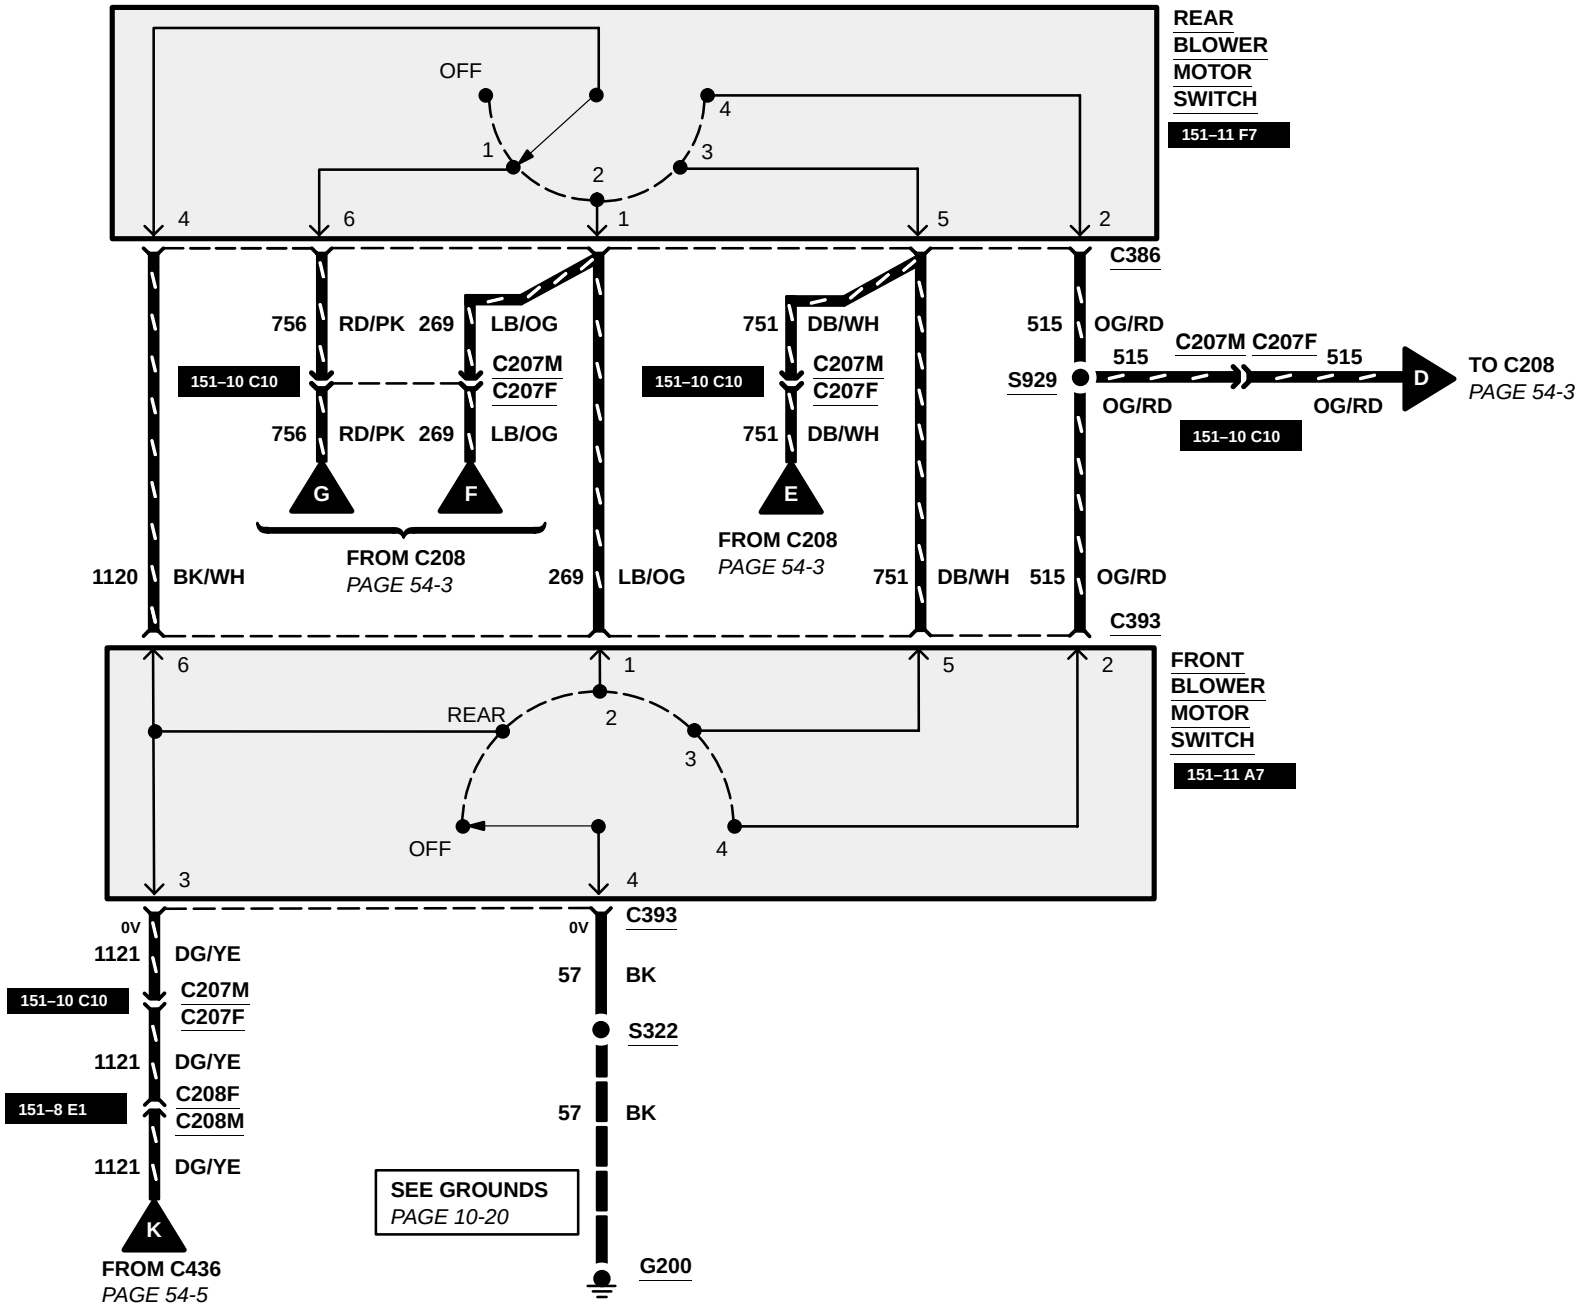W/ROOF OPENING PANEL