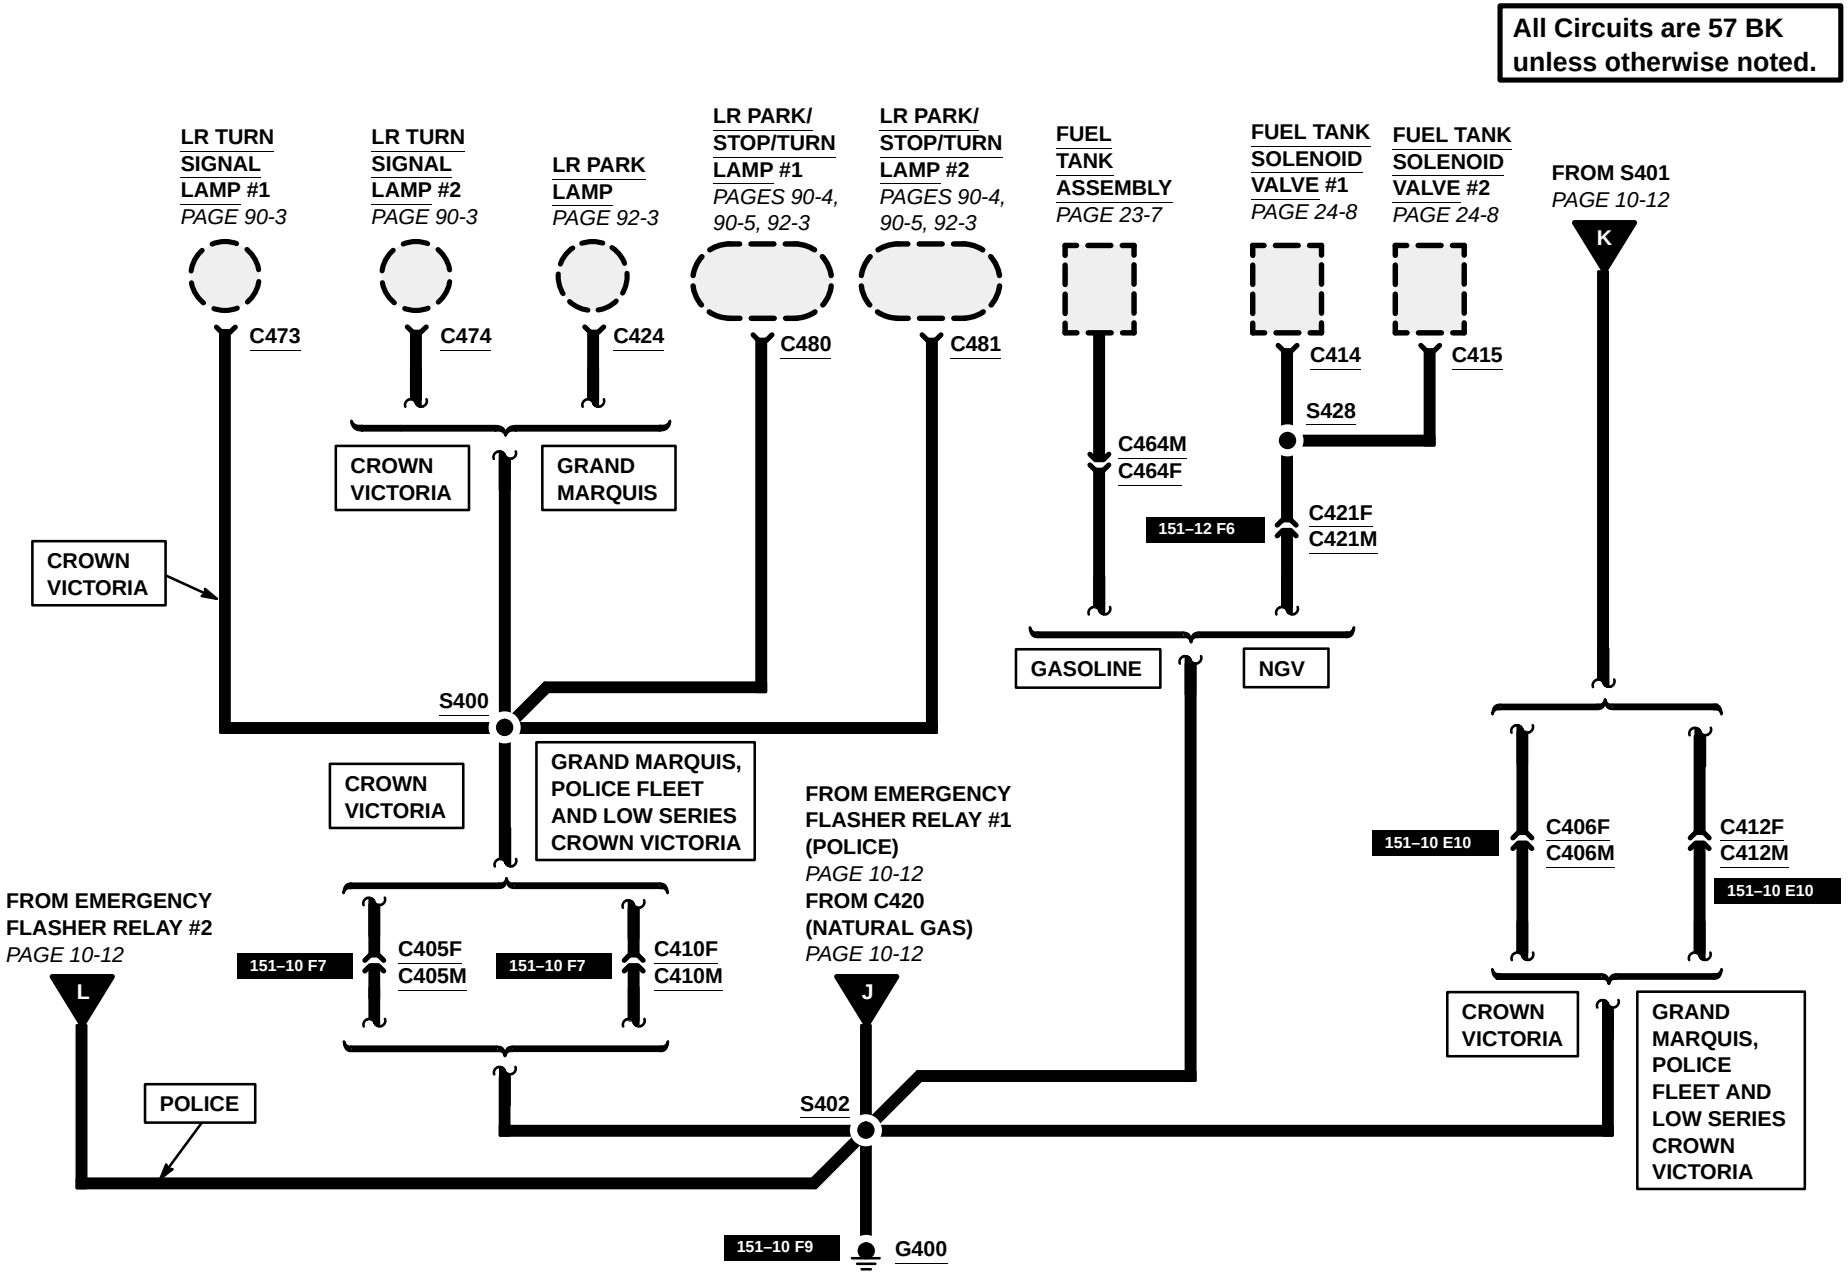10-11 GROUNDS