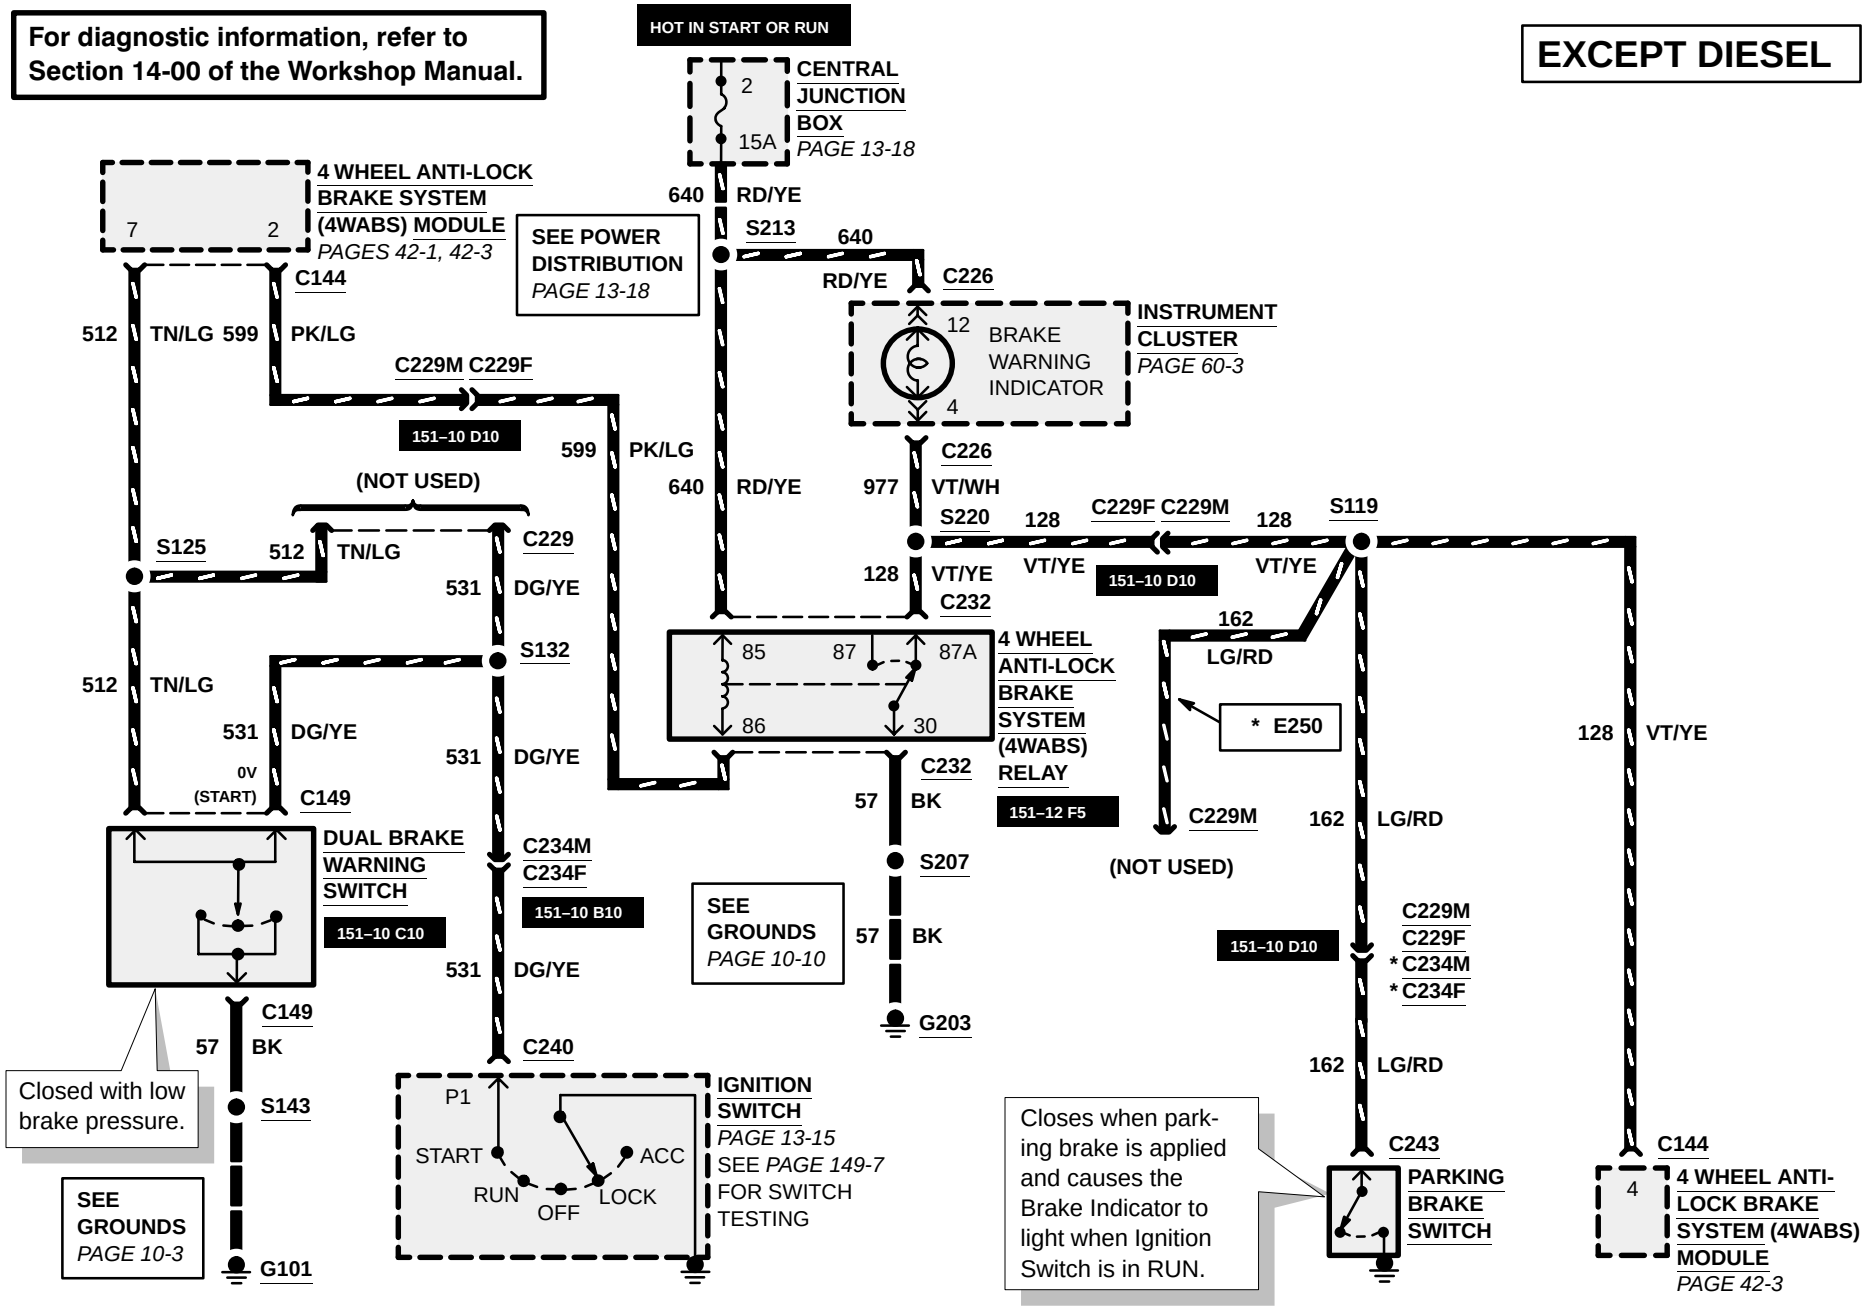65-1 WARNING INDICATORS