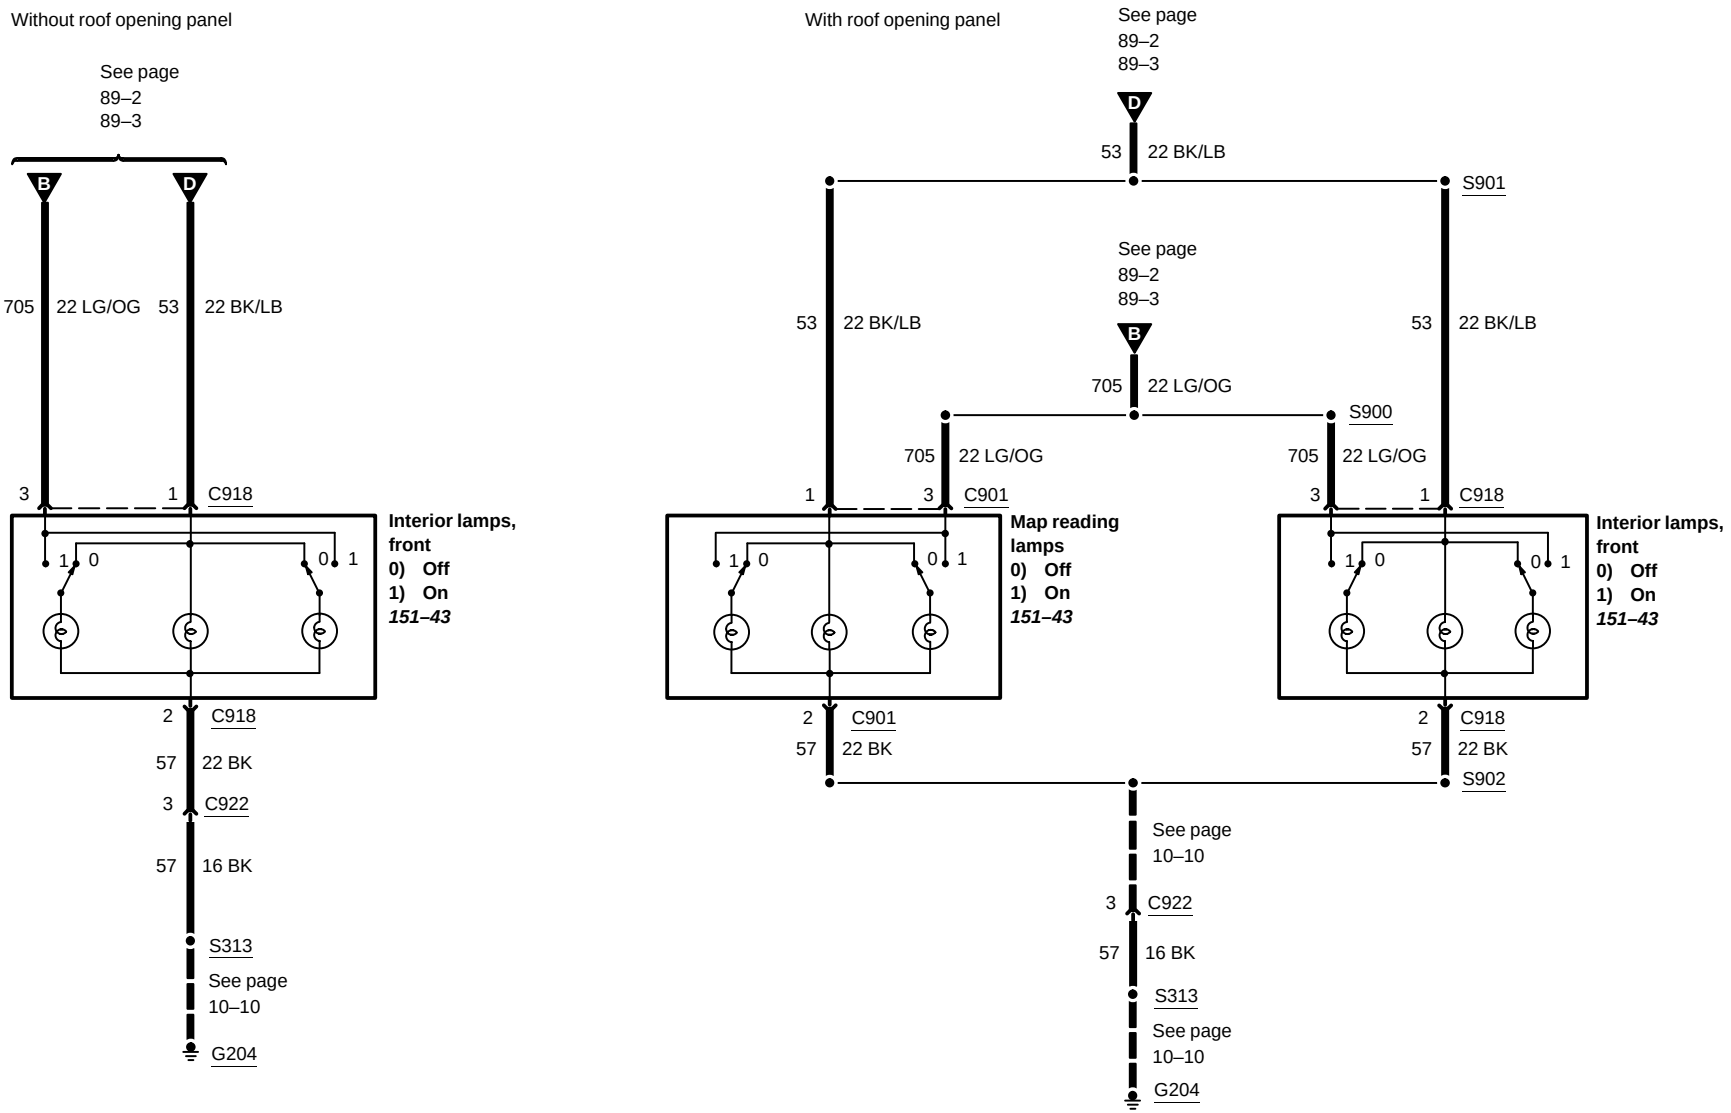
Without roof opening panel
See page
89–2
89–3
B
D
705 22 LG/OG
53 22 BK/LB
3
1
C918
Interior lamps, front
0) Off
1) On
151–43
2
C918
57 22 BK
3
C922
57 16 BK
S313
See page
10–10
G204
With roof opening panel
See page
89–2
89–3
D
53 22 BK/LB
S901
See page
89–2
89–3
53 22 BK/LB
B
705 22 LG/OG
S900
705 22 LG/OG
705 22 LG/OG
53 22 BK/LB
1
3
C901
Map reading lamps
0) Off
1) On
151–43
3
1
C918
Interior lamps, front
0) Off
1) On
151–43
2
C901
57 22 BK
2
C918
57 22 BK
S902
See page
10–10
3
C922
57 16 BK
S313
See page
10–10
G204