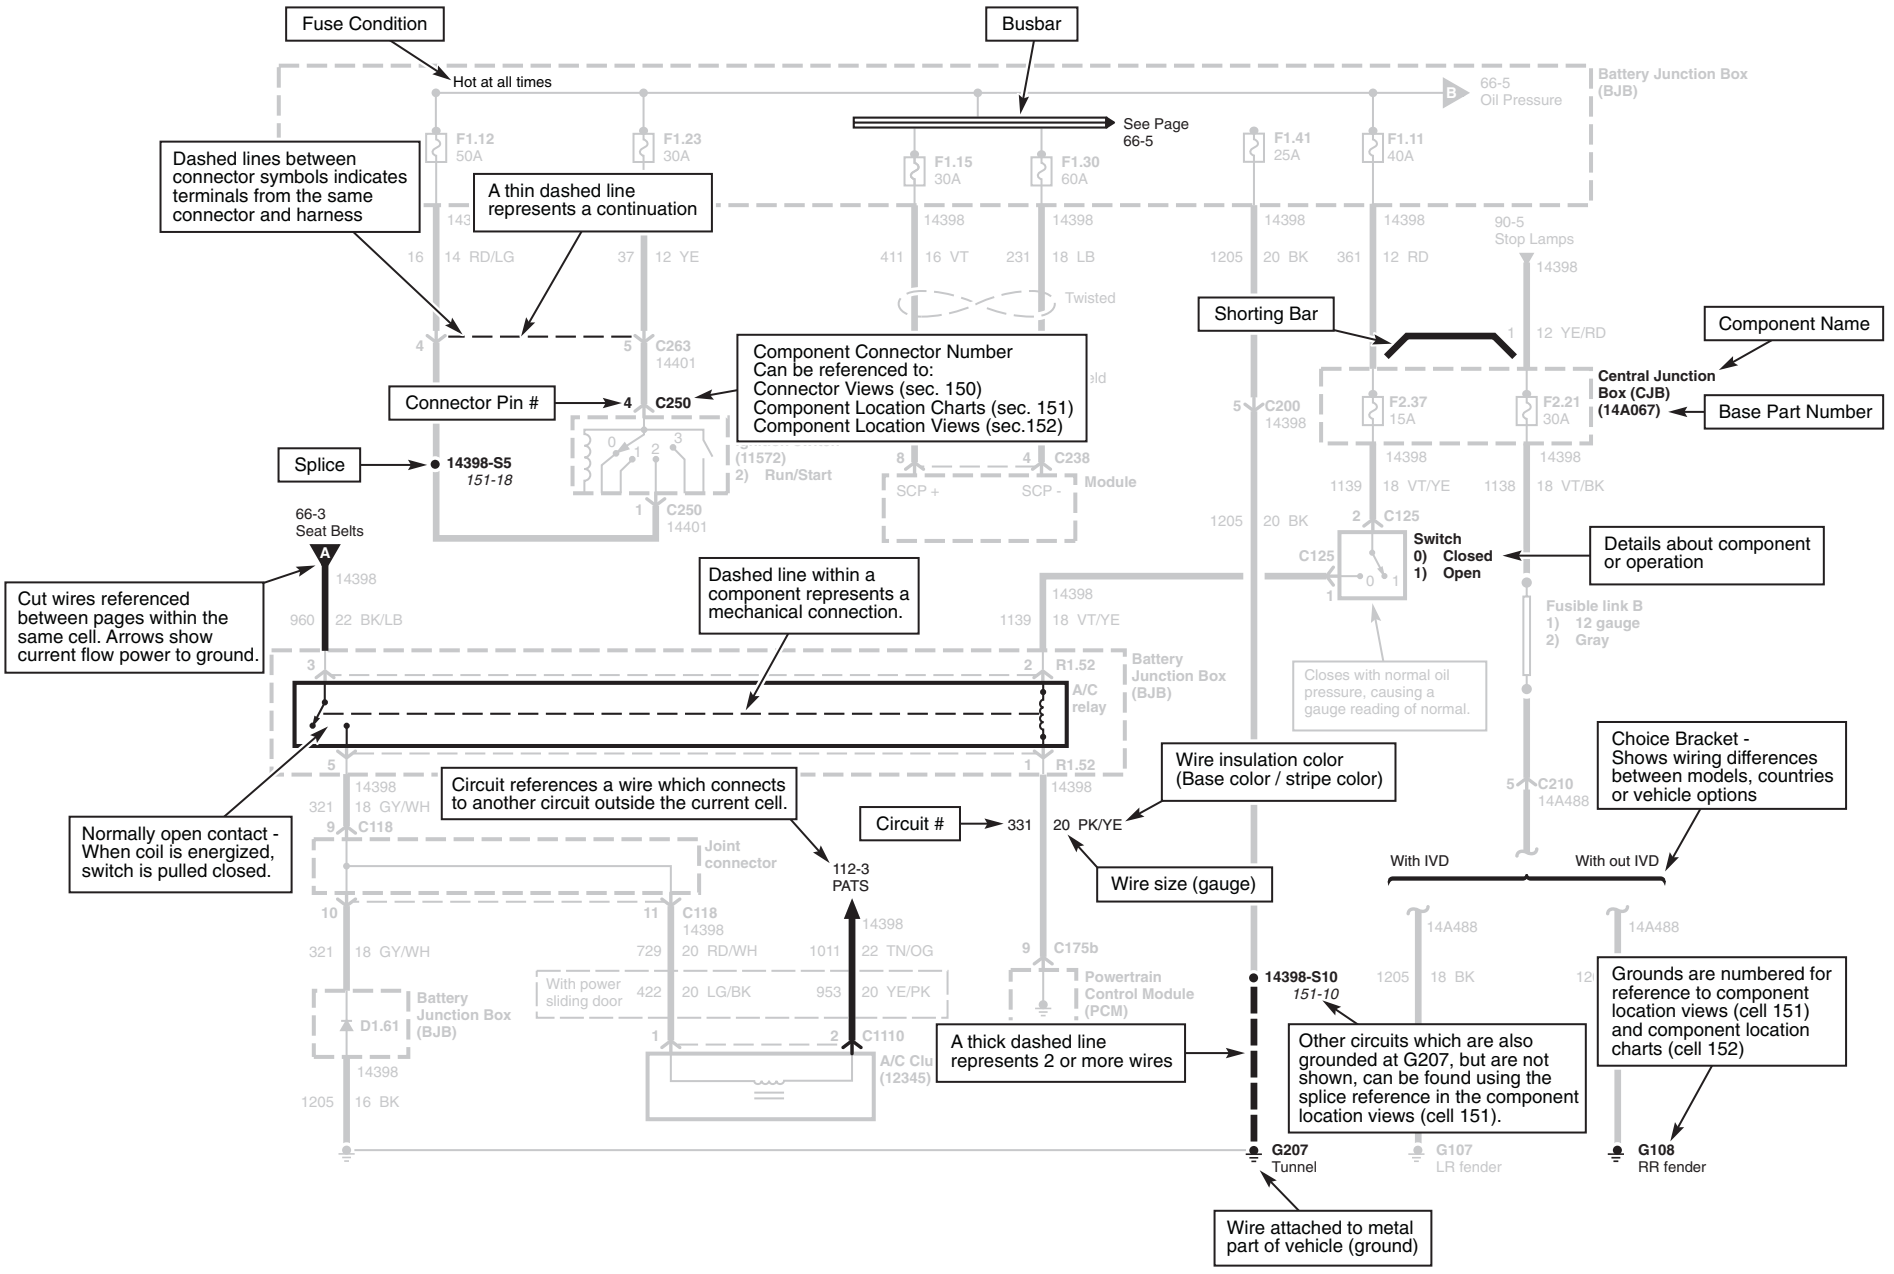

Note: Above schematic is for reference to page elements only. The information represented in the above schematic is NOT valid system information.