10-5 GROUNDS
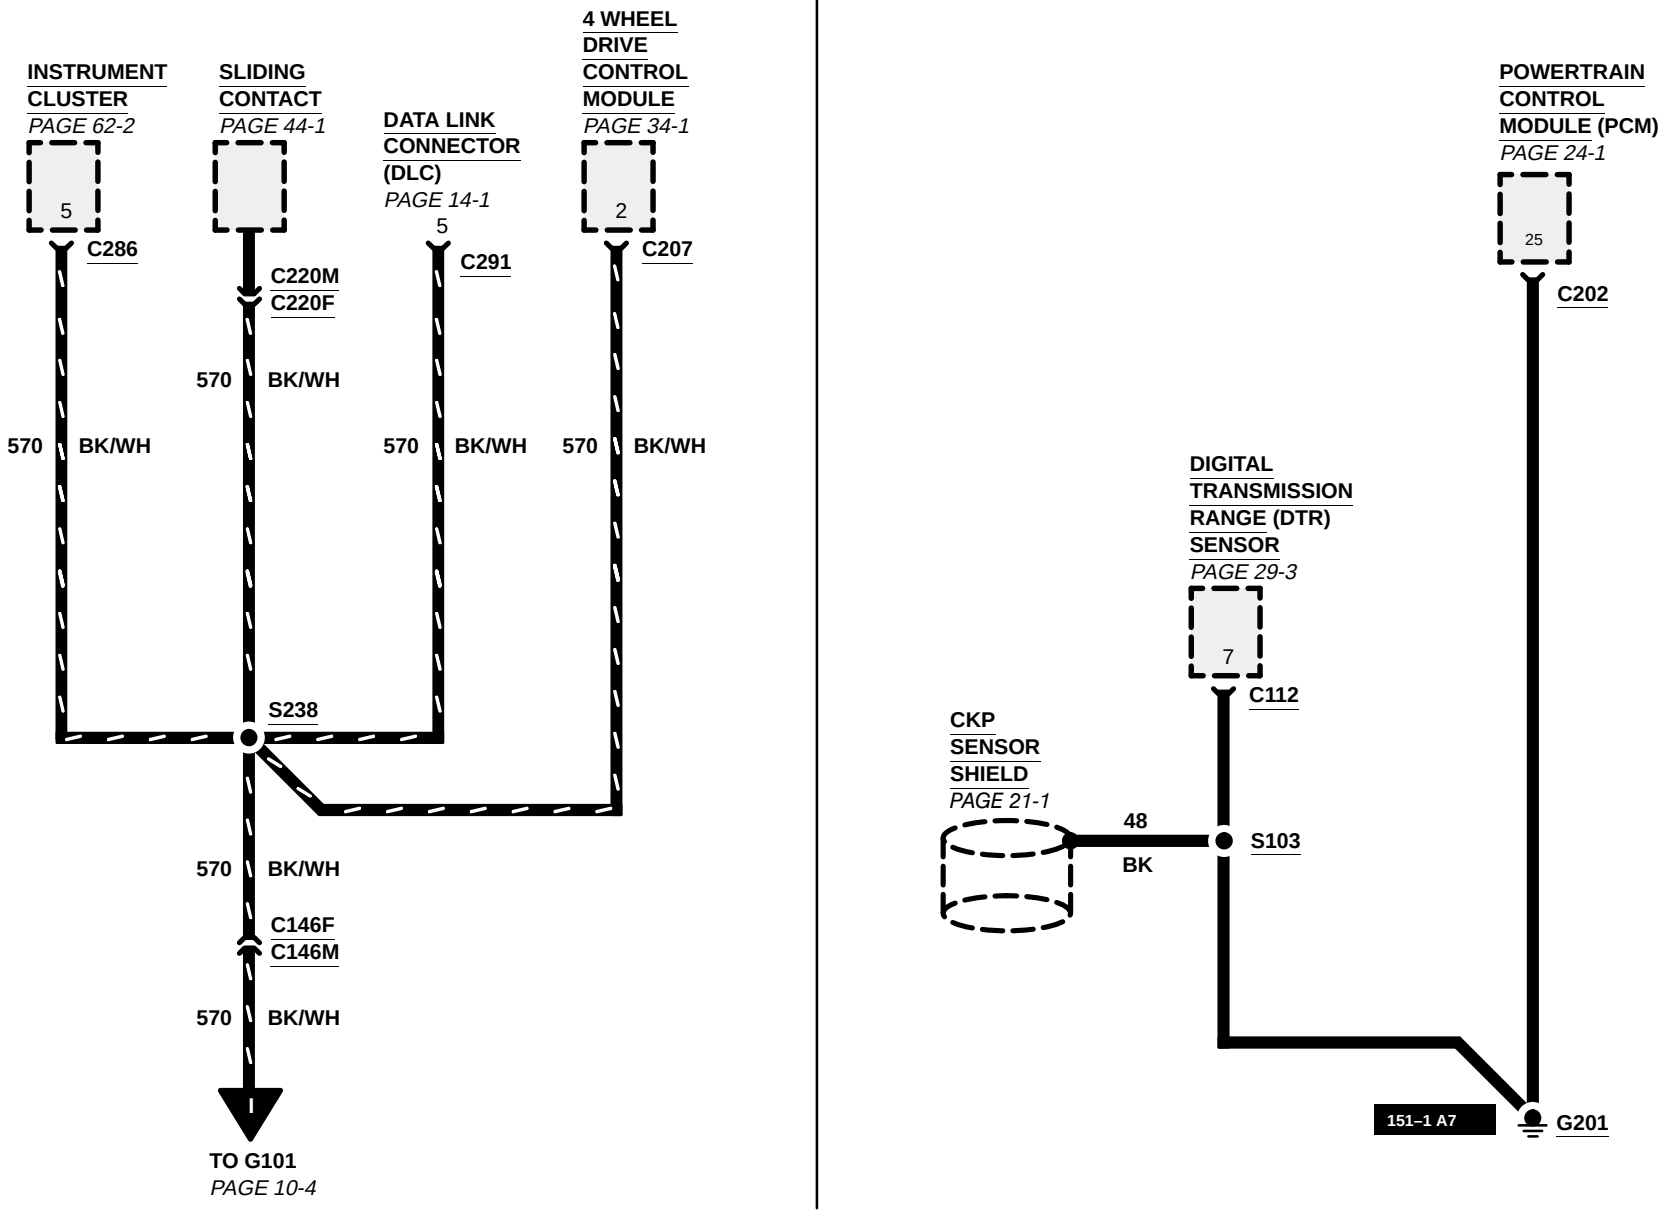
All wires are 57 (BK) unless otherwise noted.