151-7 COMPONENT LOCATION VIEWS

2001 TOWN CAR

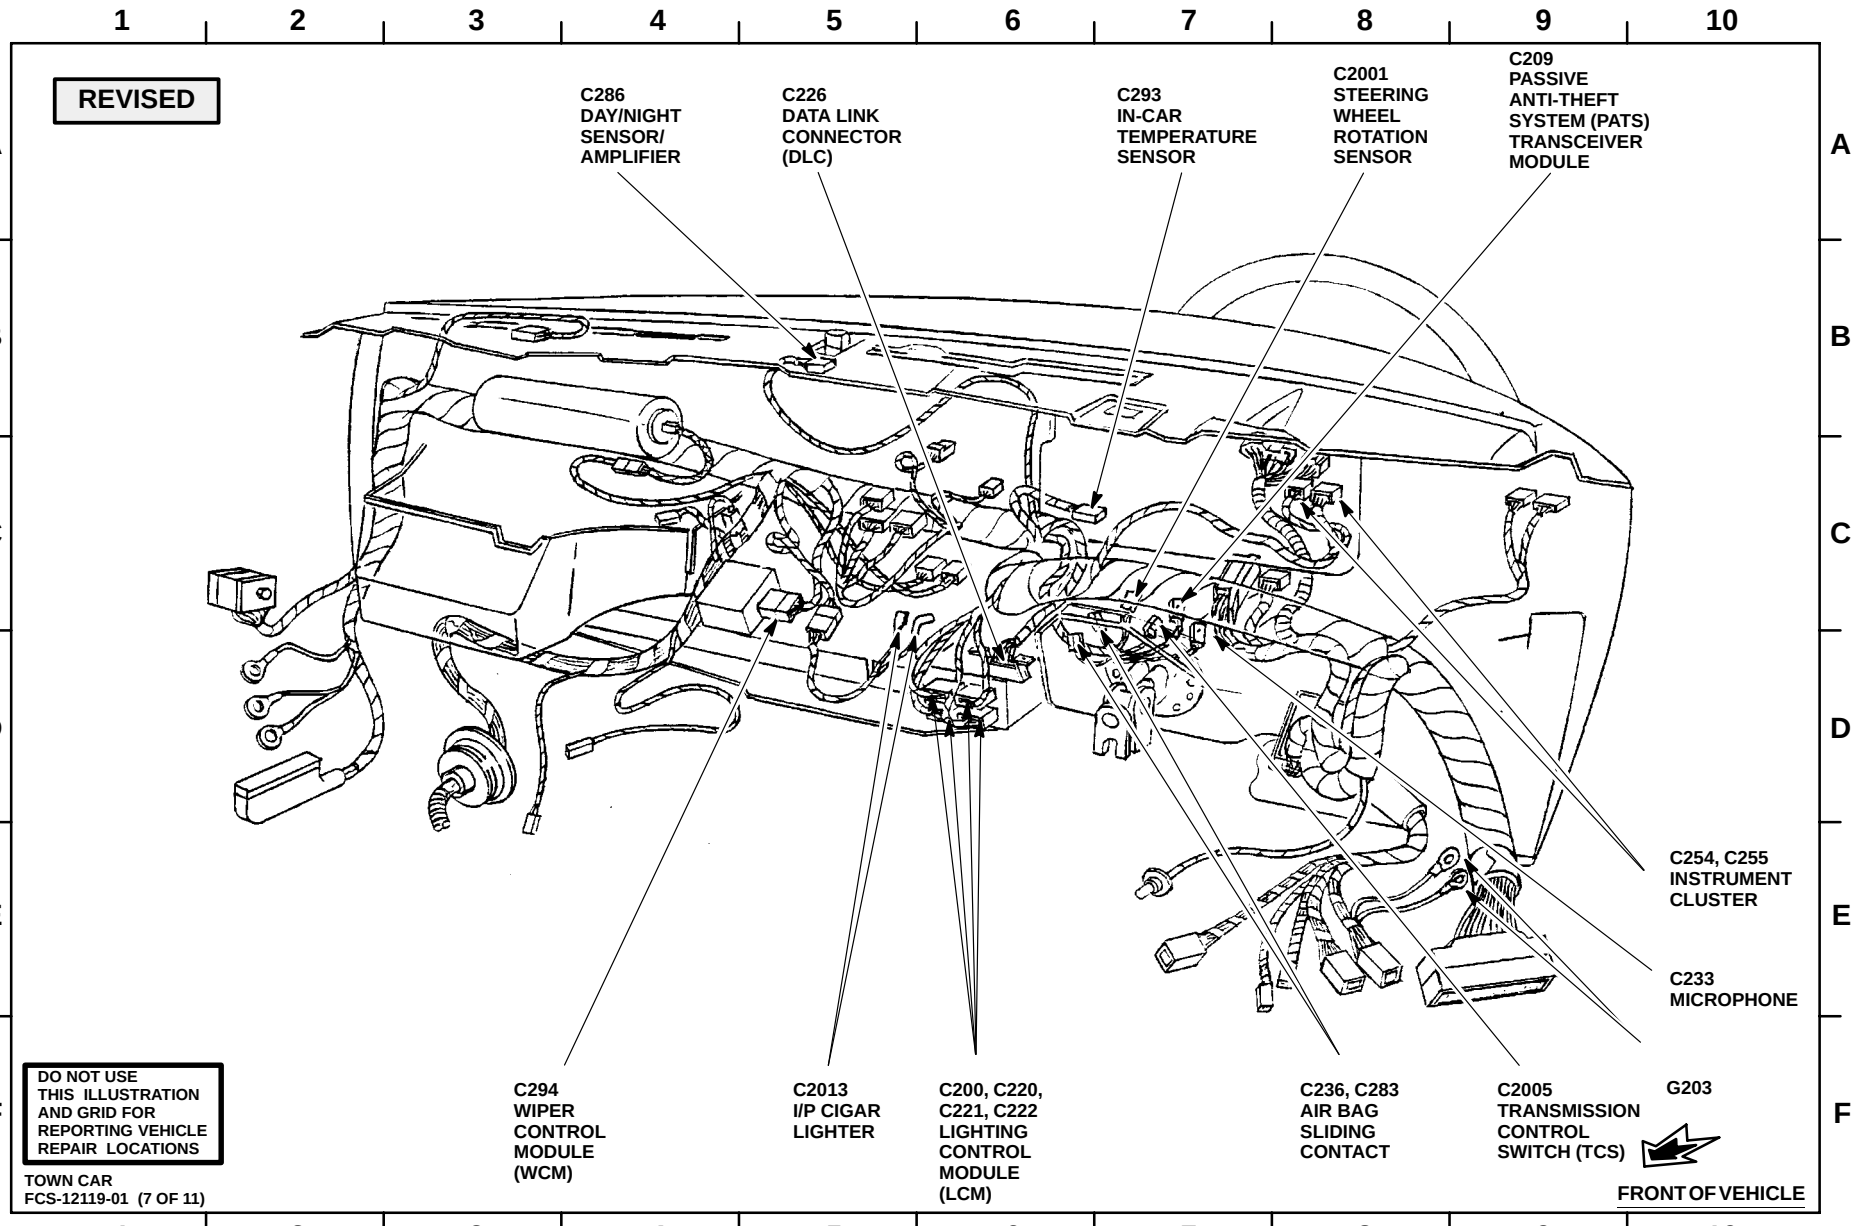

I/P VIEW (2 OF 2)