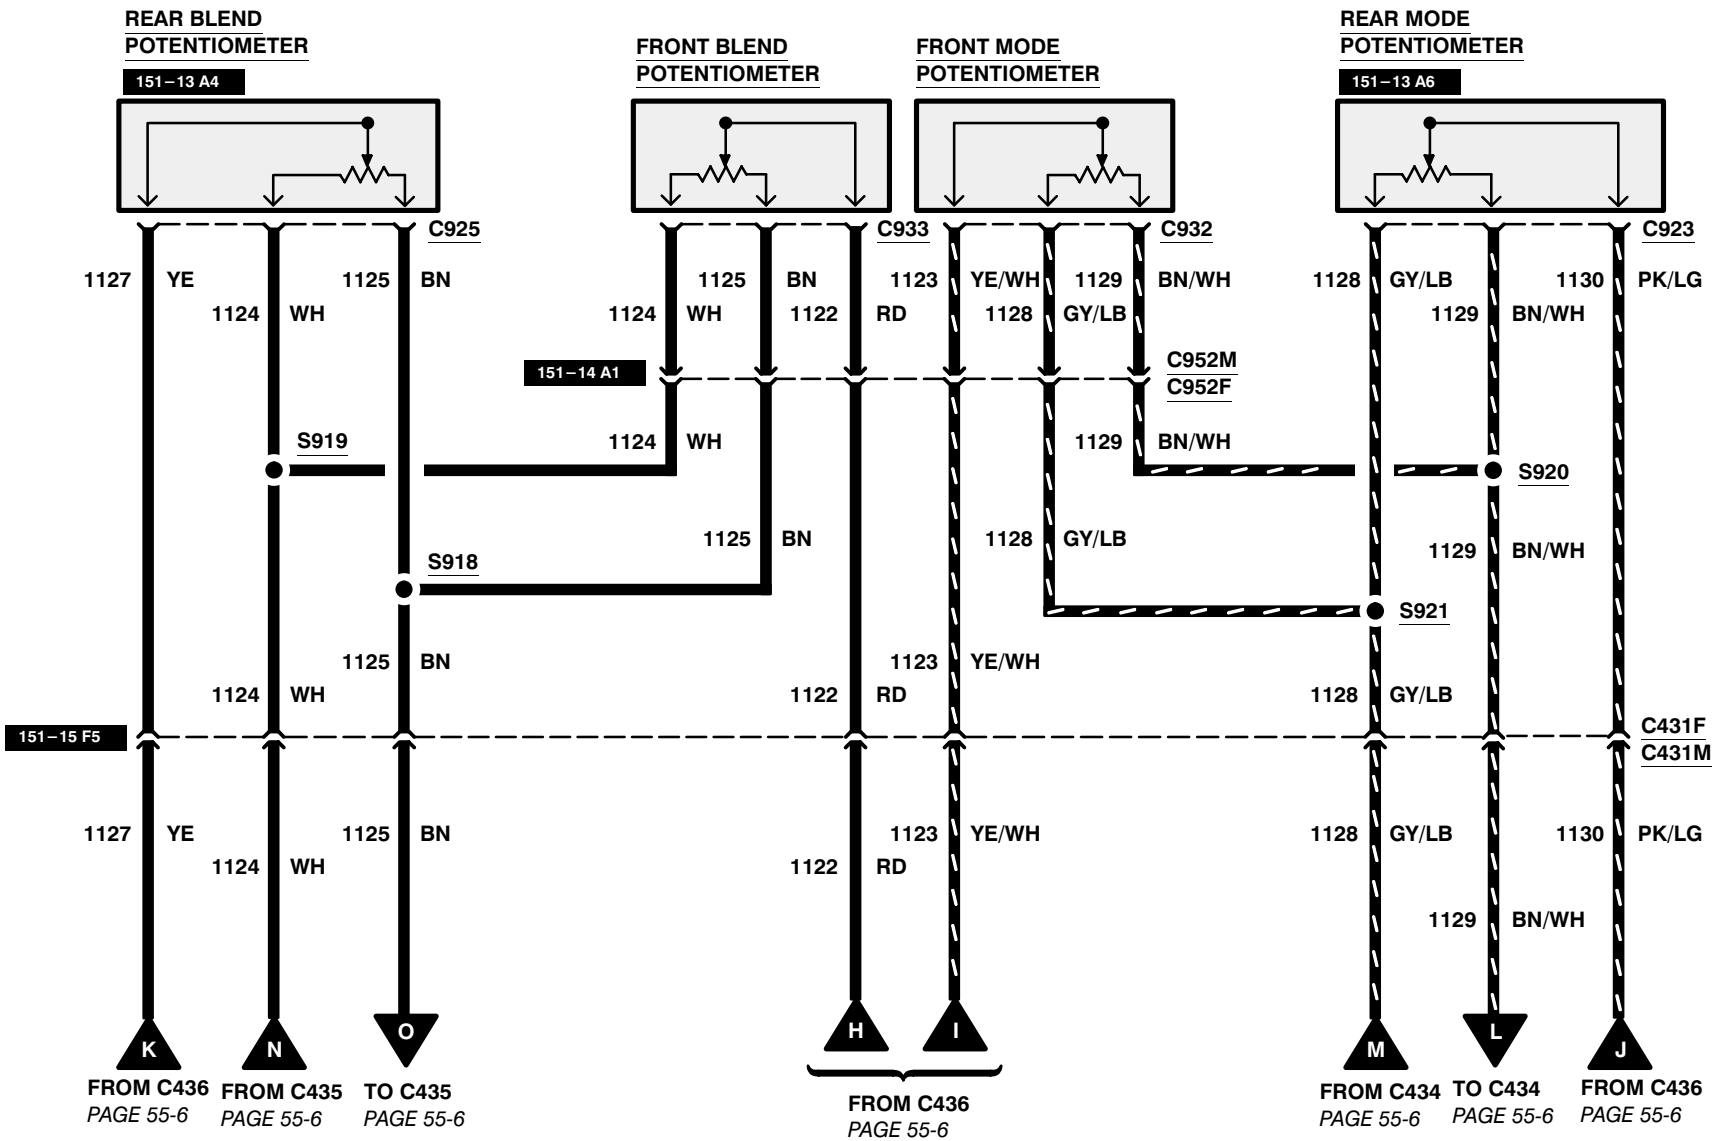EXPEDITION W/O ROOF OPENING PANEL