10-5 GROUNDS

All Circuits are 57 BK unless otherwise noted.
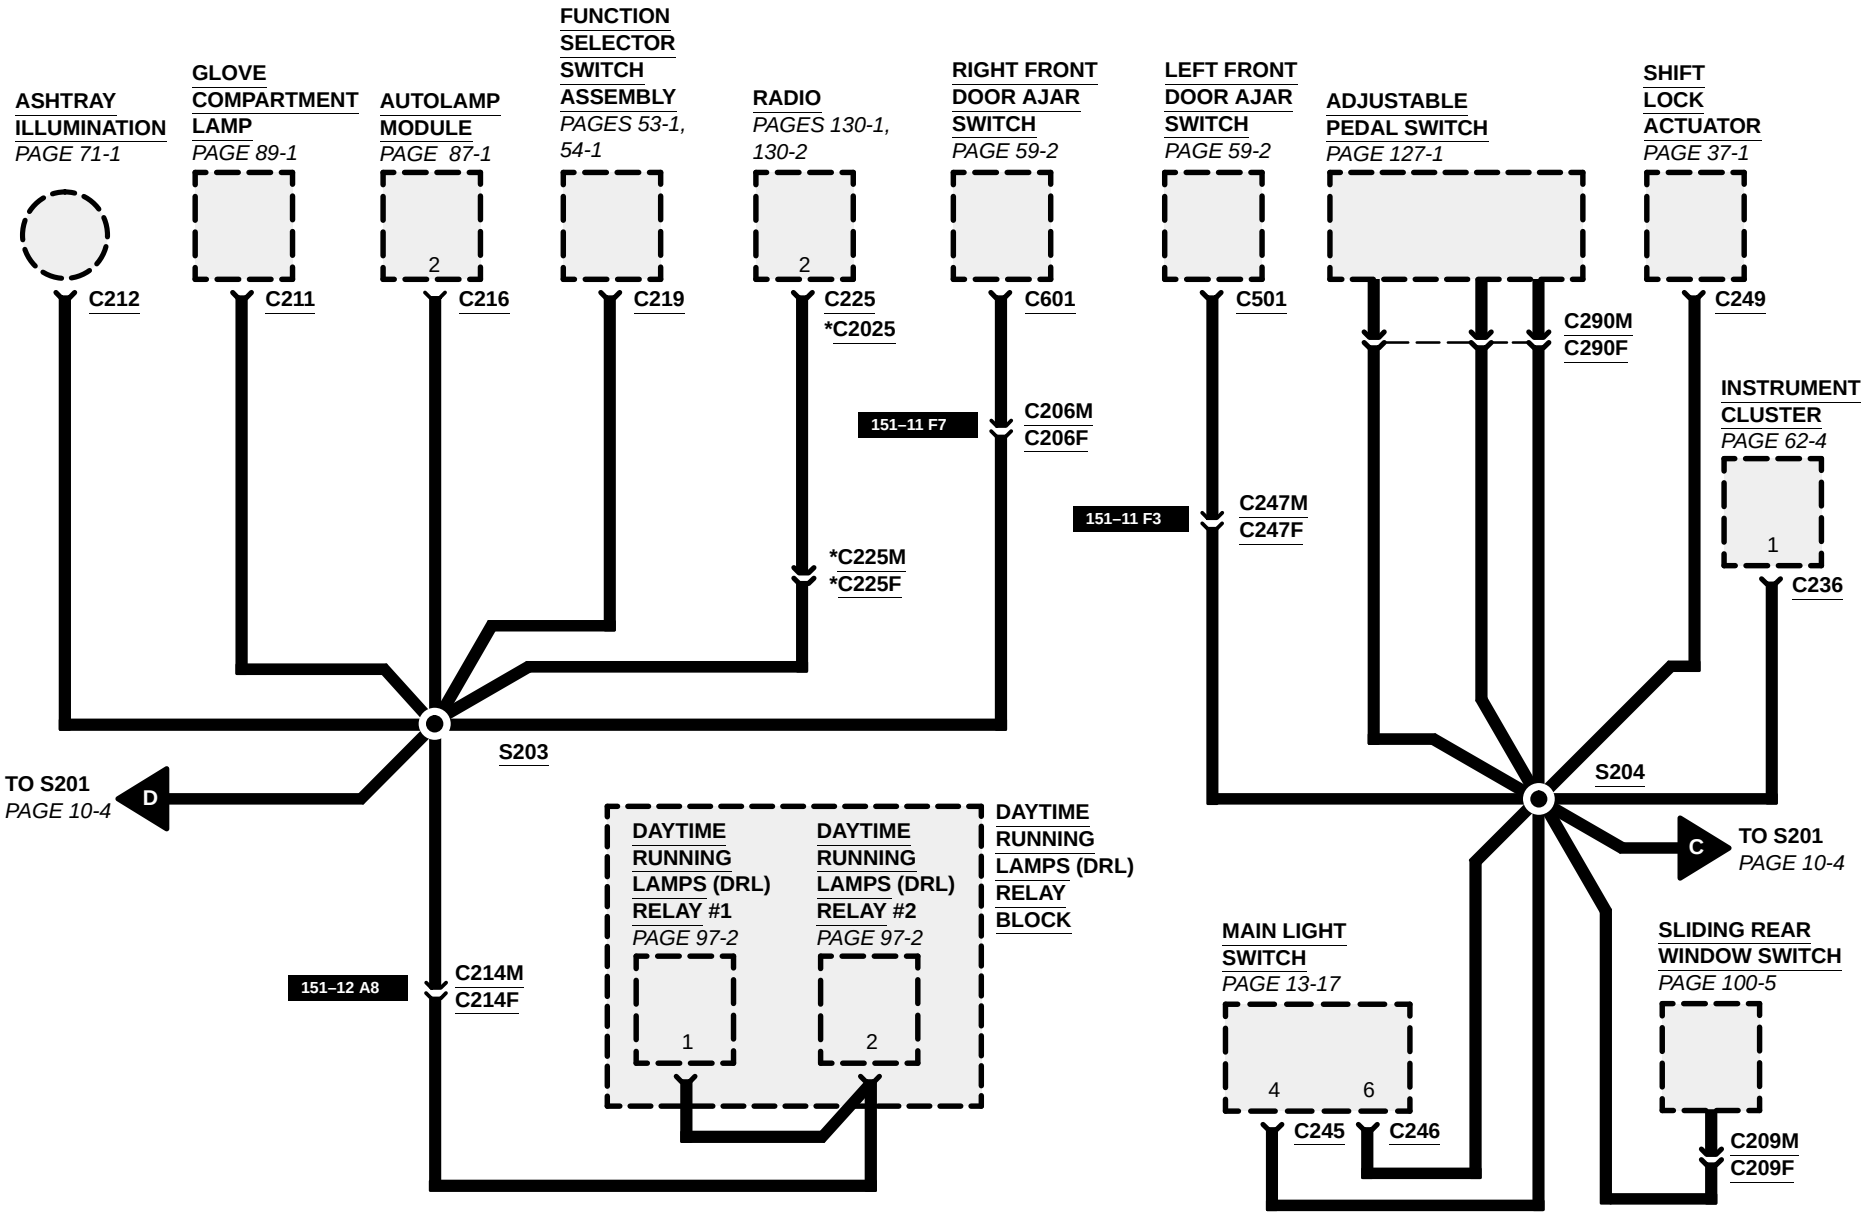
*** W/REAR SEAT ENTERTAINMENT**