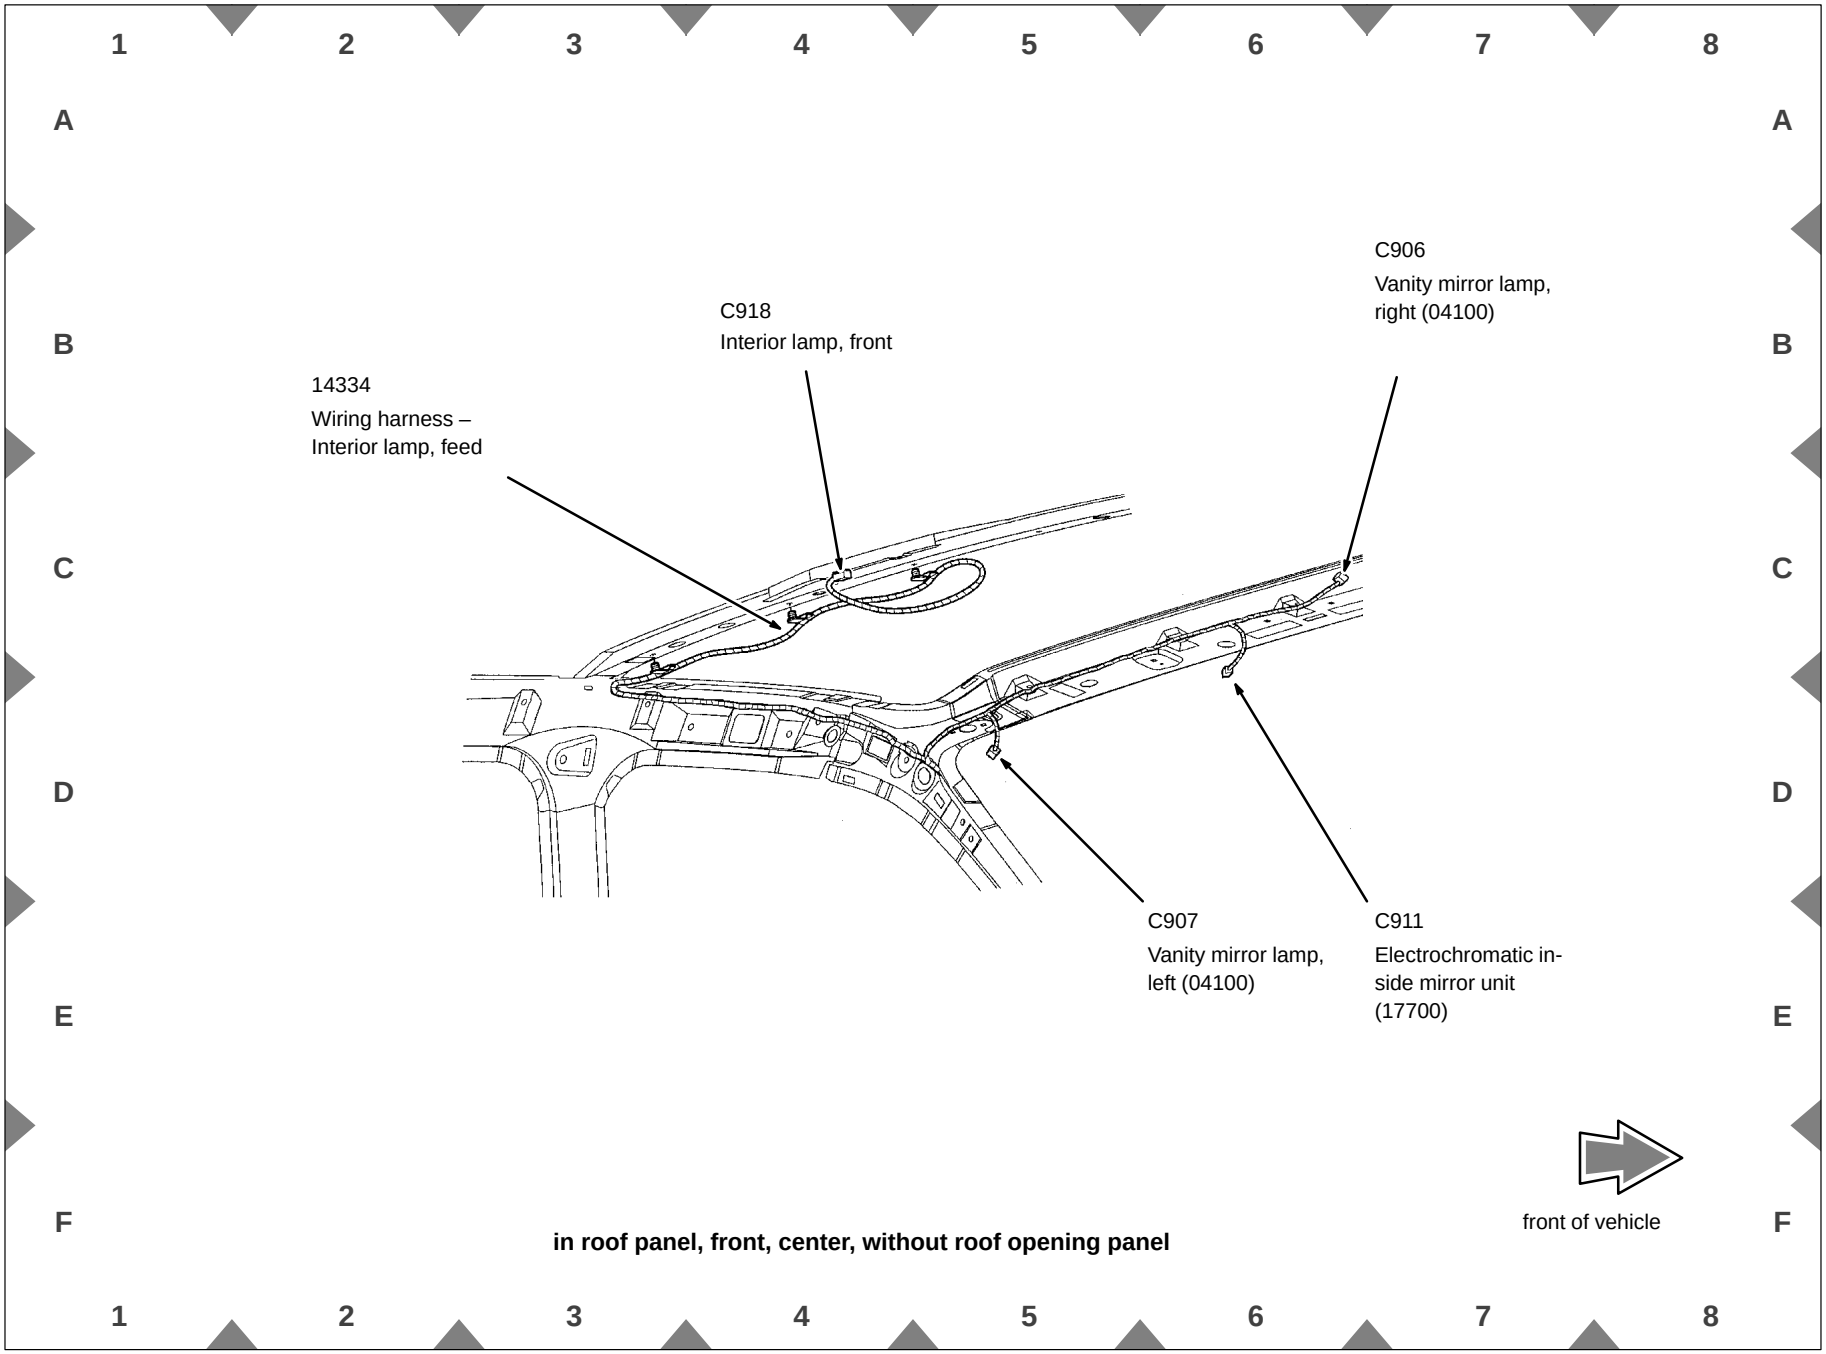

in roof panel, front, center, without roof opening panel