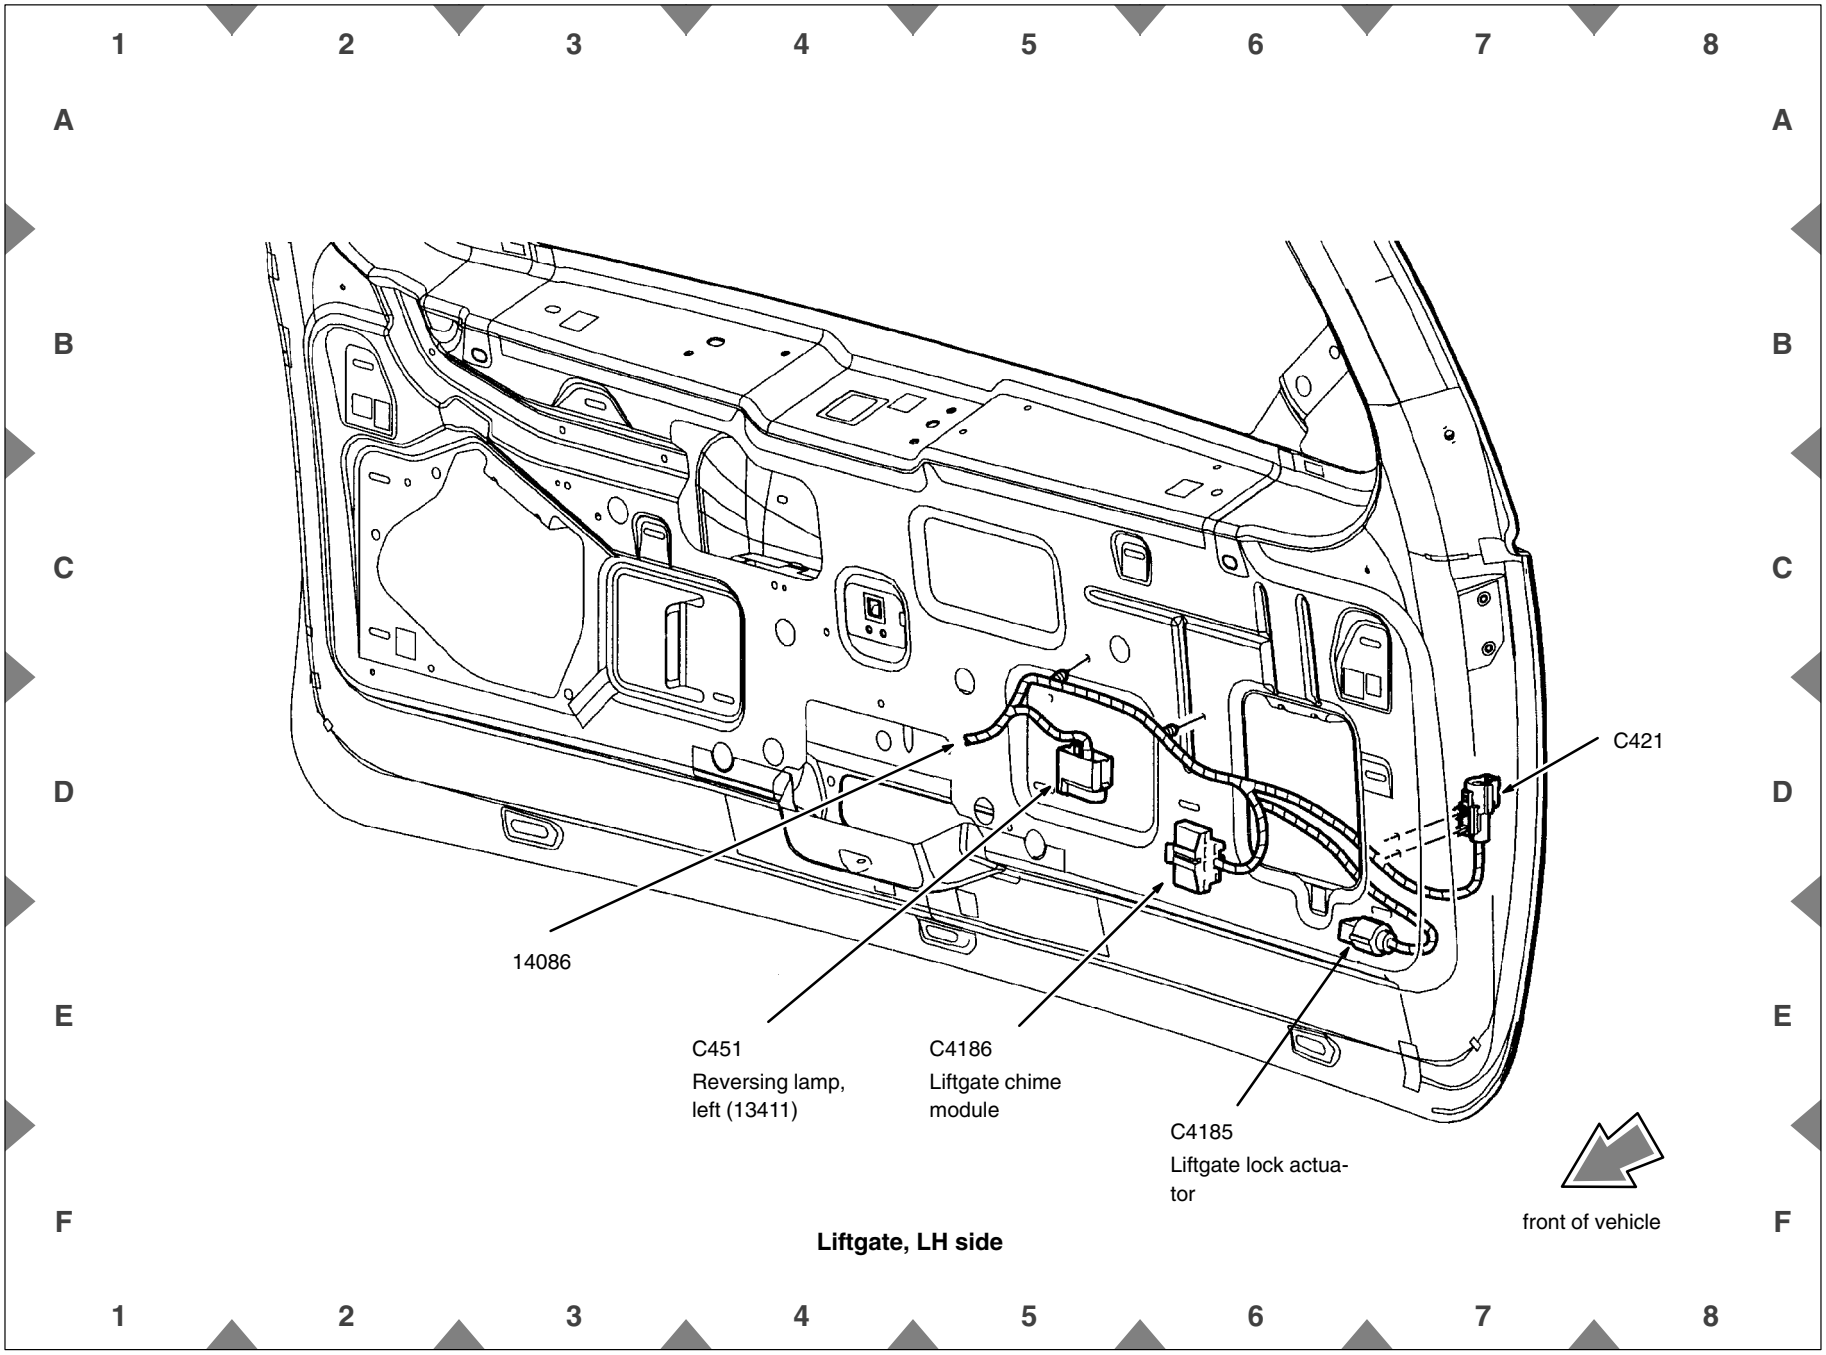

Liftgate, LH side