151-7 COMPONENT LOCATION VIEWS

2001 CROWN VICTORIA/GRAND MARQUIS

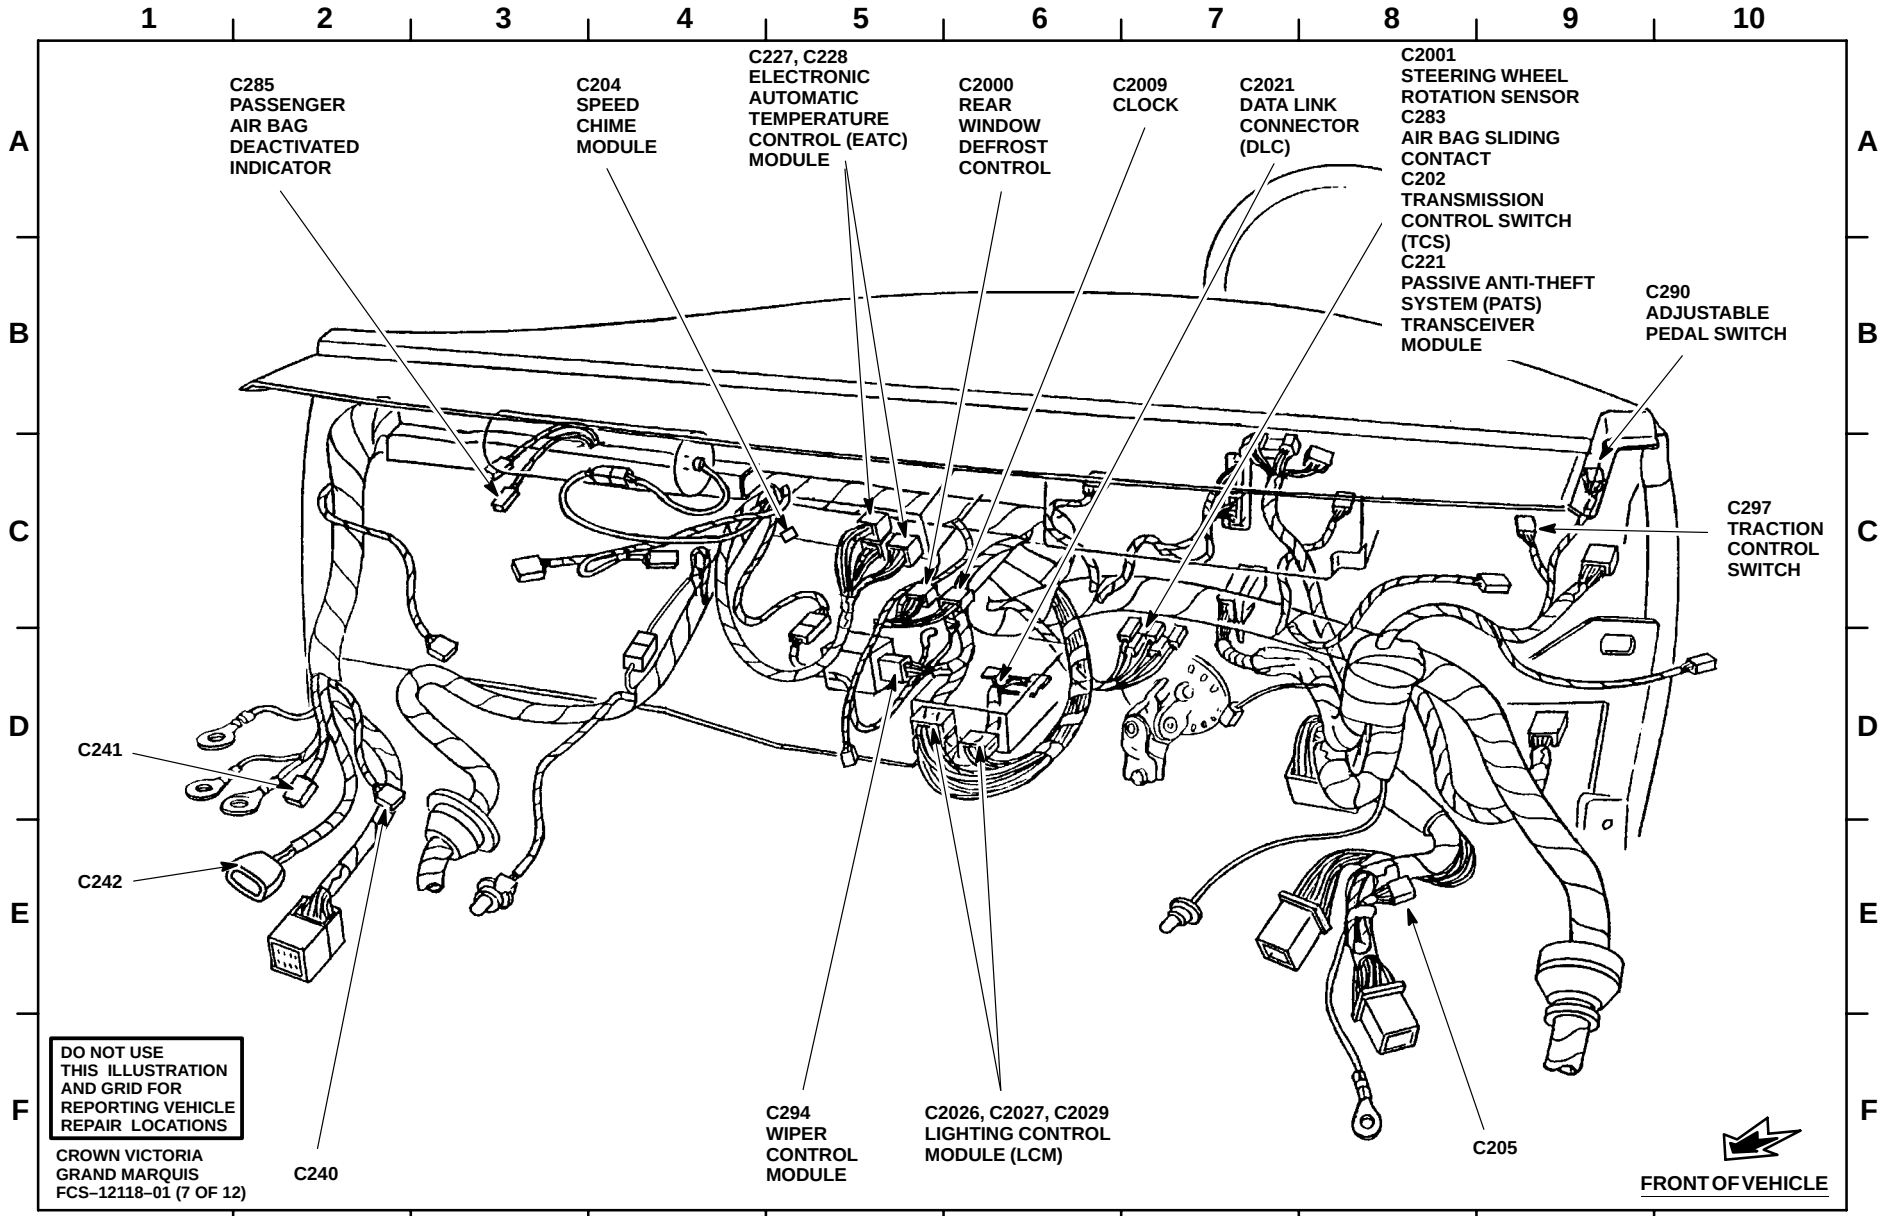

I/P VIEW (2 OF 2)