TERMINALS

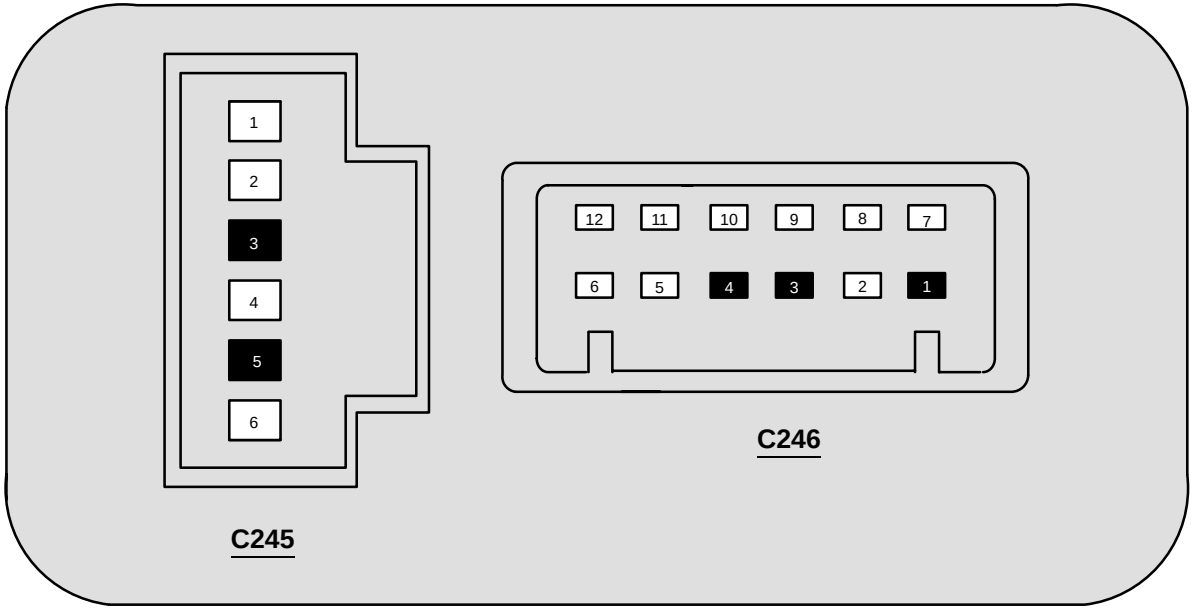
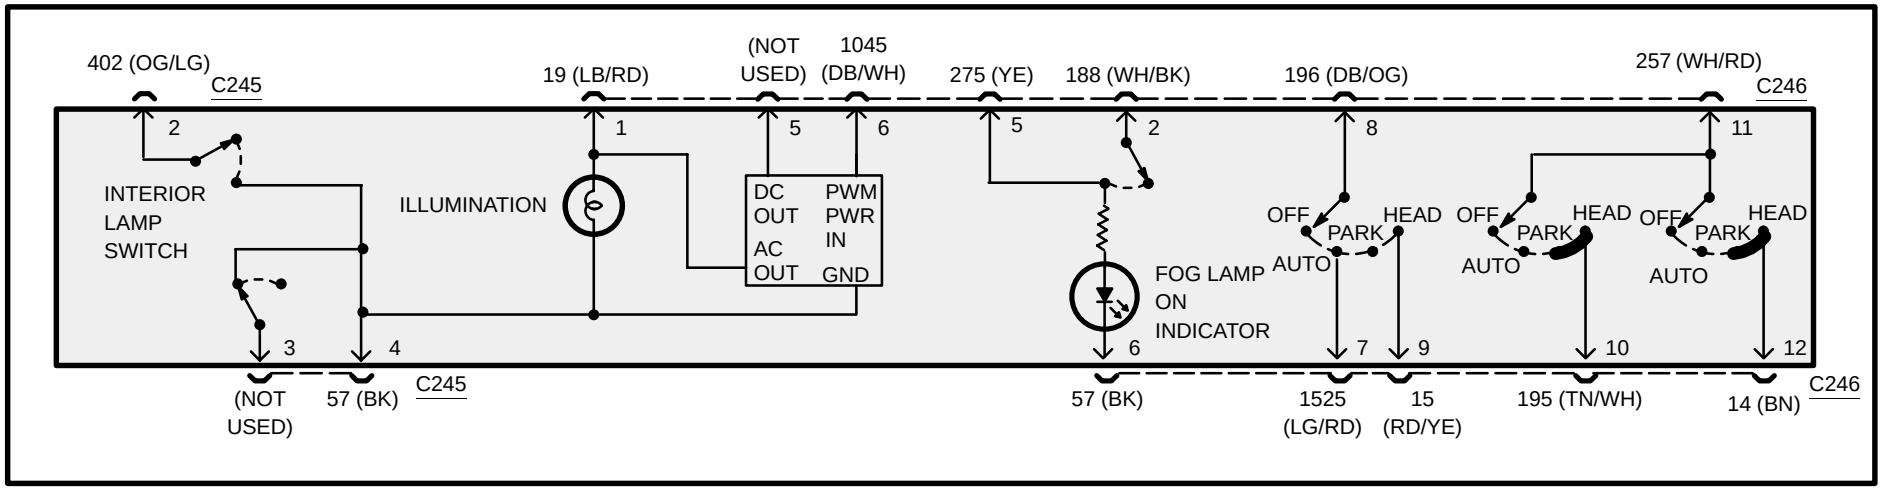
SCHEMATIC