10-19 GROUNDS

All wires are 57 (BK) unless otherwise noted.

PICKUP

* DIESEL
** CALIFORNIA
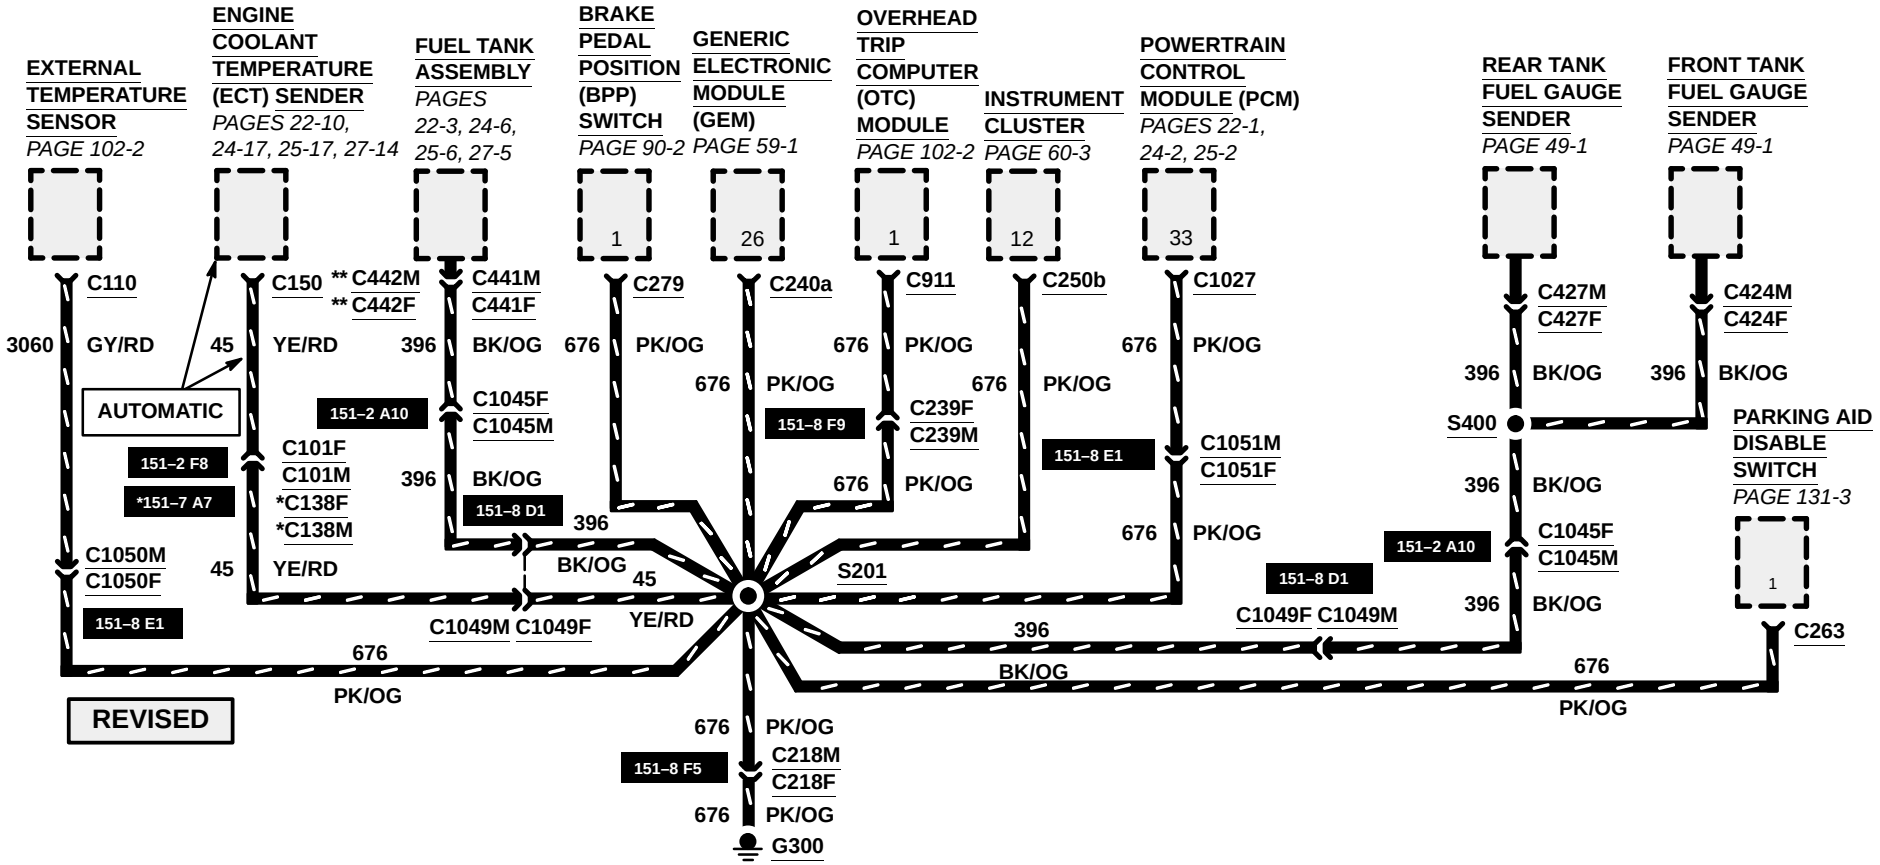
REVISED