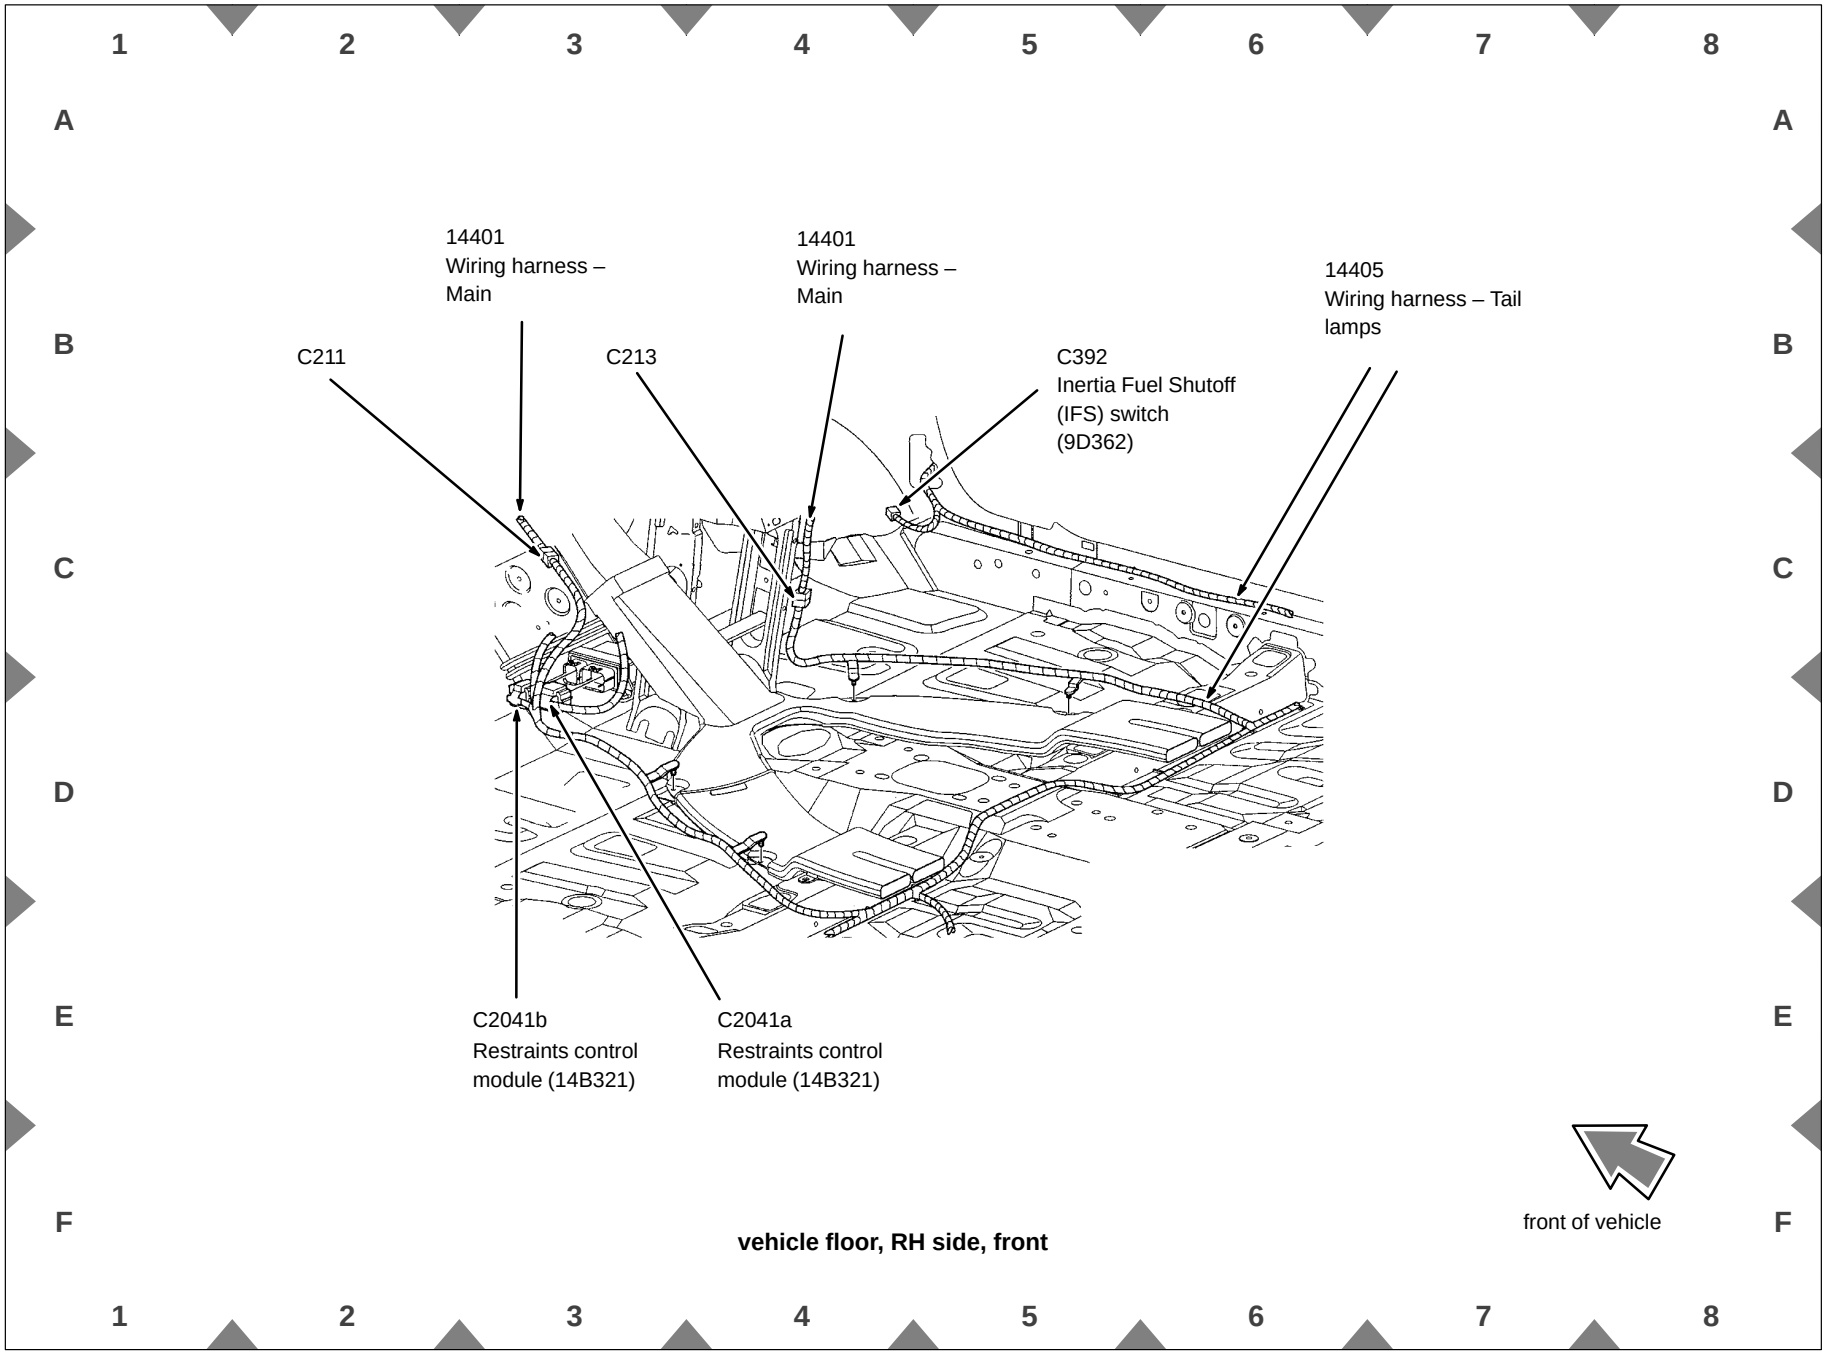

vehicle floor, RH side, front