SCHEMATIC
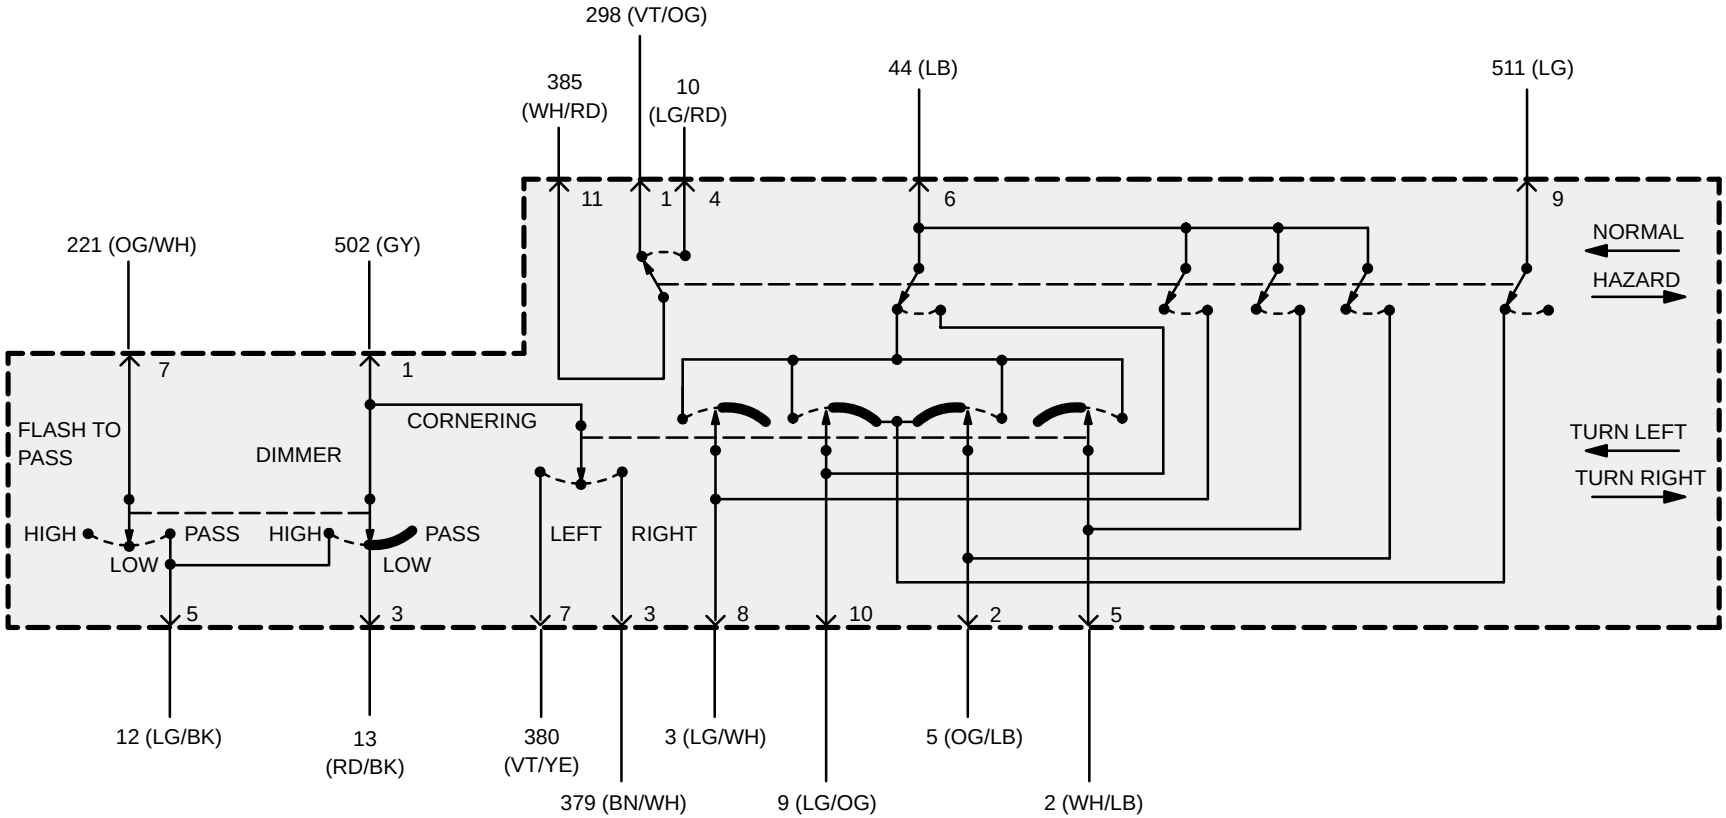
LAMP PORTION