All wires are 57 (BK) unless otherwise noted.
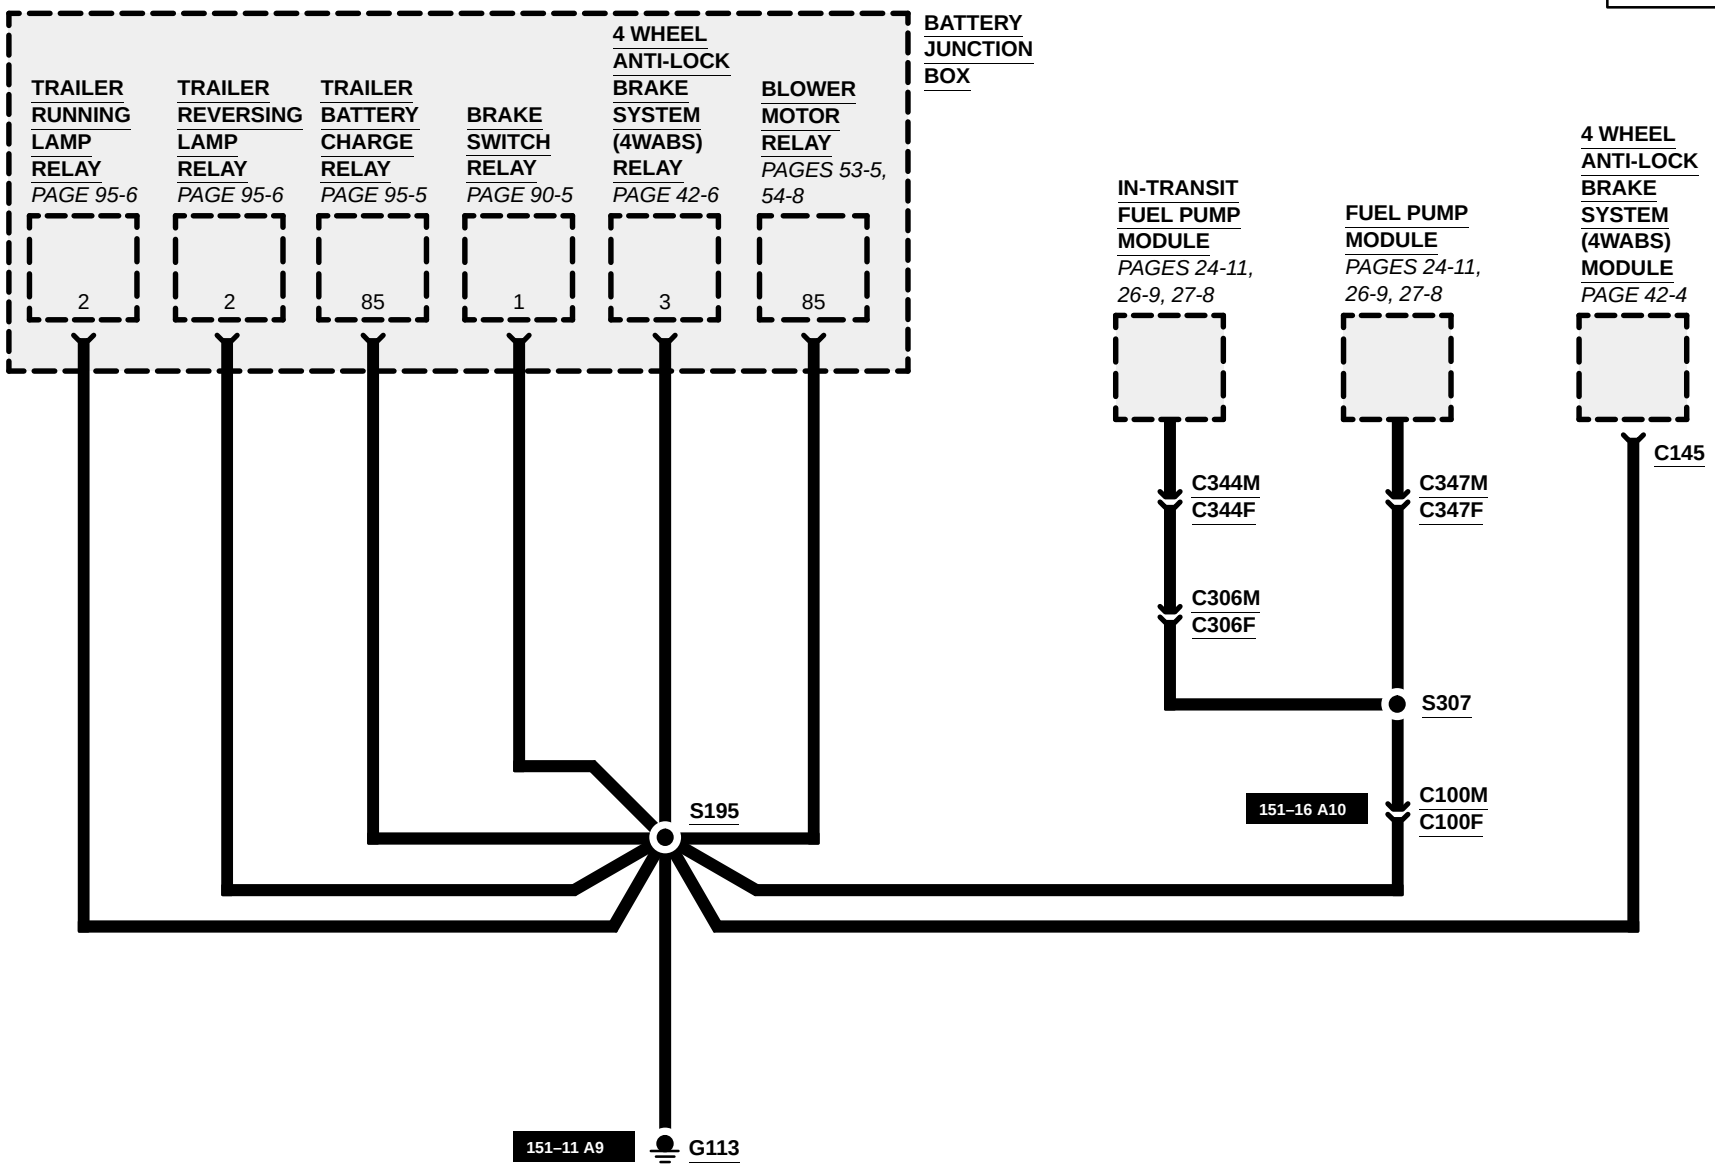
STRIPPED CHASSIS