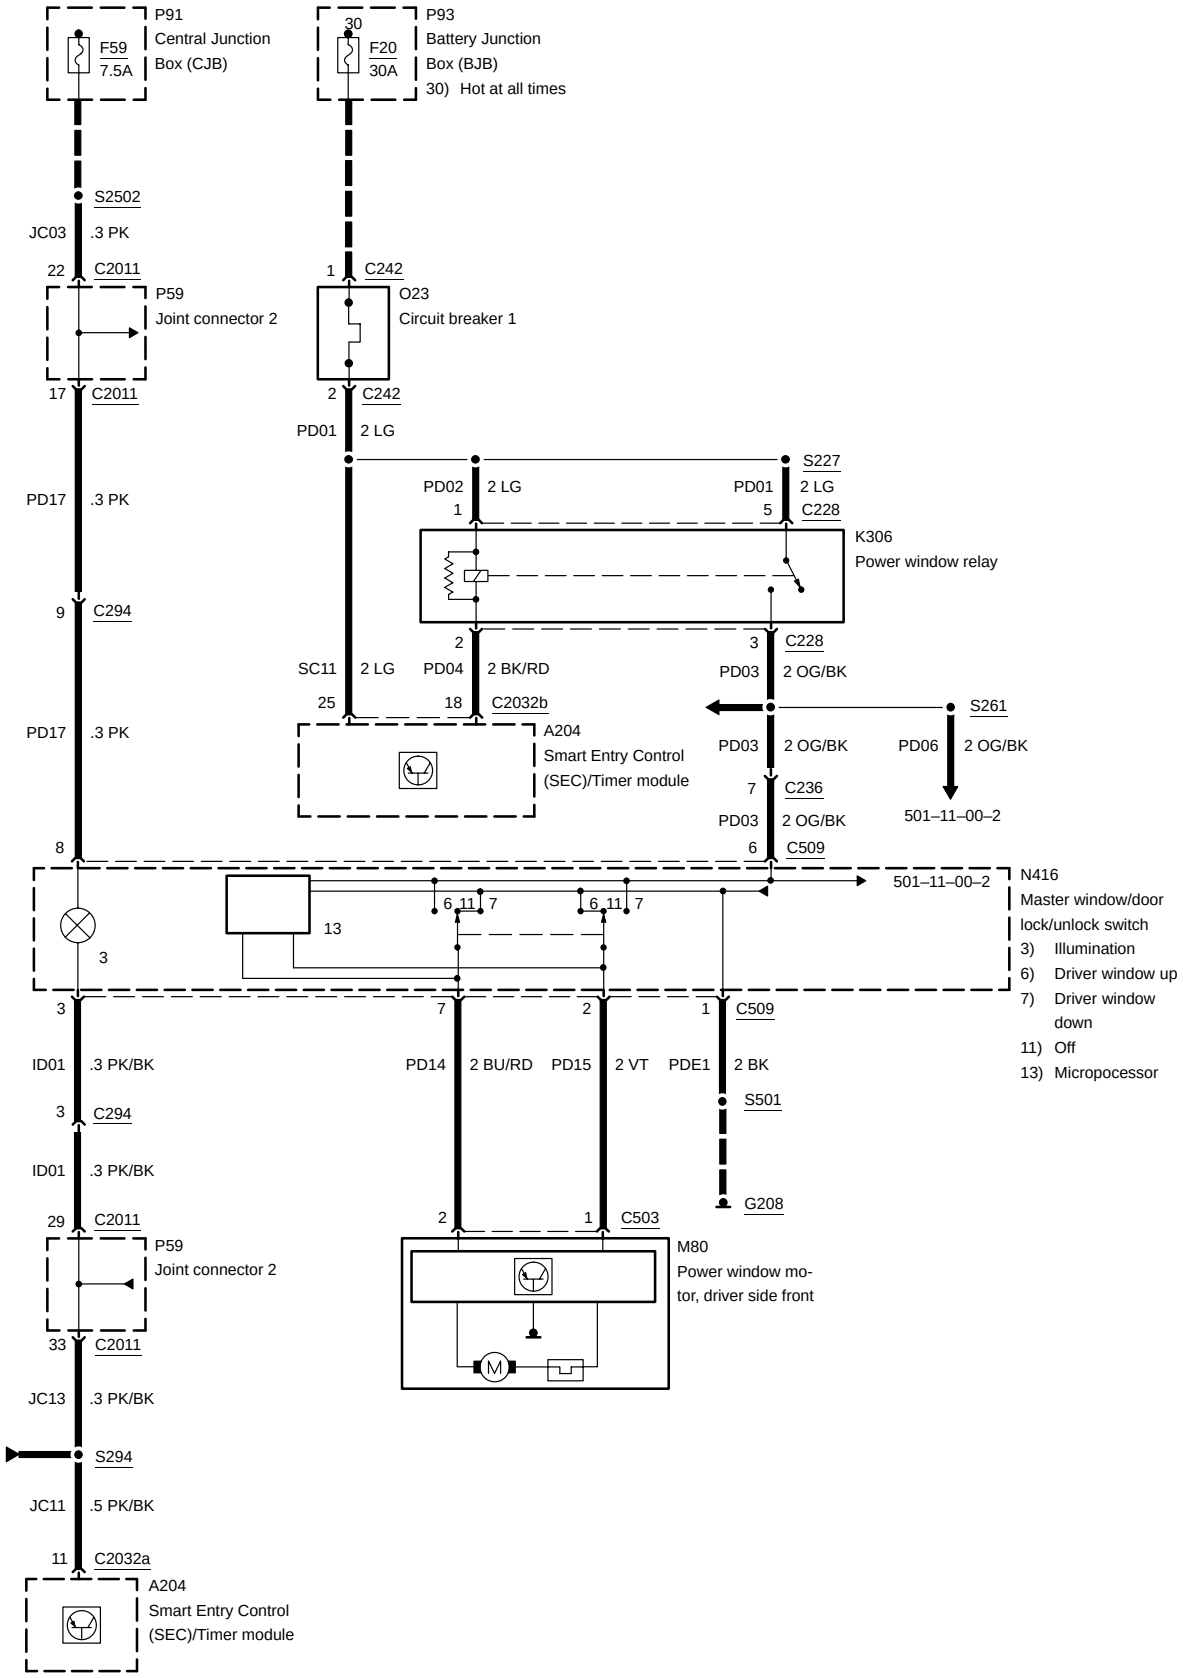front power windows -1