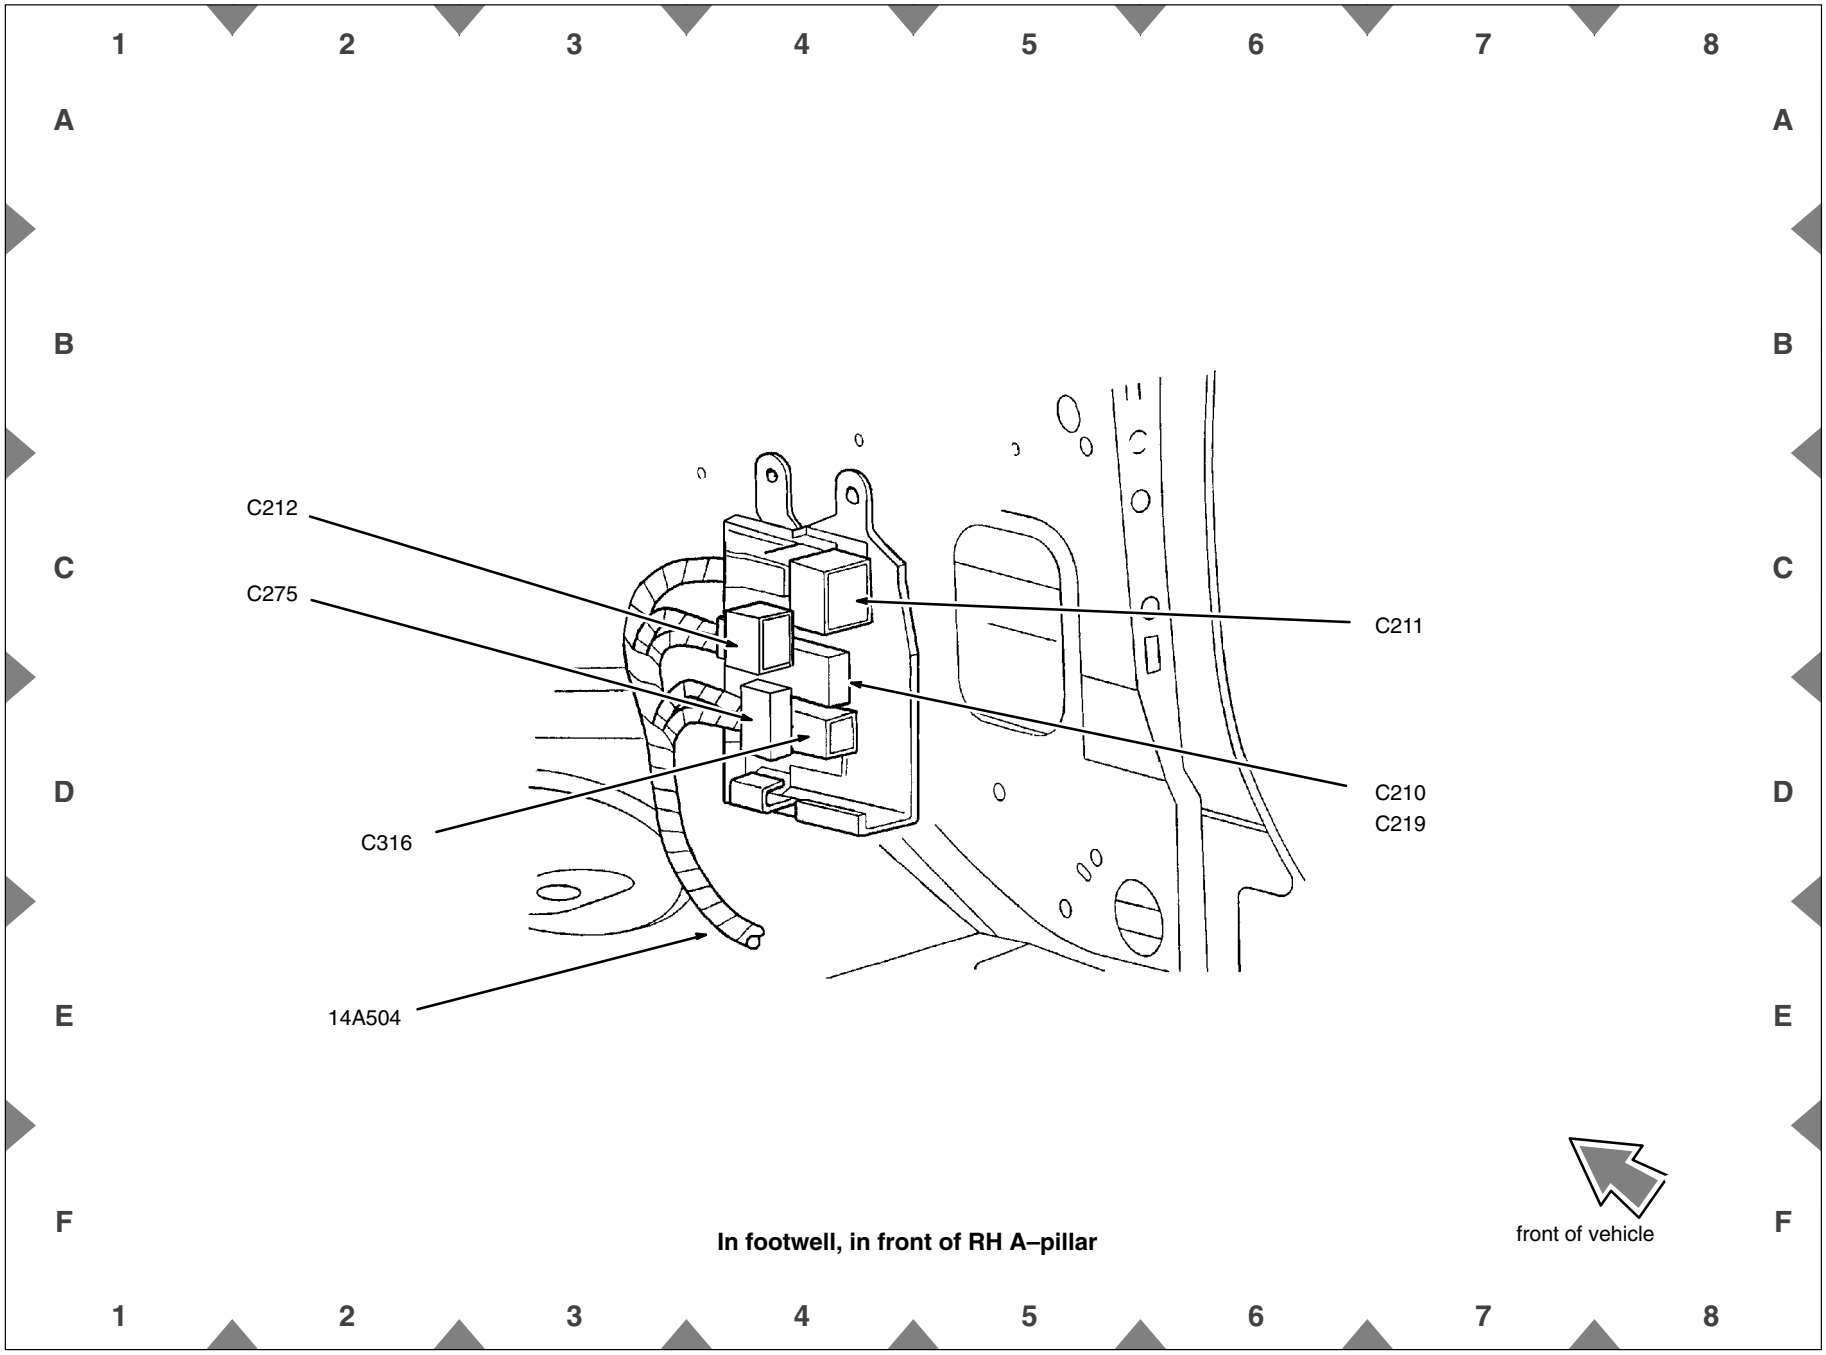

In footwell, in front of RH A–pillar