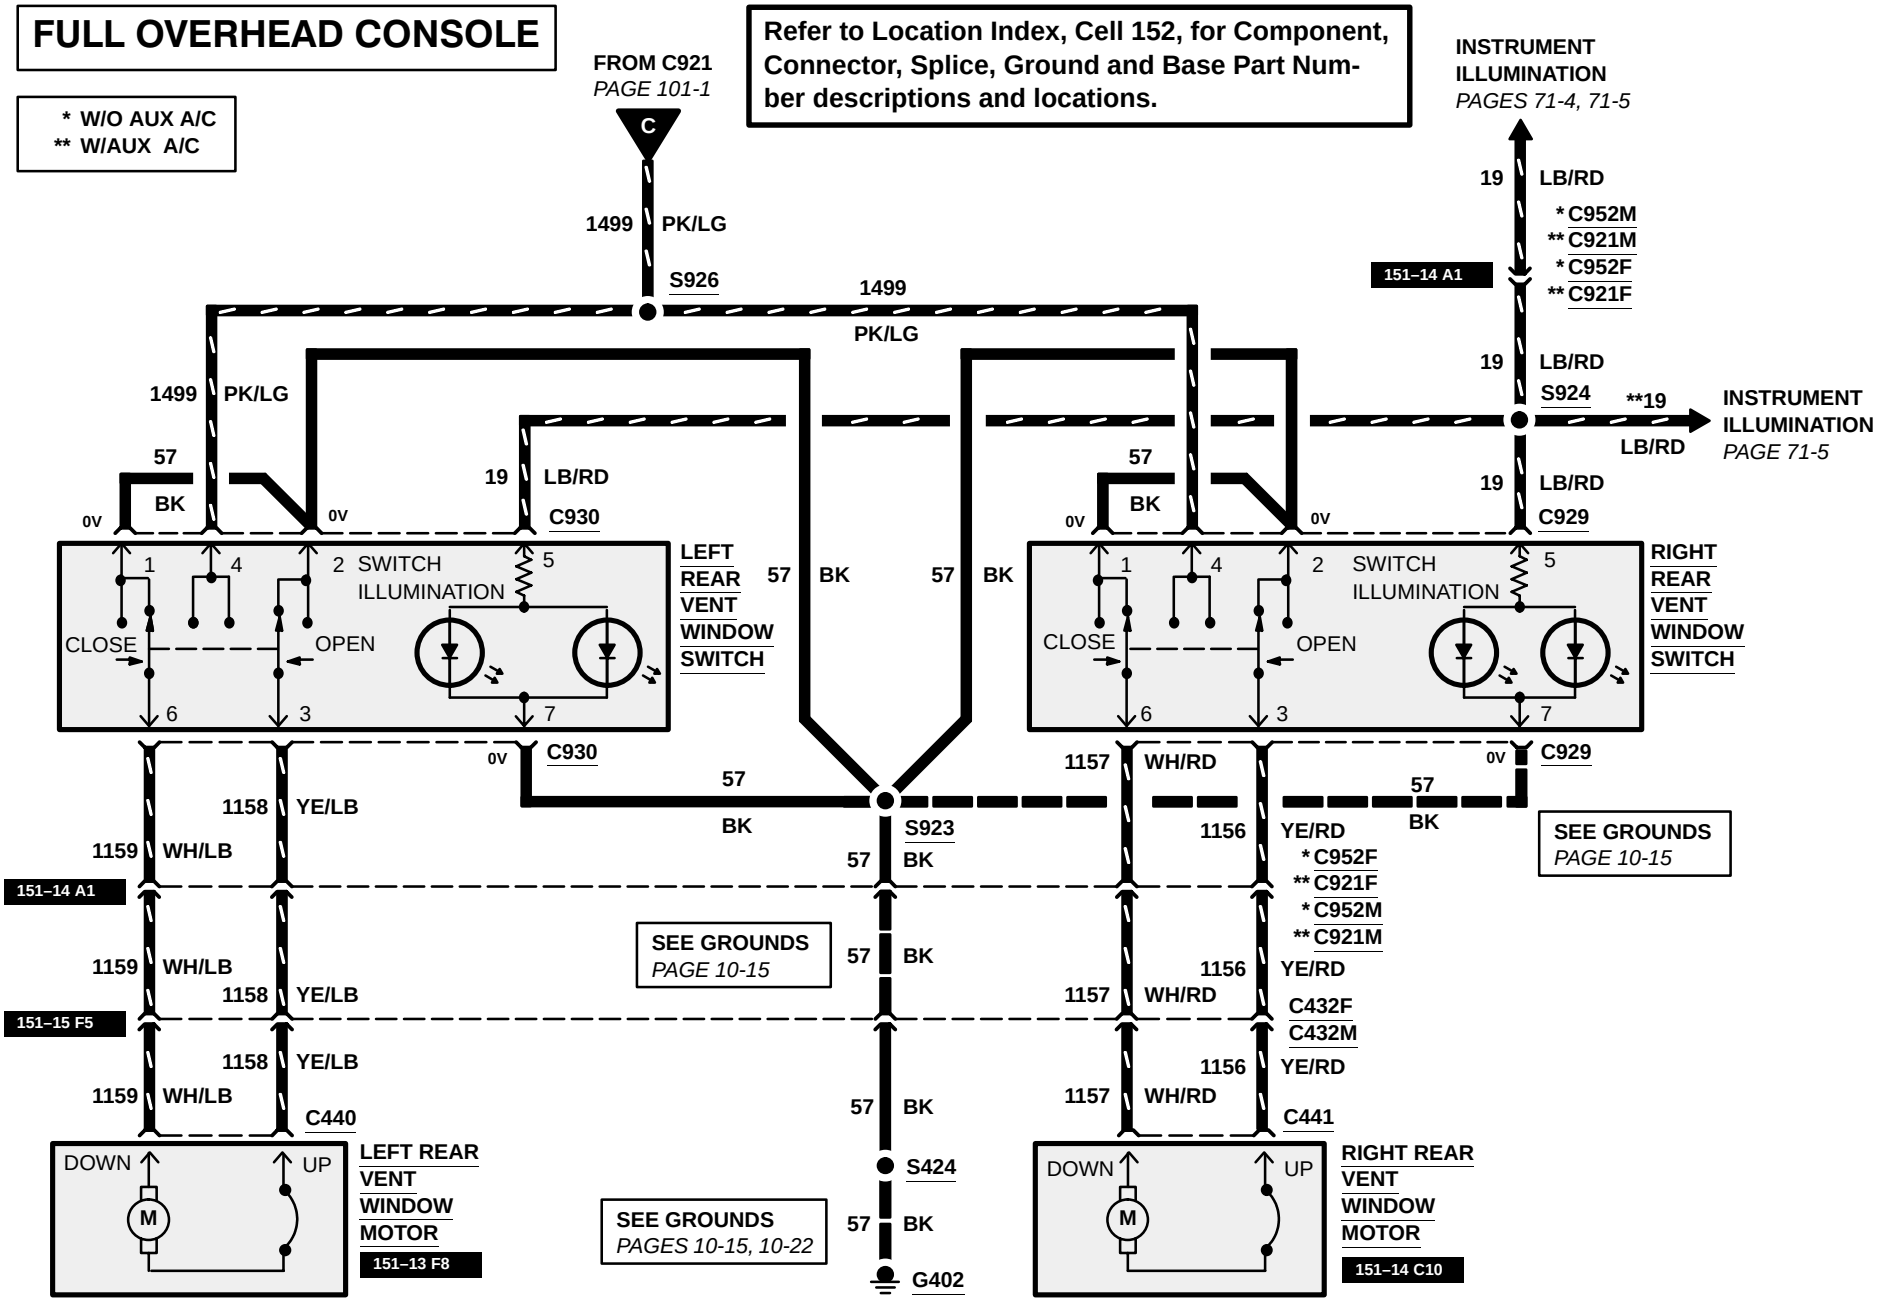101-5 ROOF OPENING PANEL/VENT WINDOWS