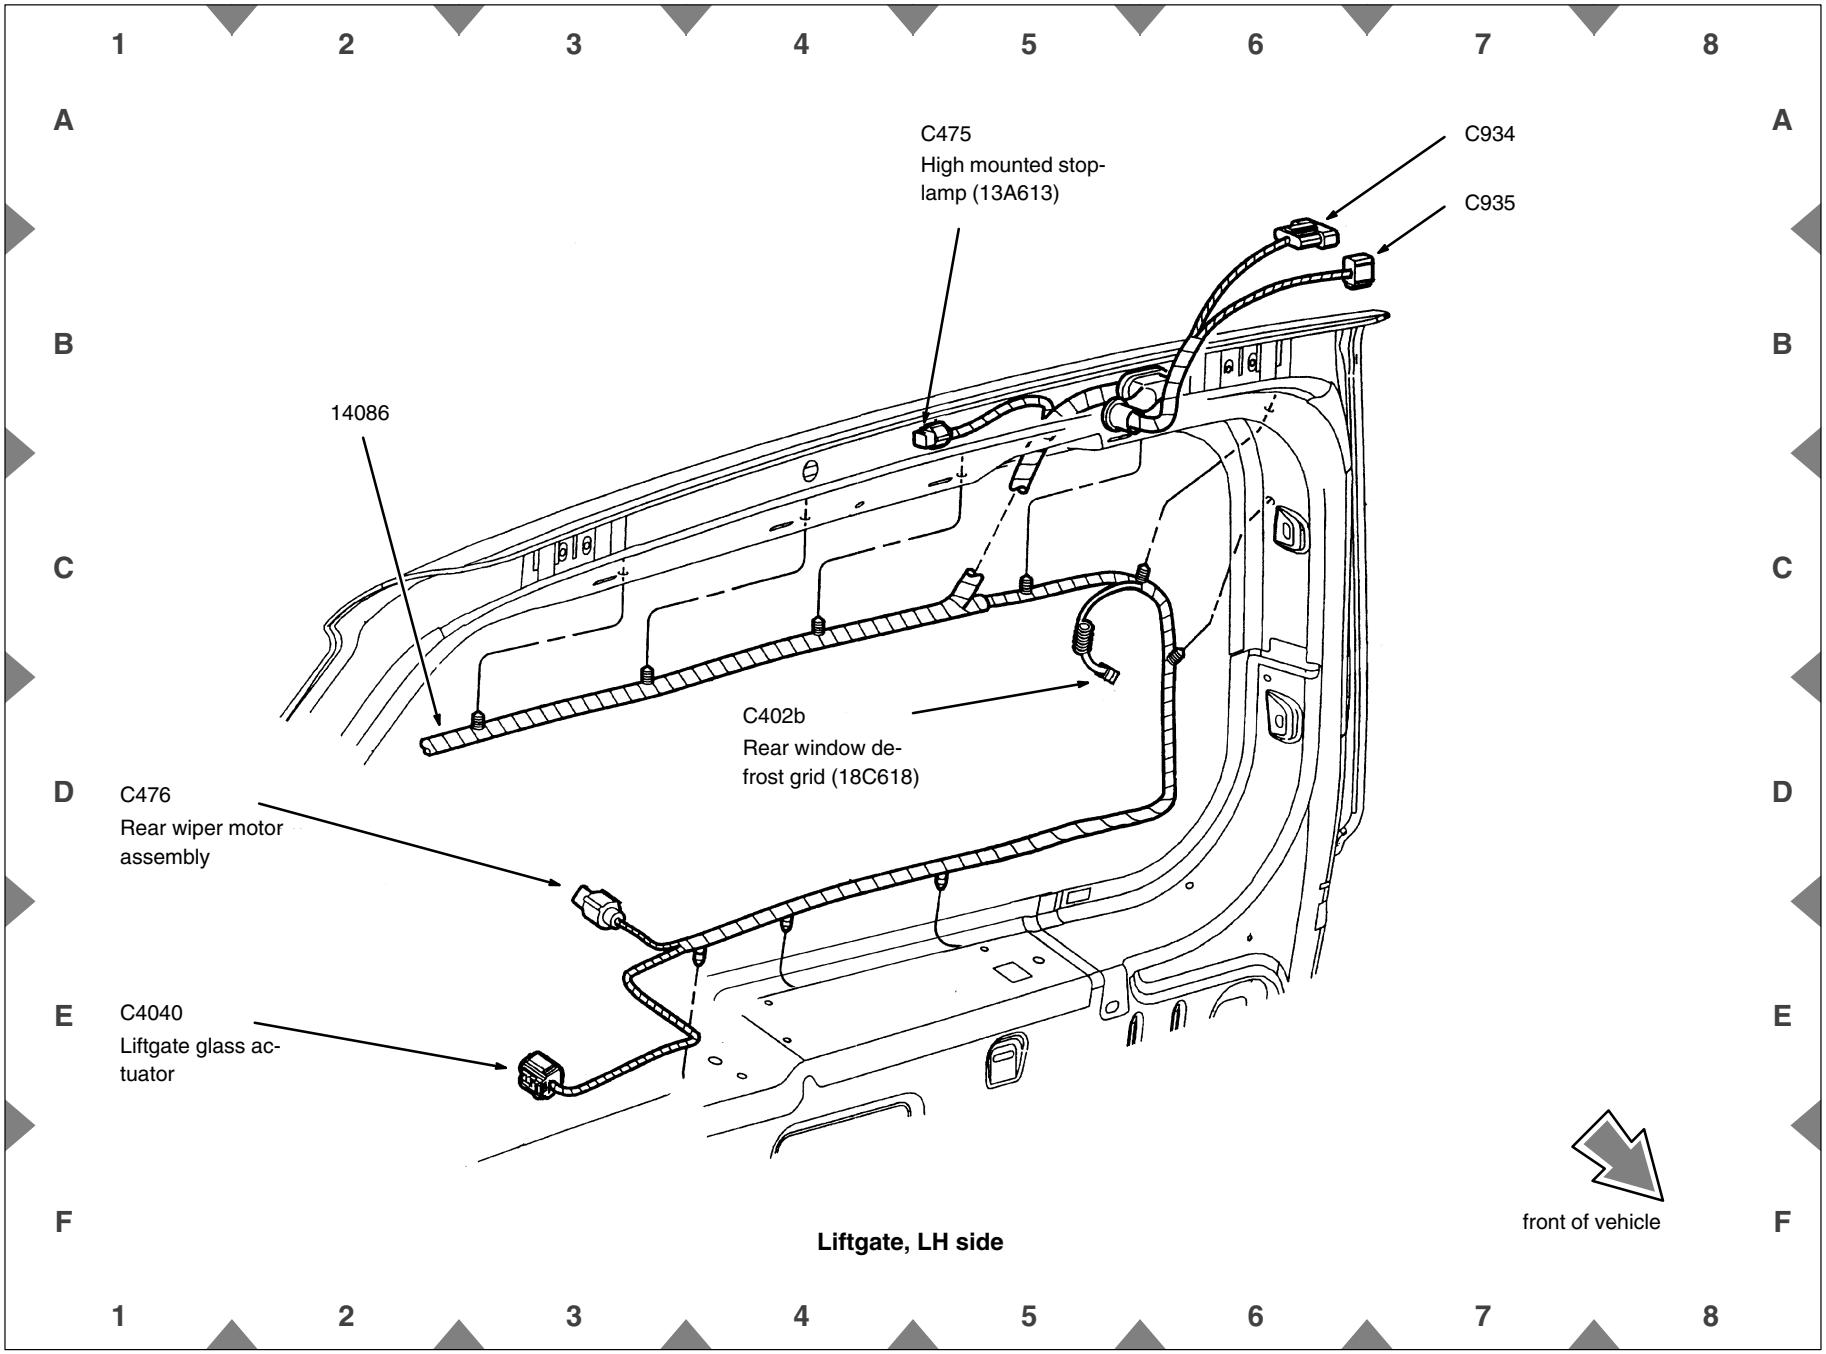


Liftgate, LH side