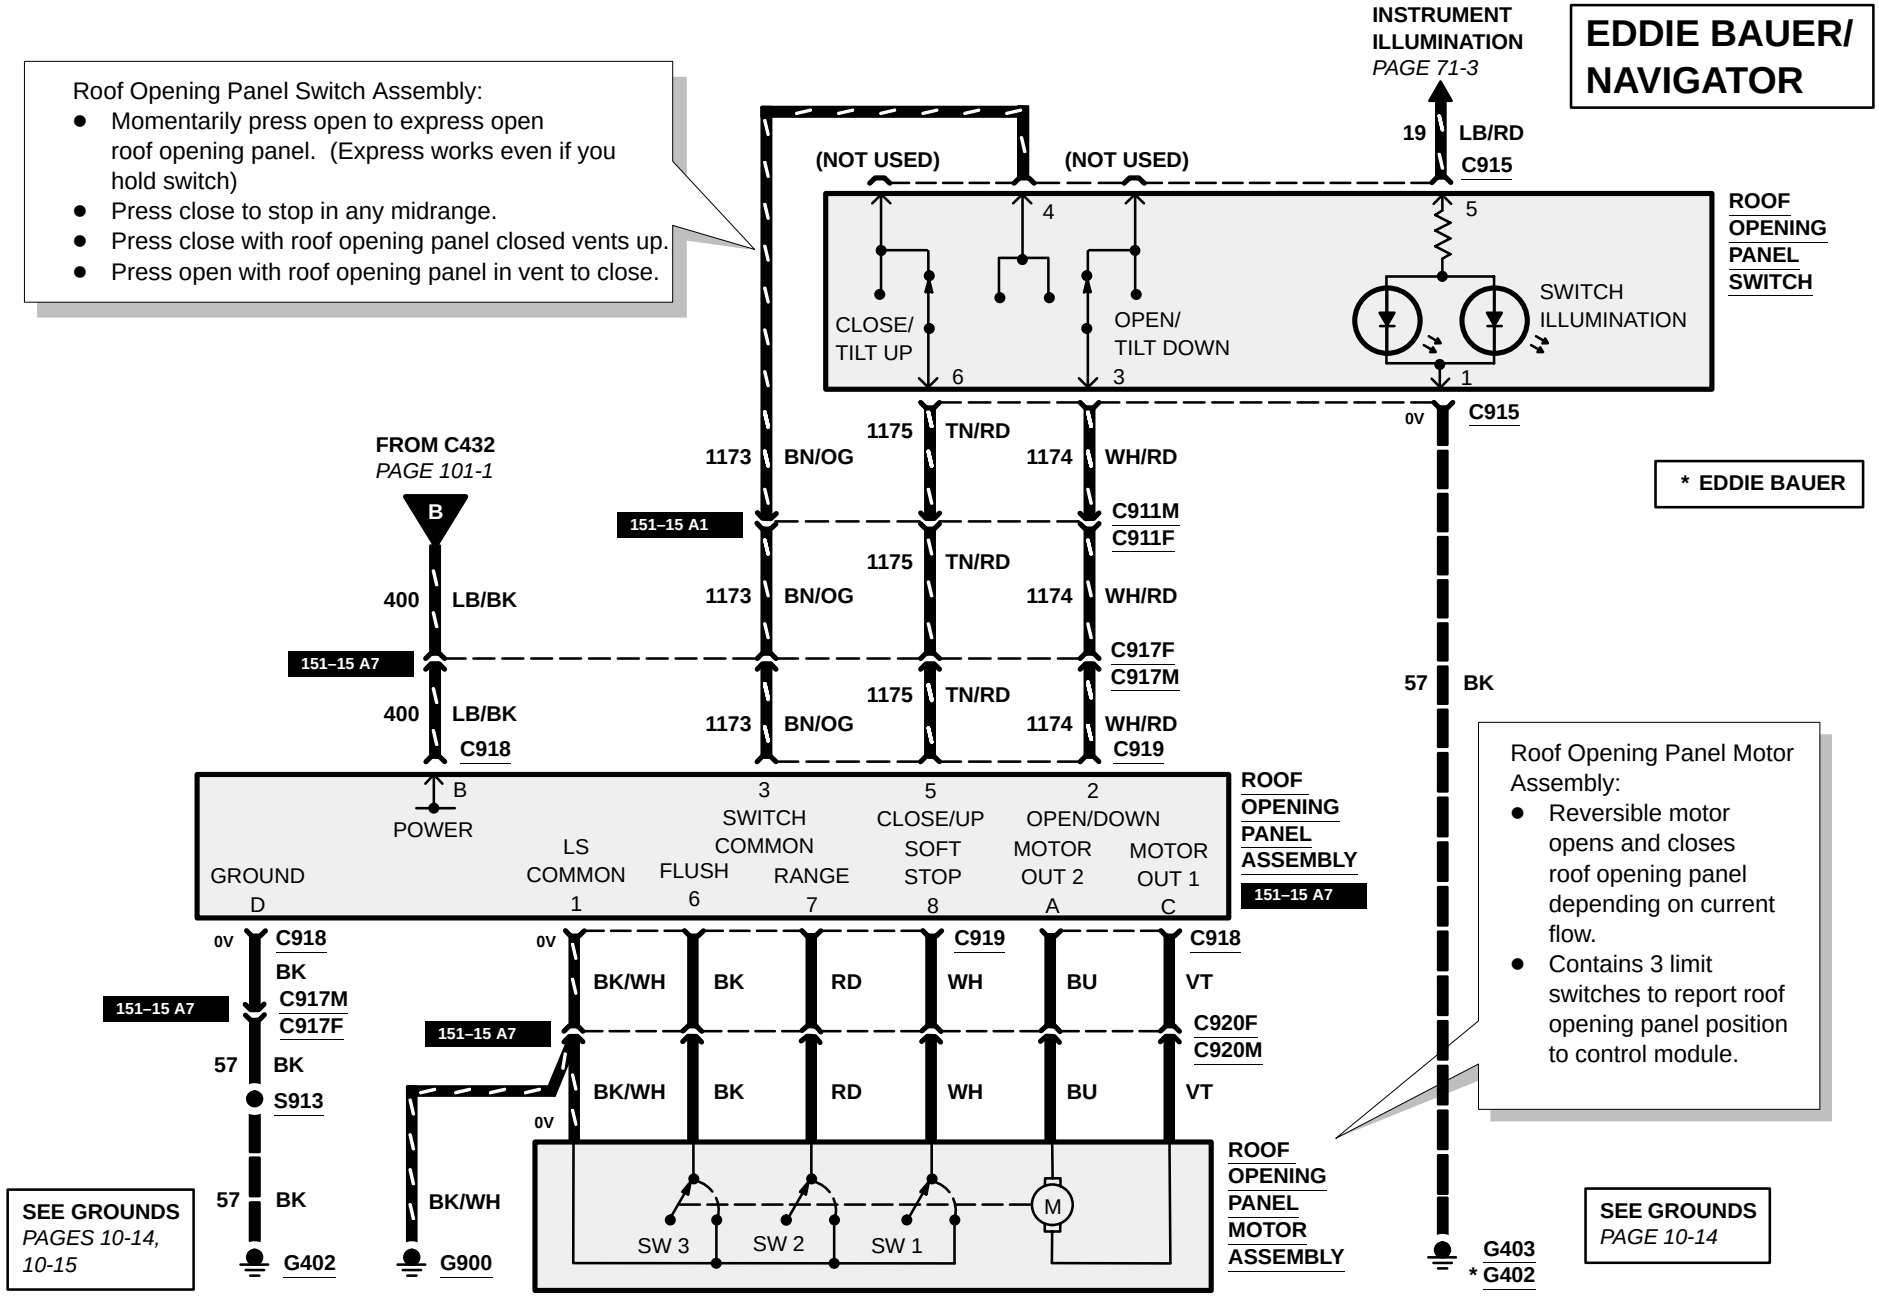101-3 ROOF OPENING PANEL/VENT WINDOWS